


EXTERIOR MOOD BOARD

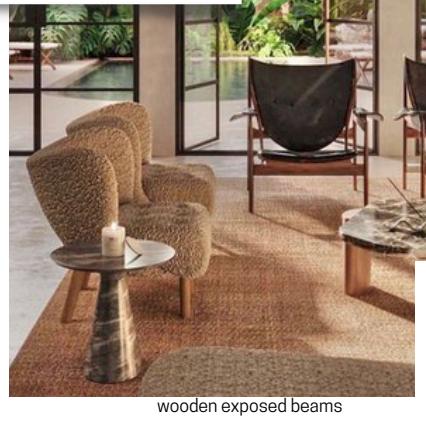

wooden exposed beams




Terracotta roof tiles



Stucco walls




Natural stones

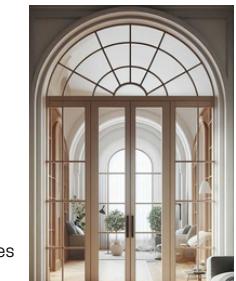

Arched doors




Ironwork light fixtures

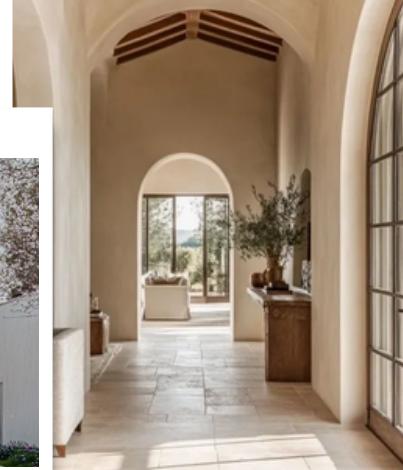


MINIMAL MODERN

MEDITERRANEAN

GROUP 12: NOURAN AHMED - MARIAM ISMAIL - HAZEM KHALED

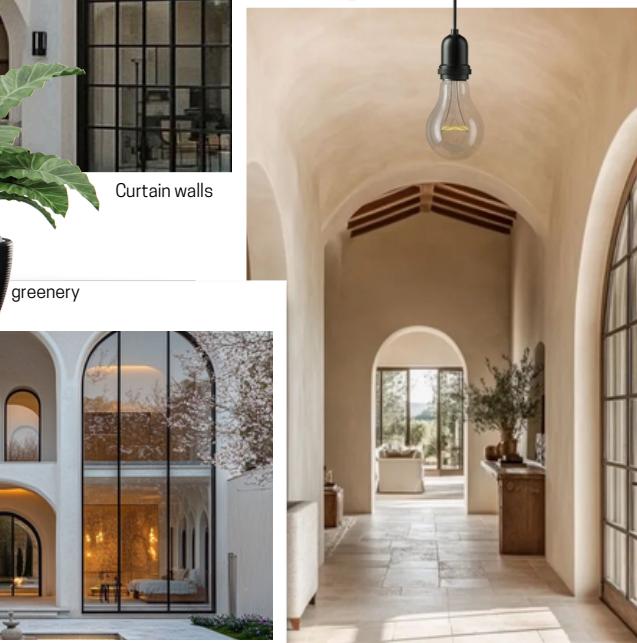


Arched openings

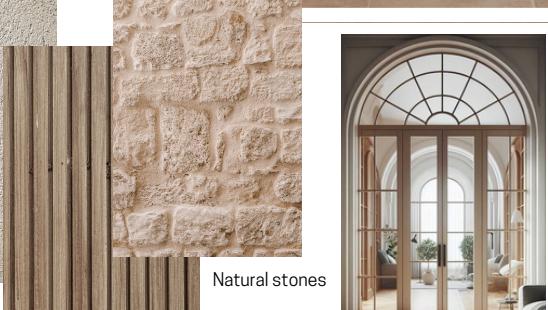

wooden exposed beams,
sheds and claddings

INTERIOR MOOD BOARD

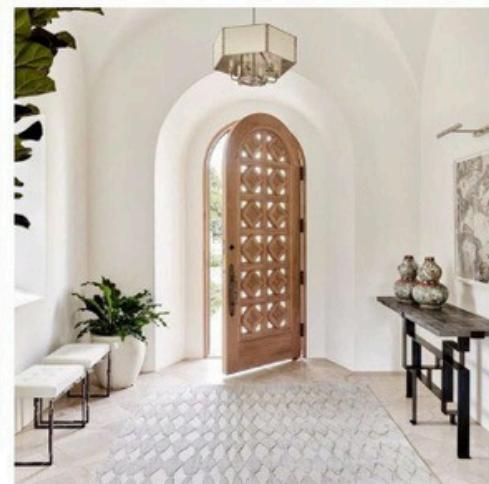

mediterranean







FLOORING MOODBOARD





CEILING MOODBOARD

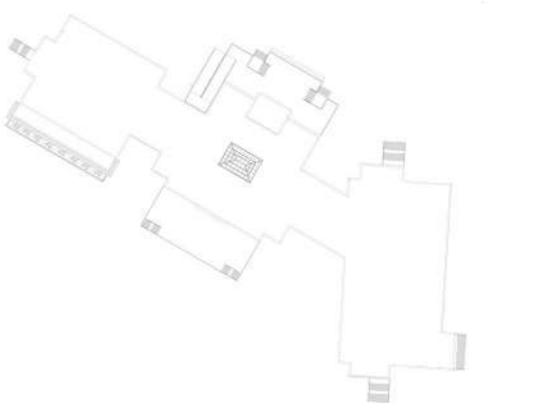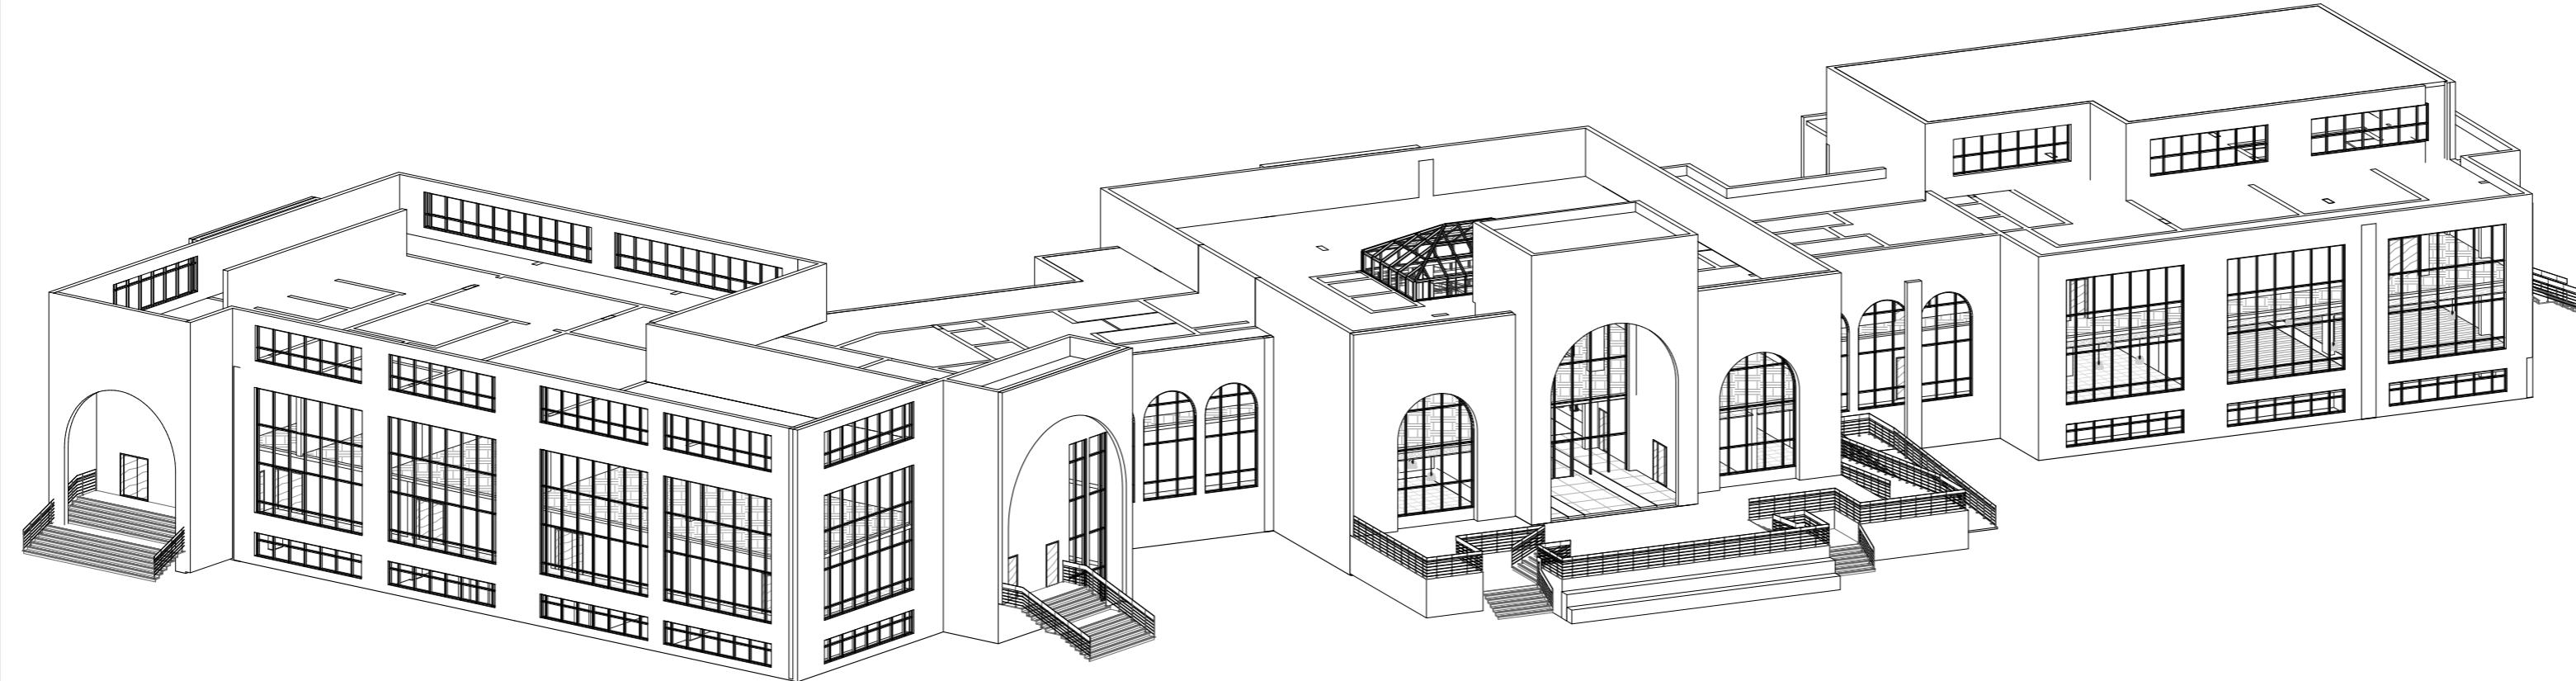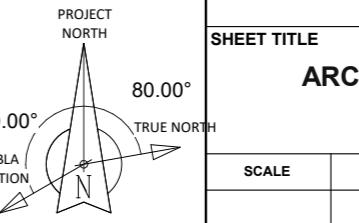



	1	2	3	4	5	6	7	8	9	10	11	12	13		
														CONSULTANT	
														HELWAN UNIVERSITY 	
														OWNER	
														 FAP Fine Arts Programs	
														CONTRACTOR	
														 SAUD Sustainable Architecture and Urban Design Program	
														REMARKS	
														KEY PLAN: 	
														REV DATE ISSUED FOR DRW CHK TL PM STUDENT INFORMATION Mariam Ismail Nouran Ahmed Hazem Khaled	
														PROJECT DATA MIXED USE BUILDING	
														DISCIPLINE ARCHITECTURE	
														SHEET TITLE ARCHITECTURAL COVER SHEET	
														SCALE SHEET NO REV MARK AI001	
A	B	C	D	E	F	G	H	I	J	K	L	M	N		
															
HOTEL BUILDING															
Presented to: DR. Hossam Sabry, TA. Adham Yasser															
SHEET SIZE - ISO A1 (841*594 MM) 100 mm 50 mm 10 mm Scanning scale															
															
1 2 3 4 5 6 7 8 9 10 11 12 13															

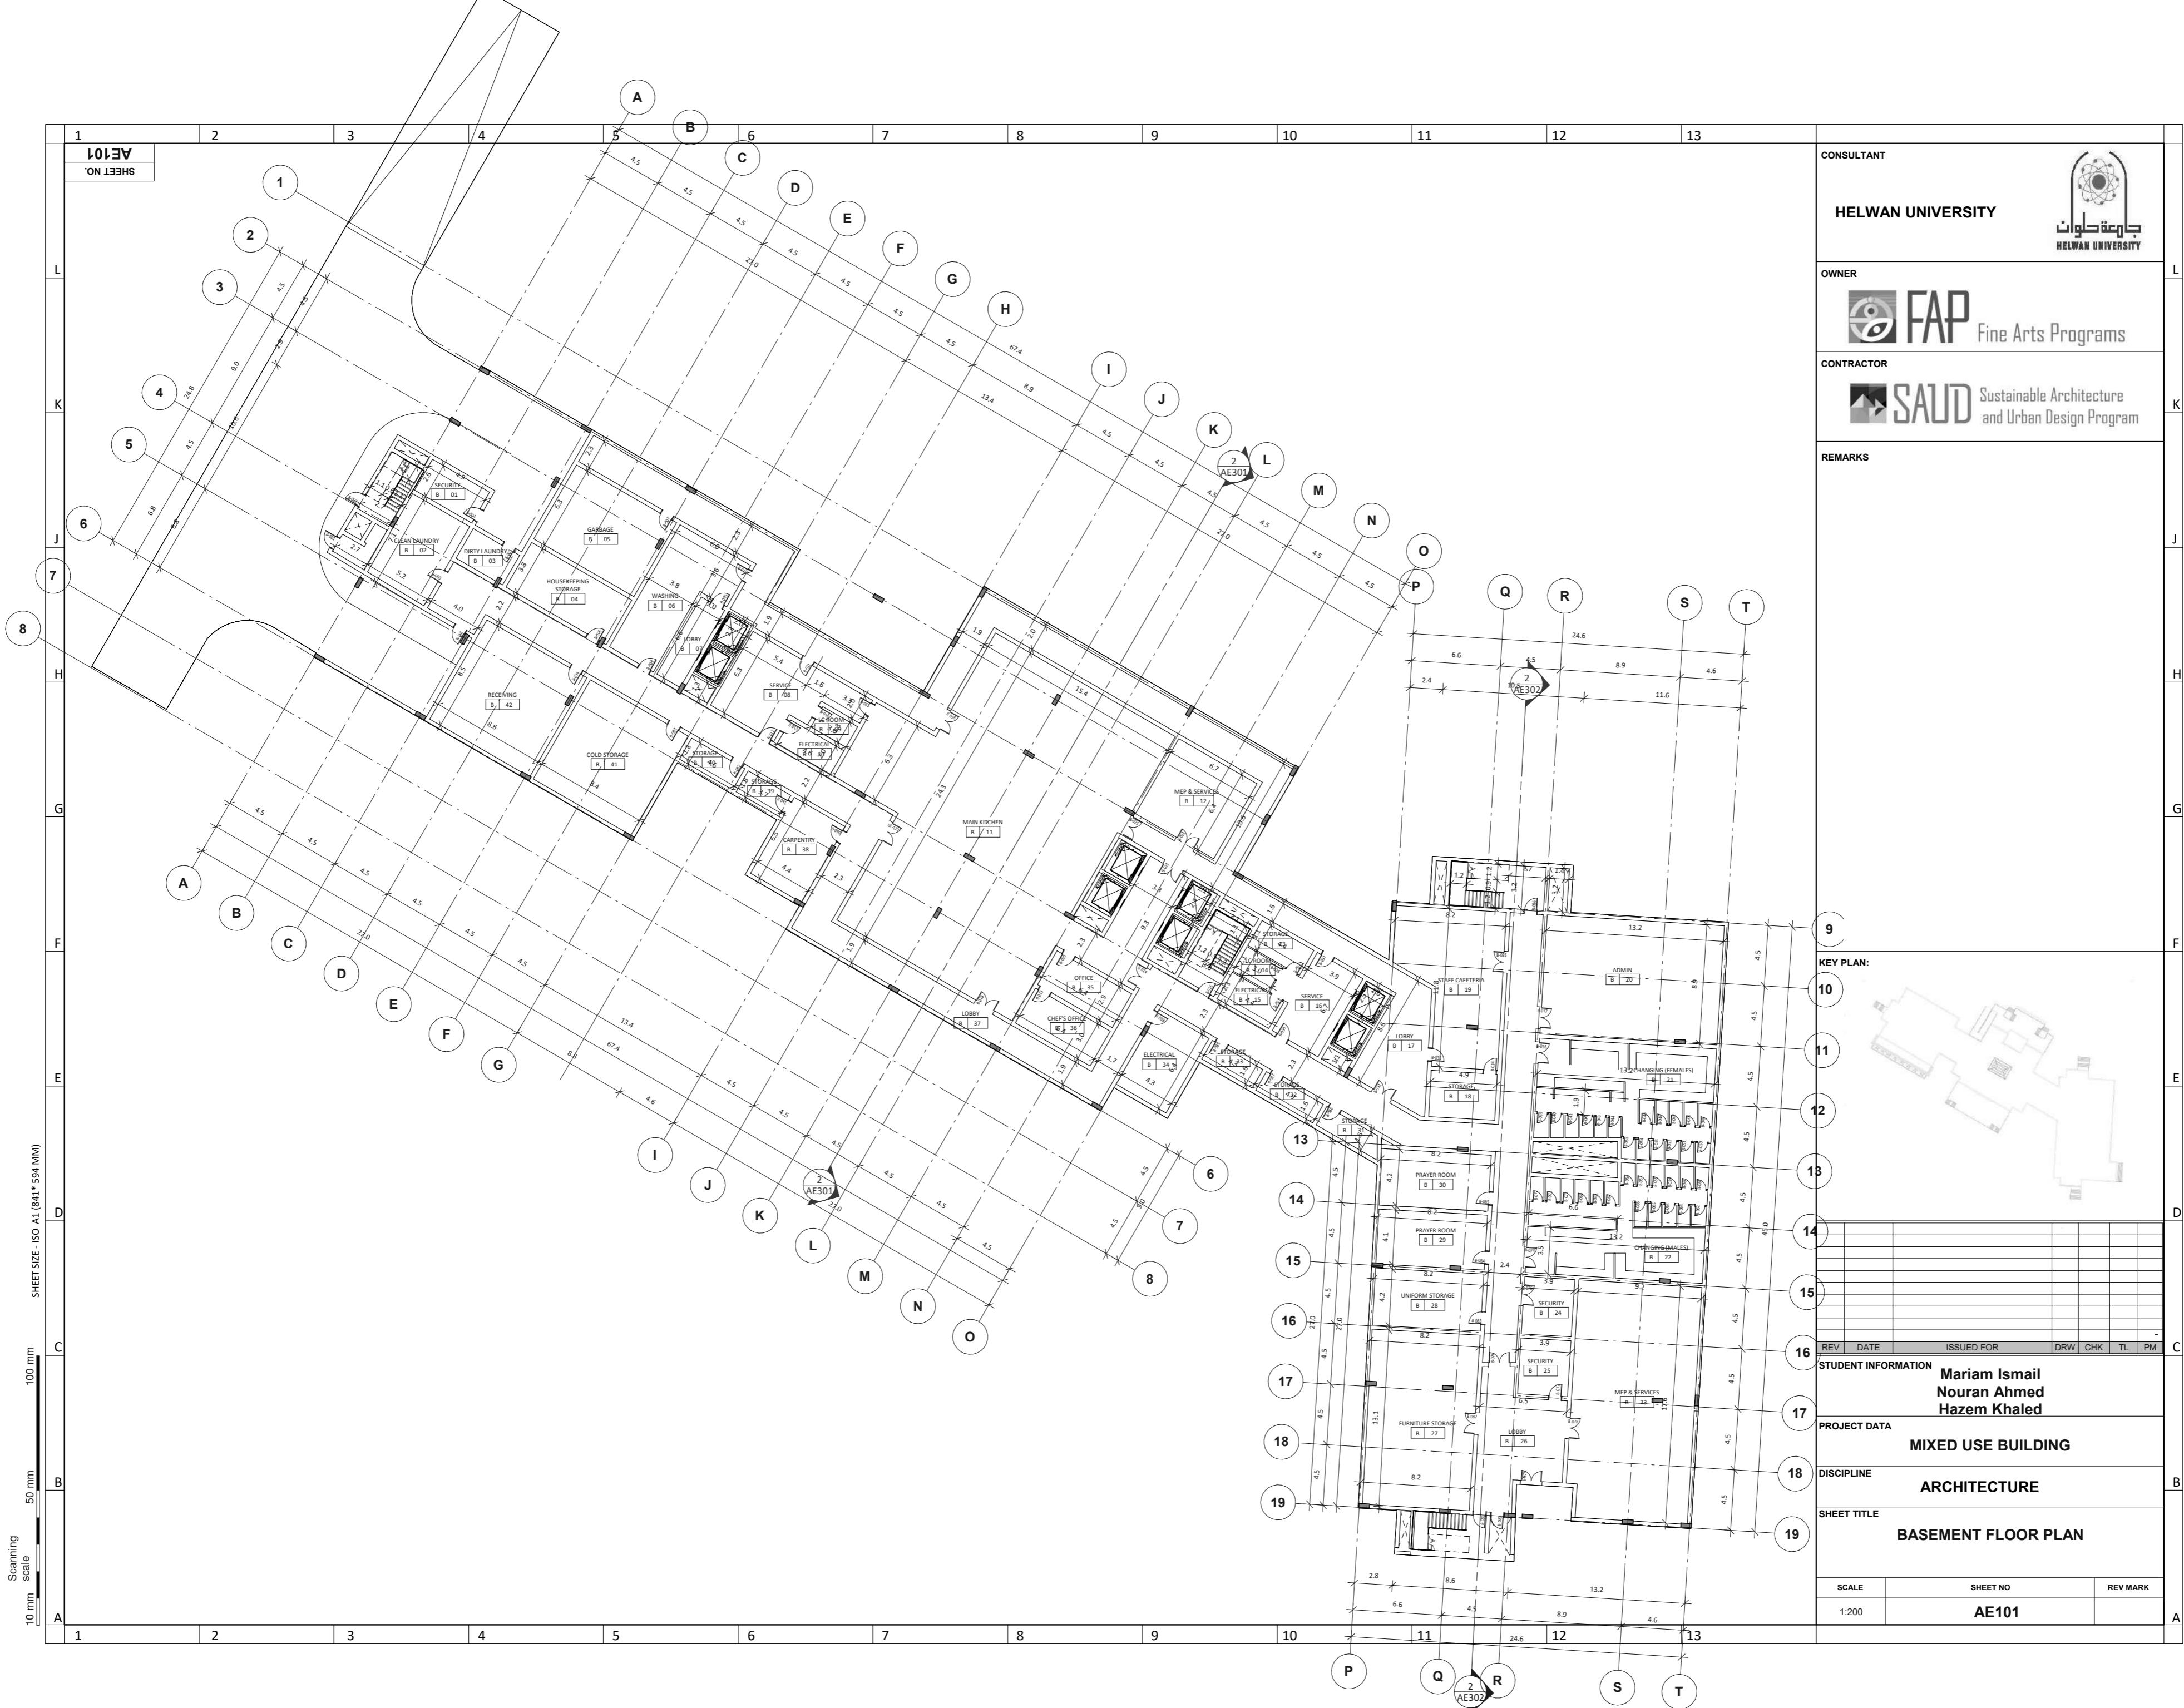

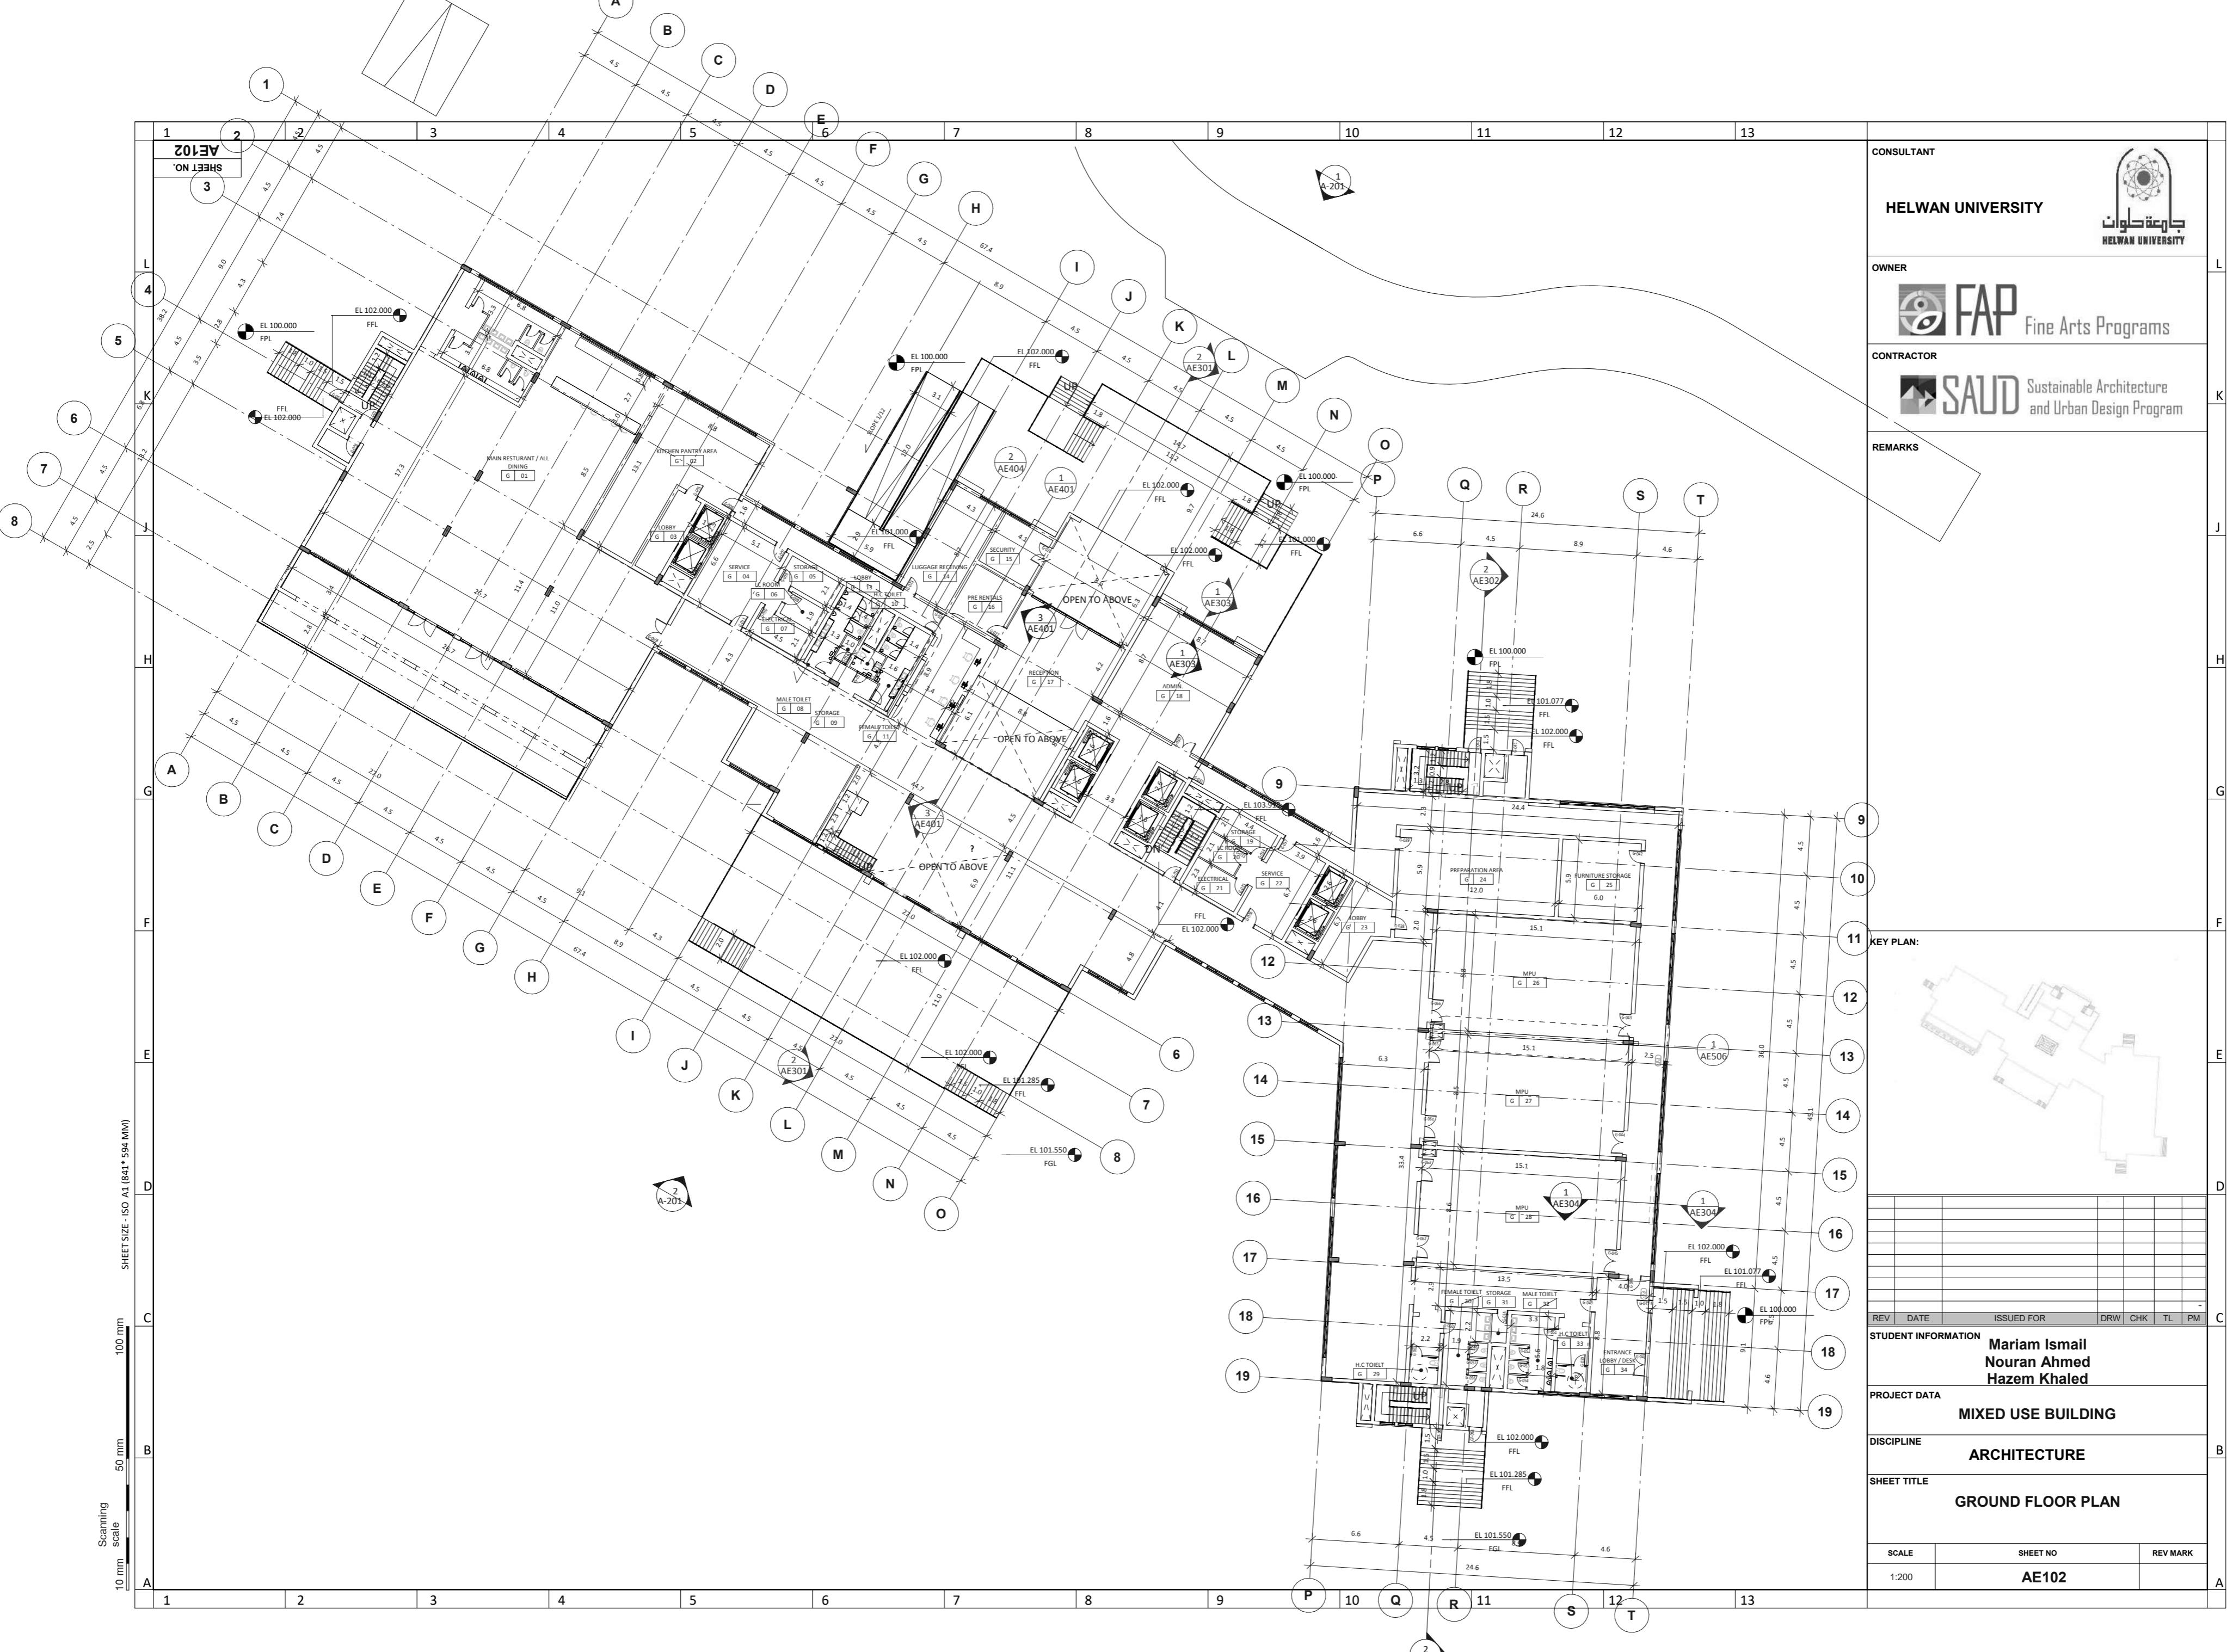

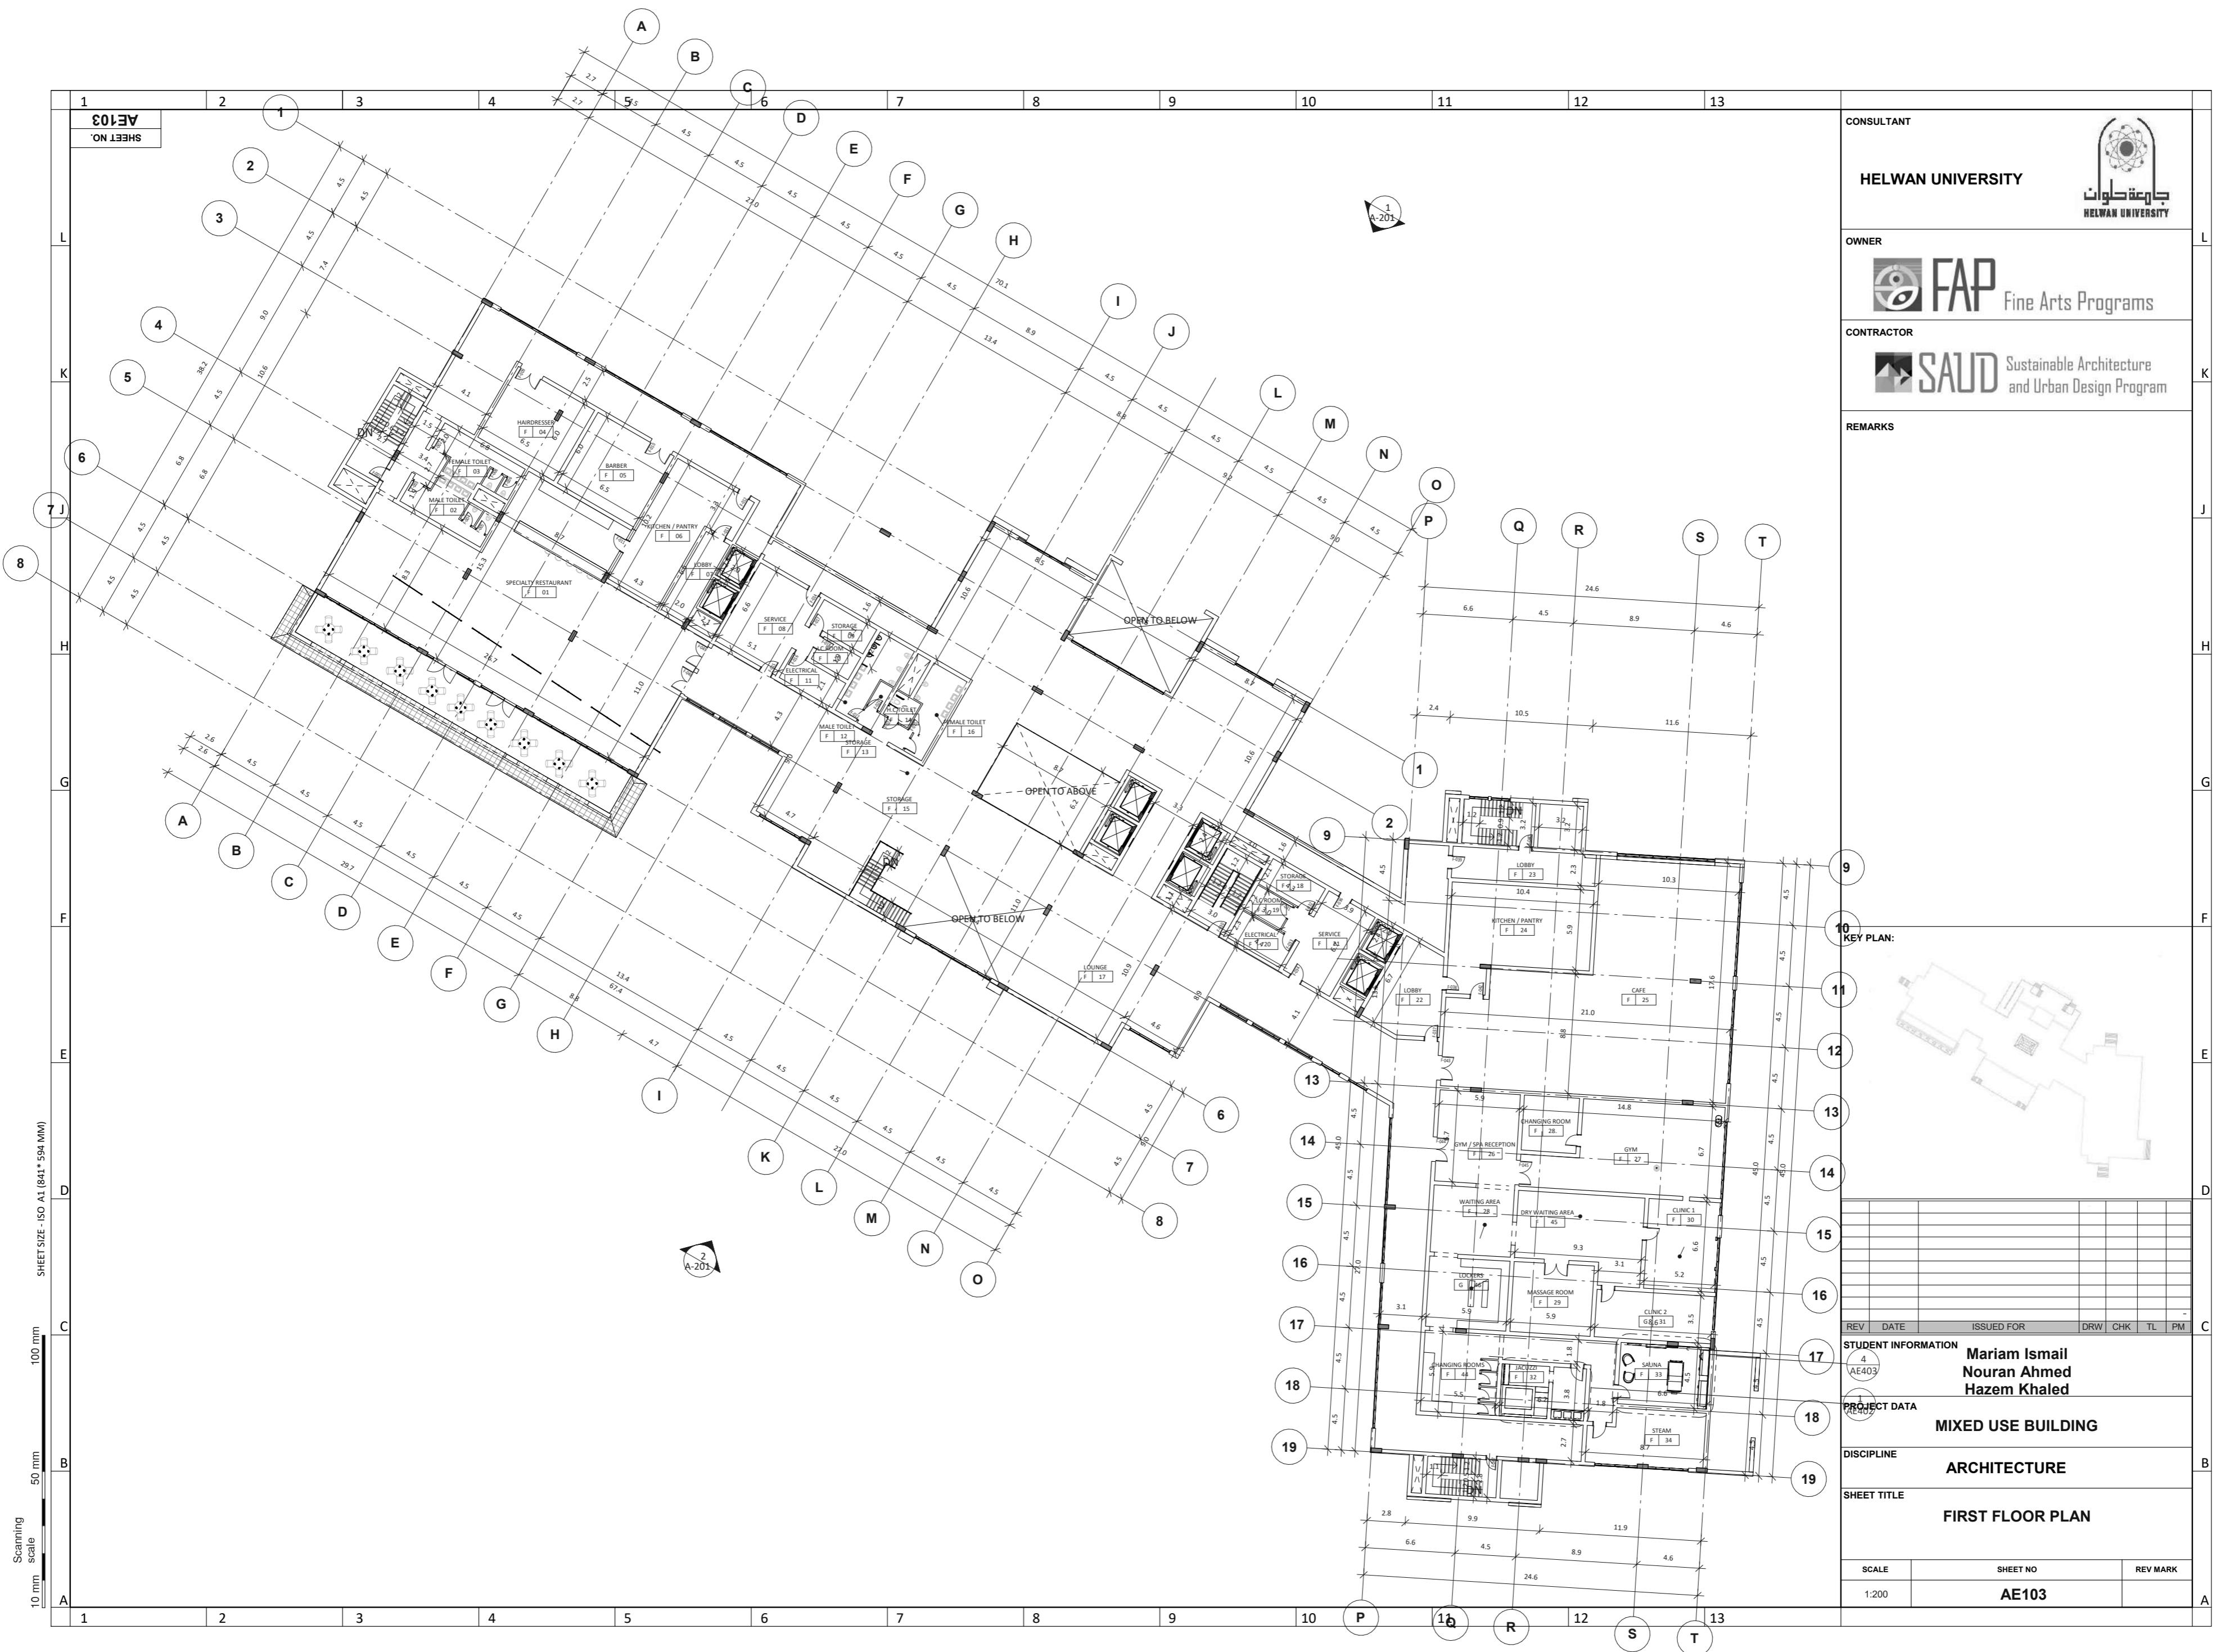

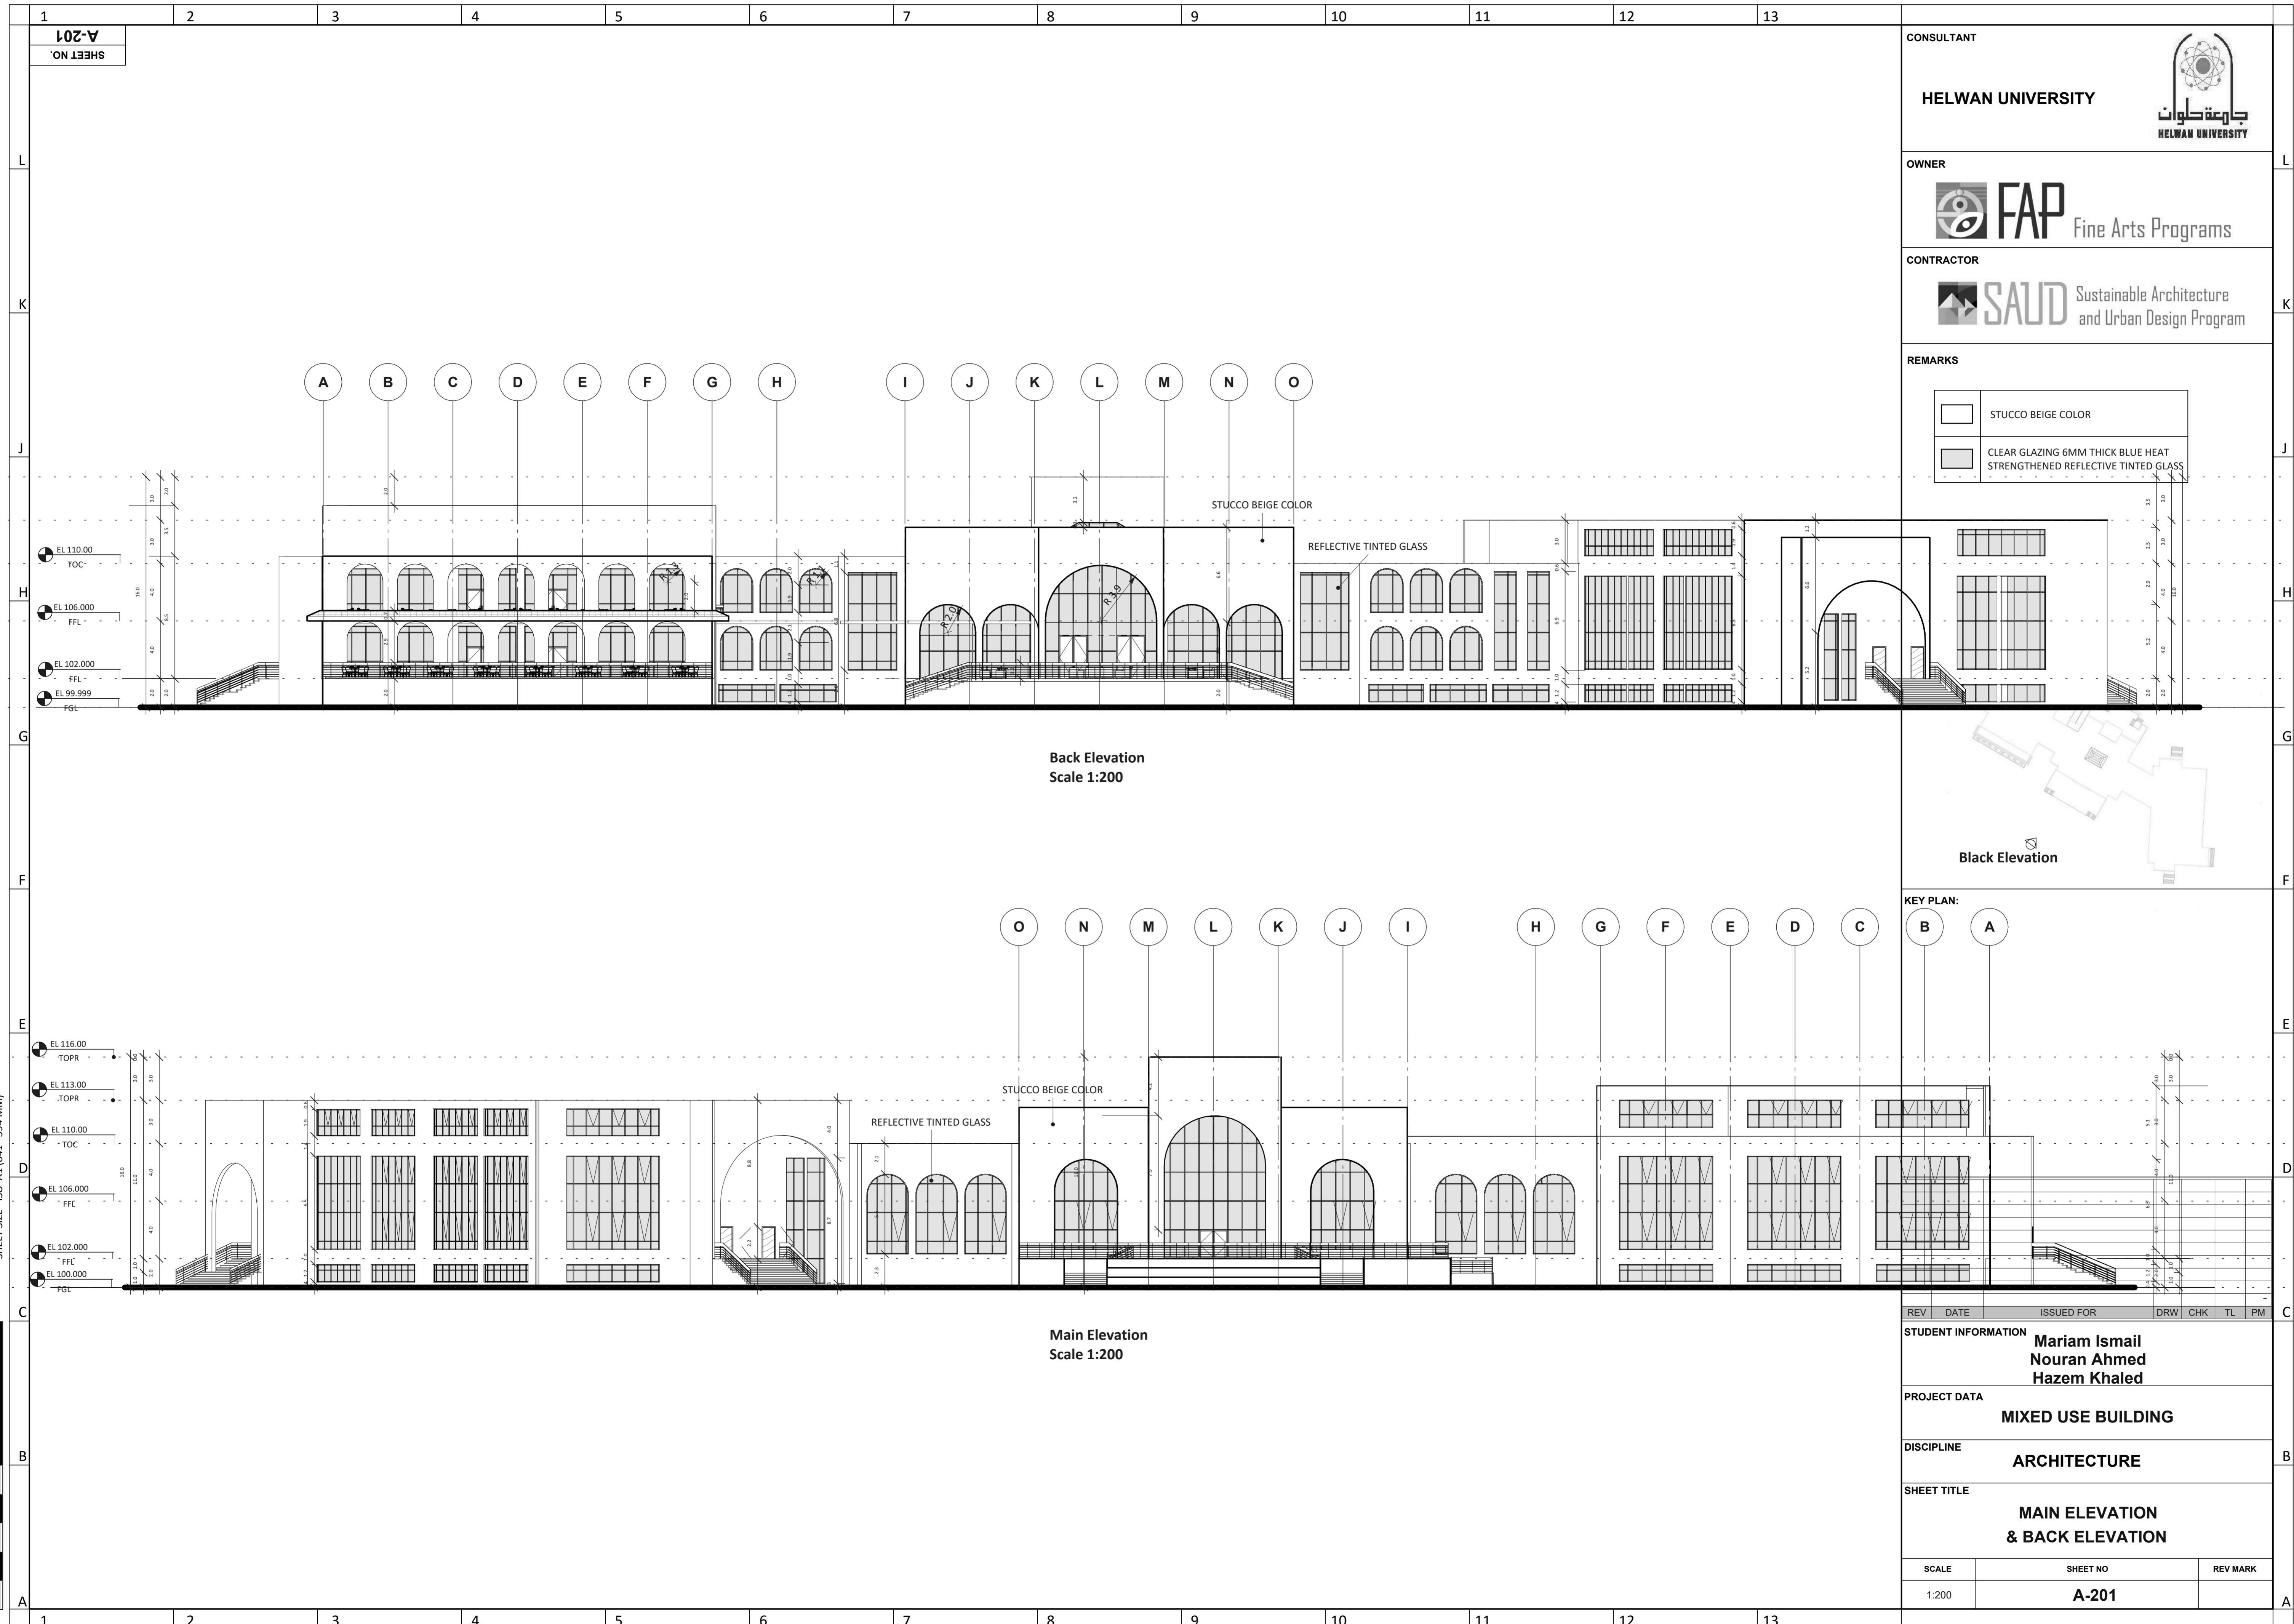

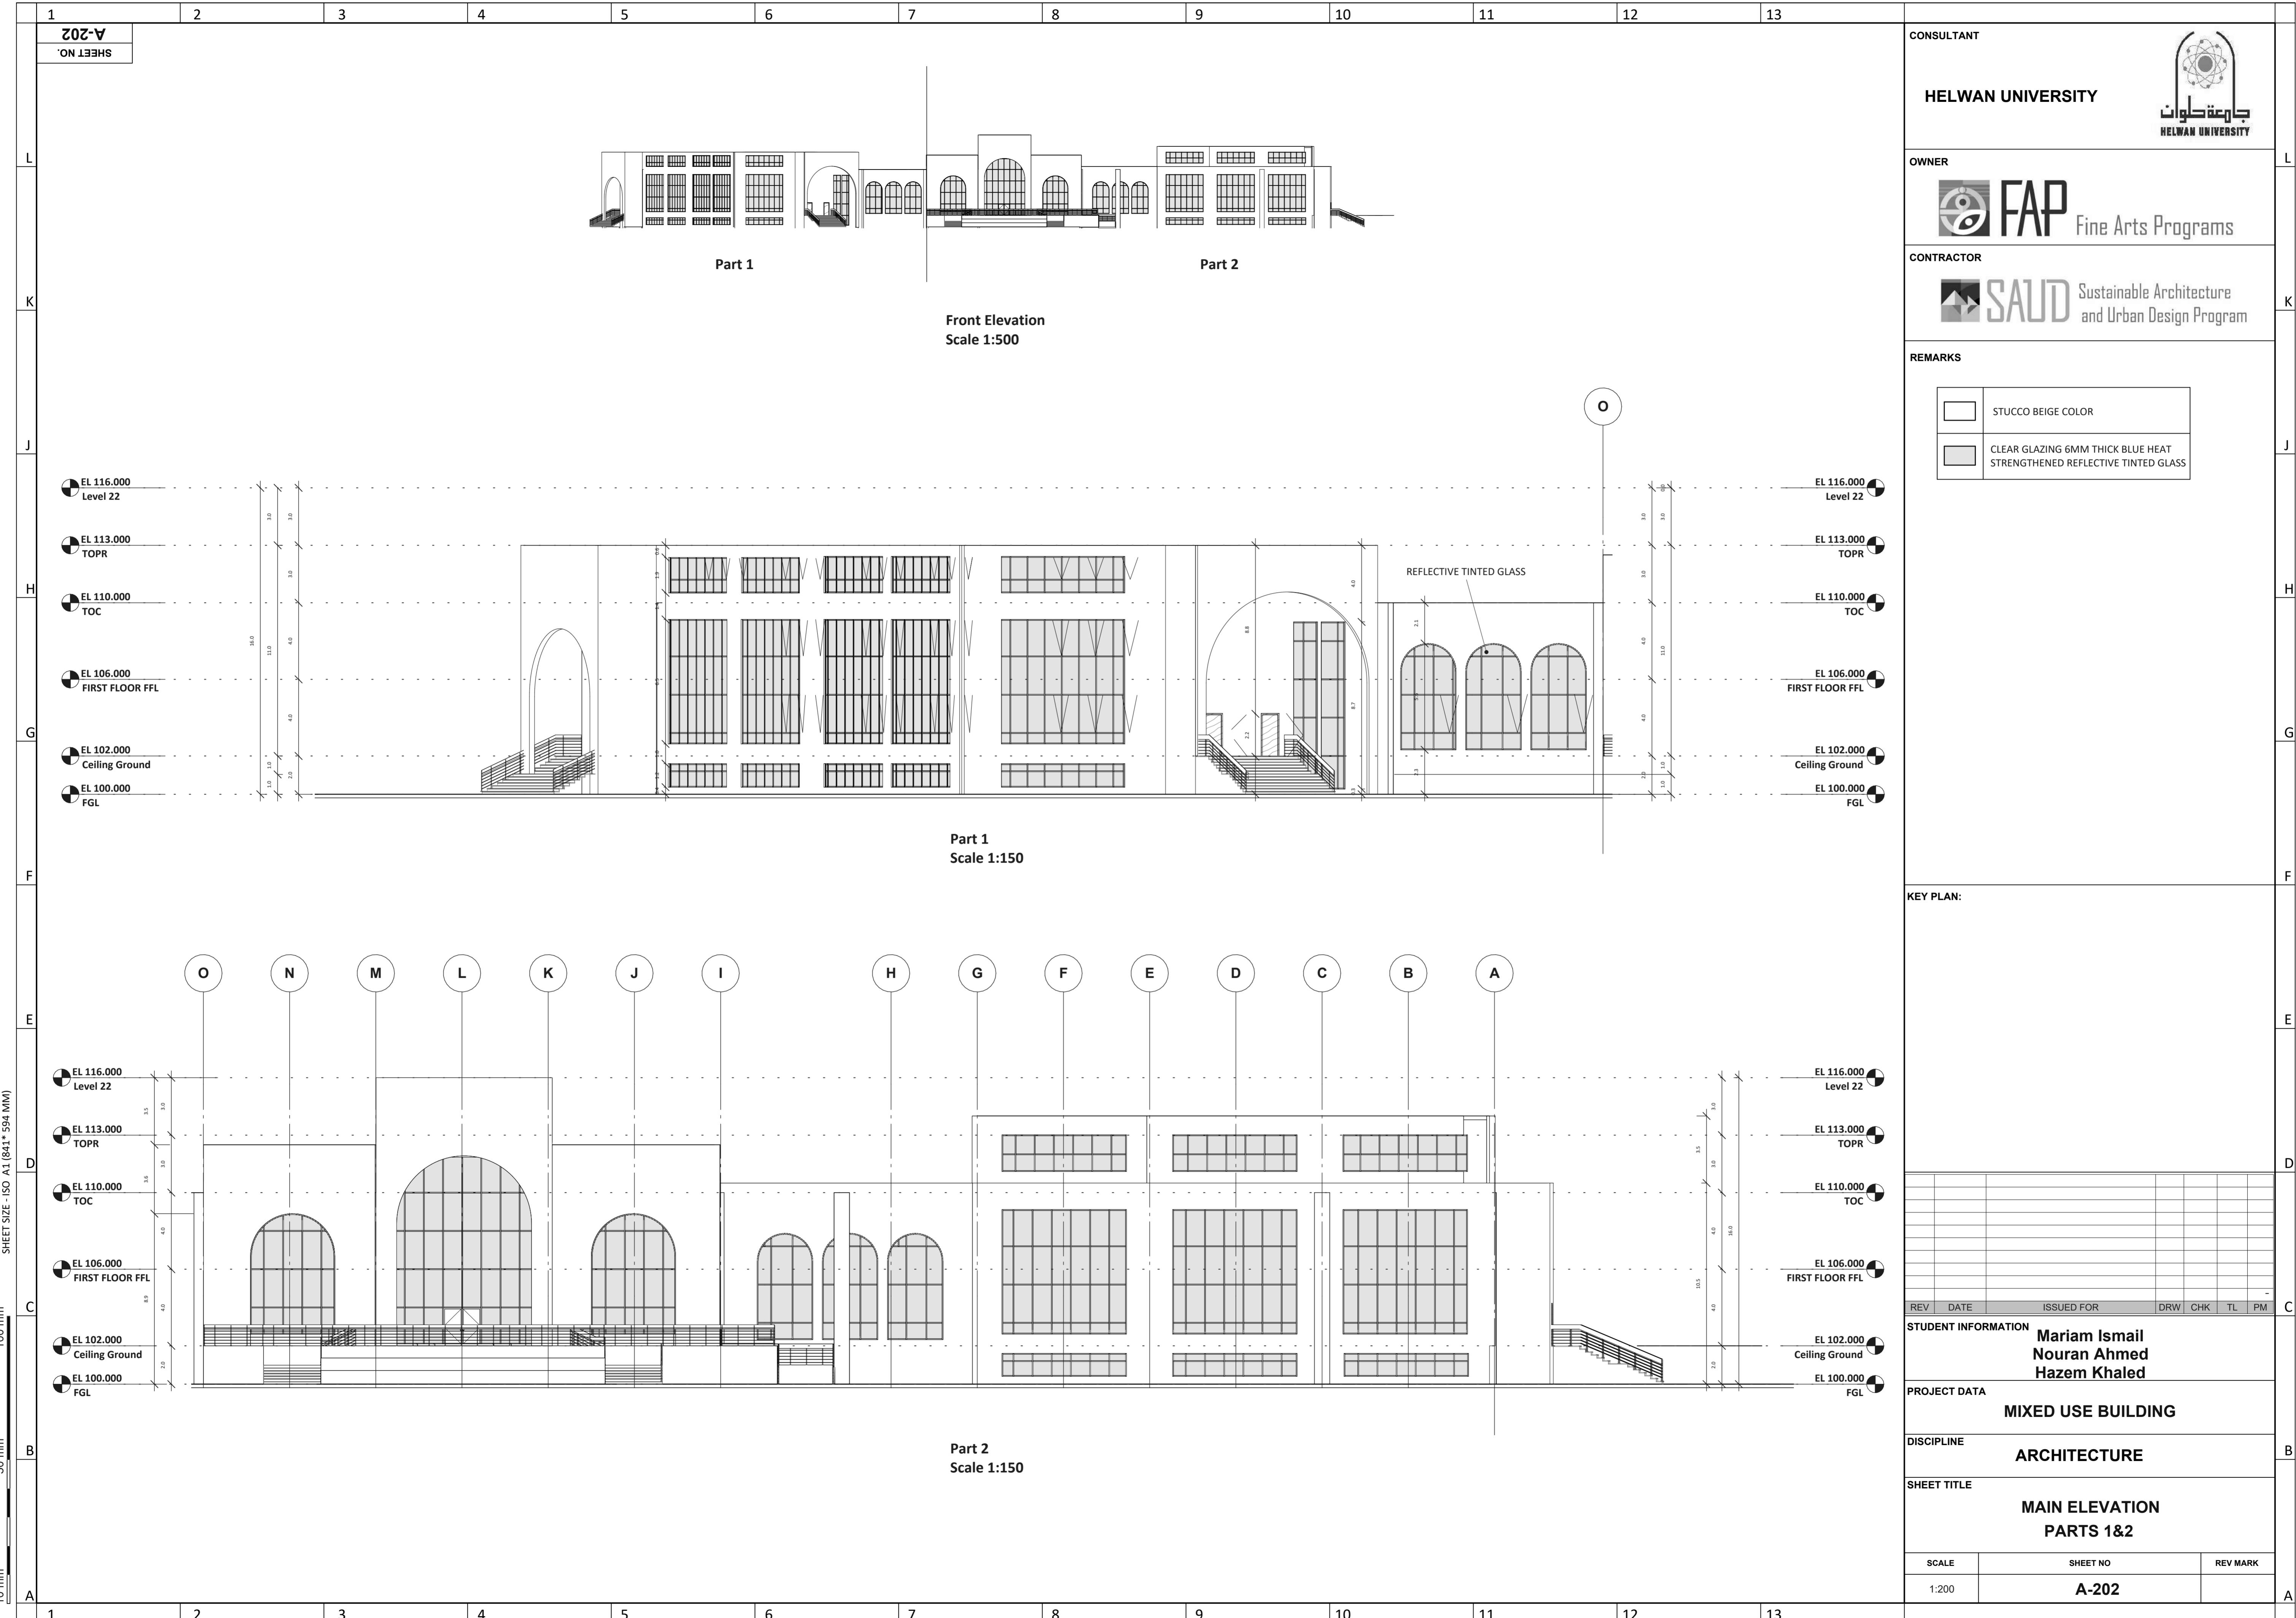

1 **2** **3** **4** **5** **6** **7** **8** **9** **10** **11** **12** **13**

A-203
SHEET NO.

CONSULTANT
HELWAN UNIVERSITY



OWNER

FAP Fine Arts Programs

CONTRACTOR

SAUD Sustainable Architecture and Urban Design Program

REMARKS

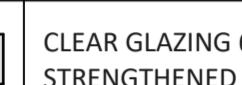	STUCCO BEIGE COLOR
	CLEAR GLAZING 6MM THICK BLUE HEAT STRENGTHENED REFLECTIVE TINTED GLASS

KEY PLAN:

REV	DATE	ISSUED FOR	DRW	CHK	TL	PM
STUDENT INFORMATION						
Mariam Ismail Nouran Ahmed Hazem Khaled						
PROJECT DATA						
MIXED USE BUILDING						
DISCIPLINE						
ARCHITECTURE						
SHEET TITLE						
BACK ELEVATION PAERTS 1&2						
SCALE	SHEET NO	REV MARK				
1:200	A-203					


Part 1
Part 2
Back Elevation
Scale 1:500


Part 1
Scale 1:150


Part 2
Scale 1:150

100 mm
50 mm
Scanning scale



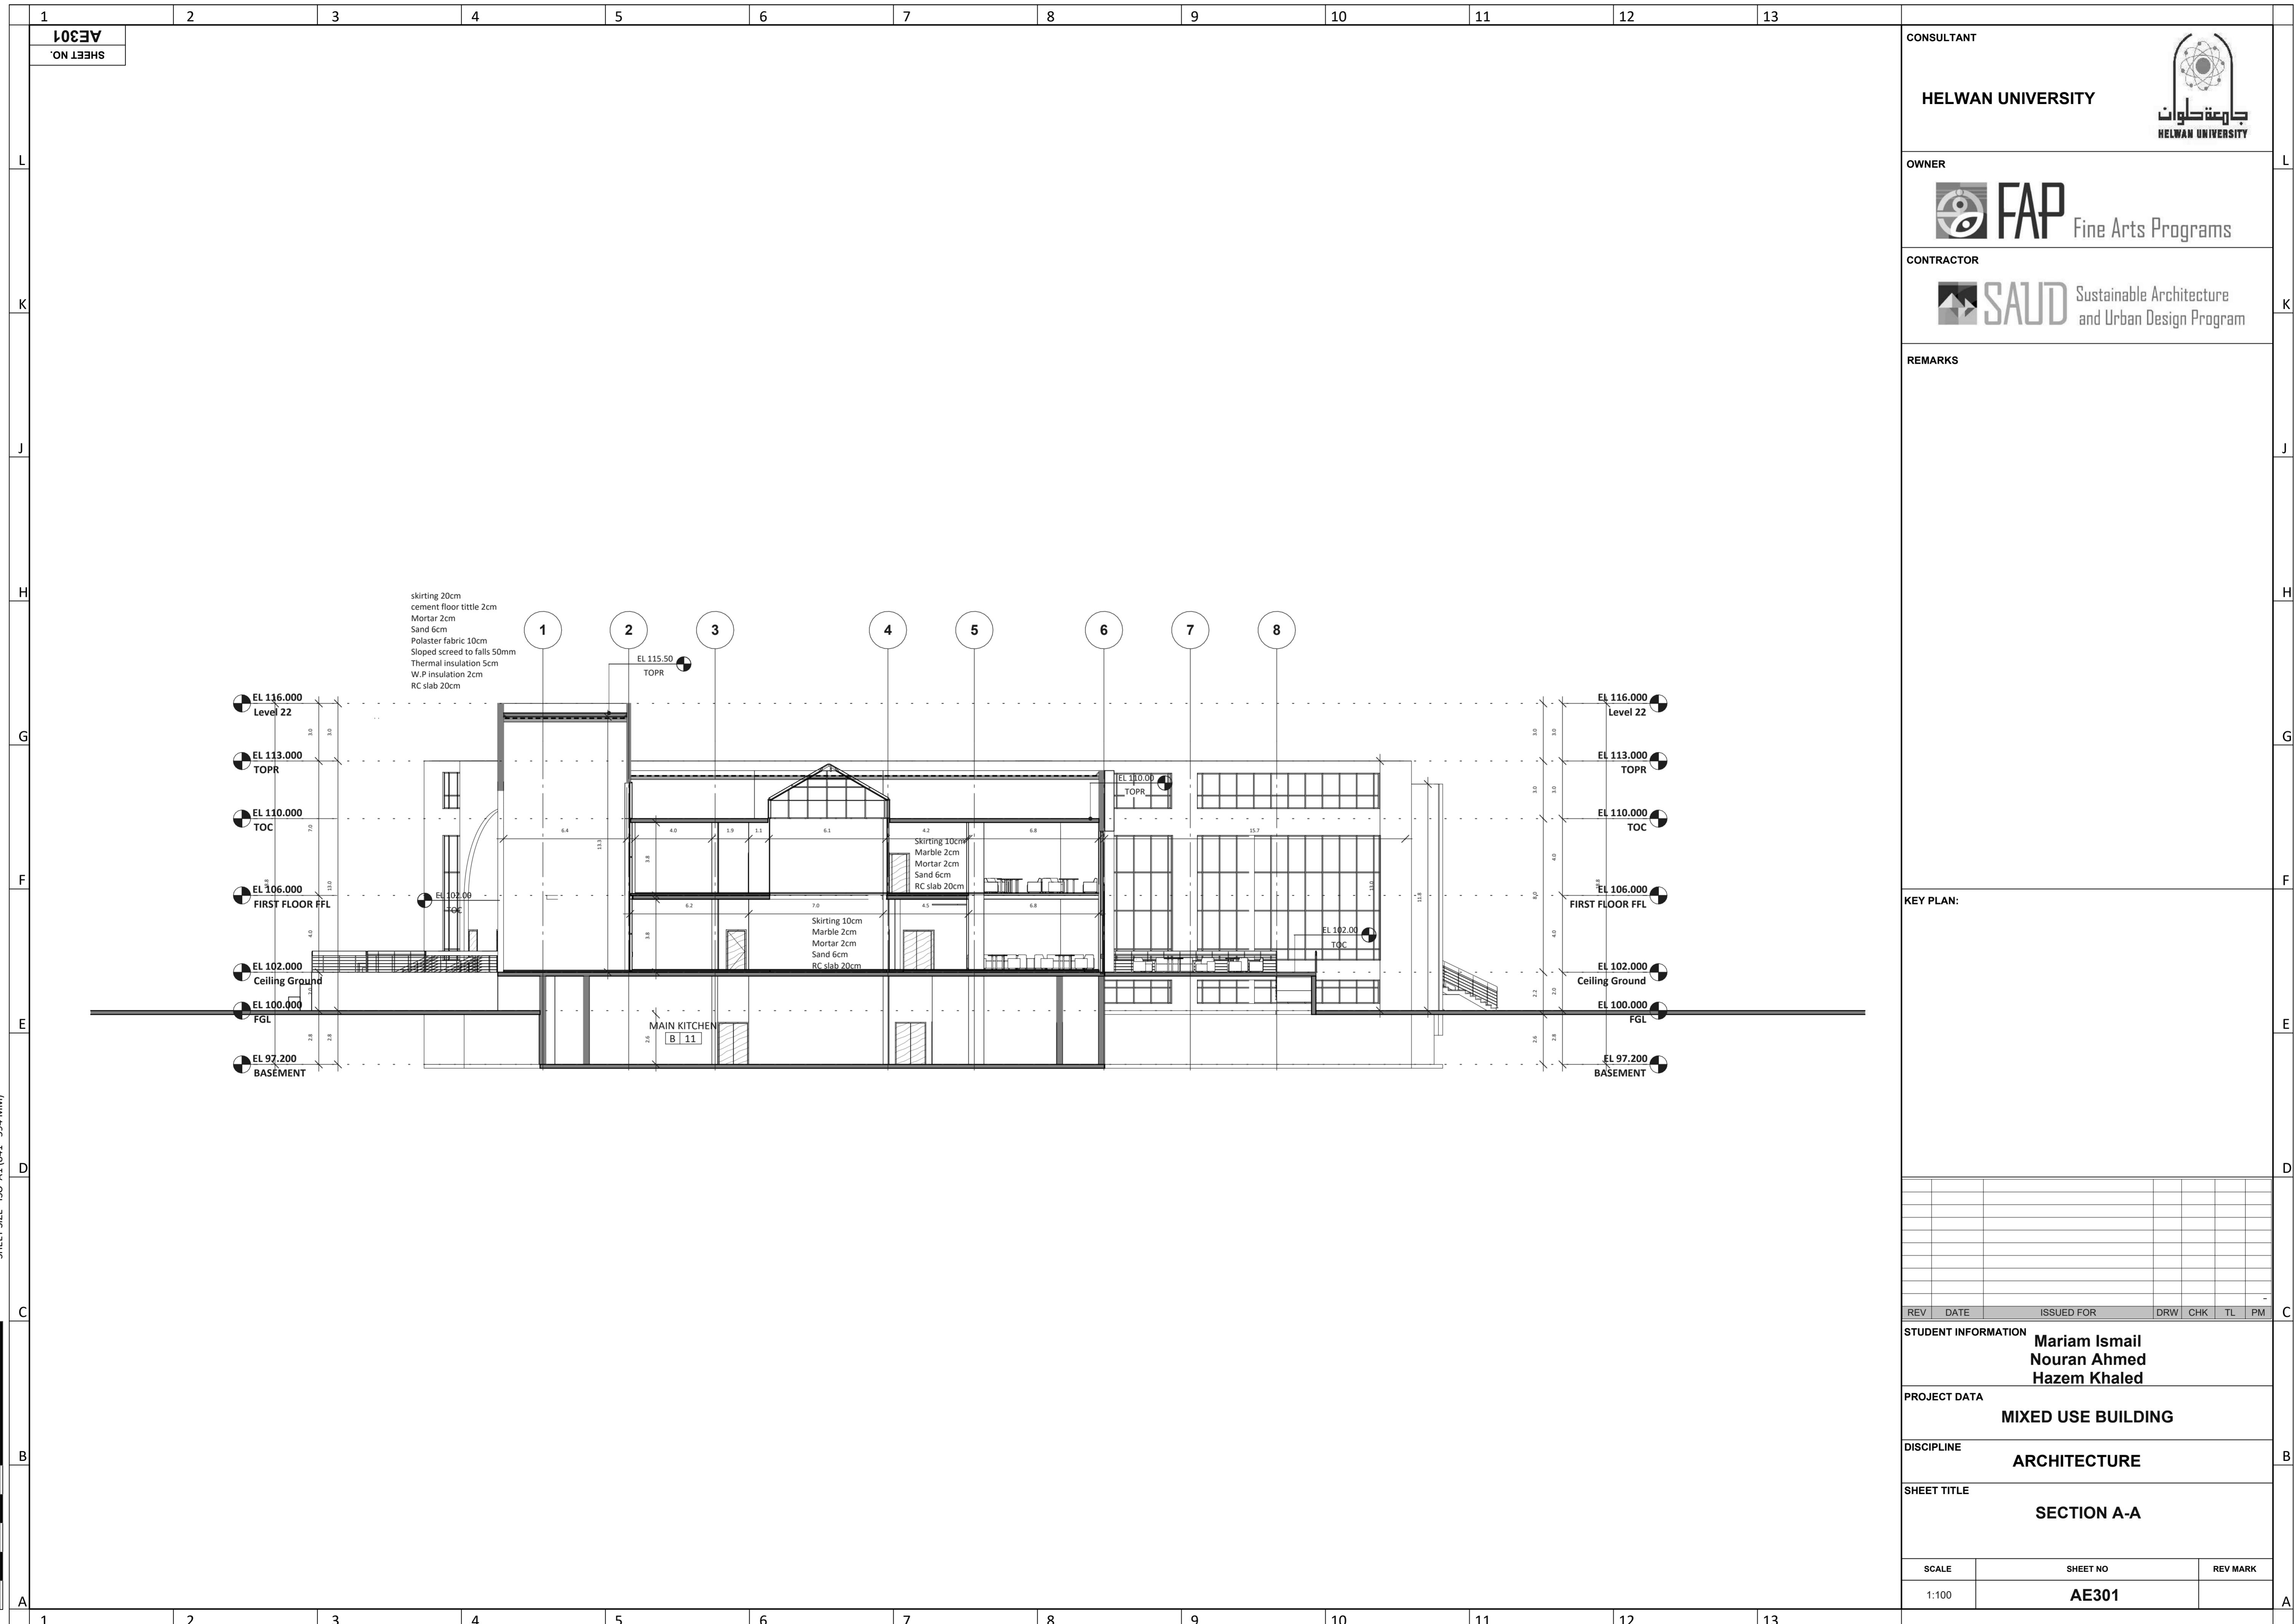

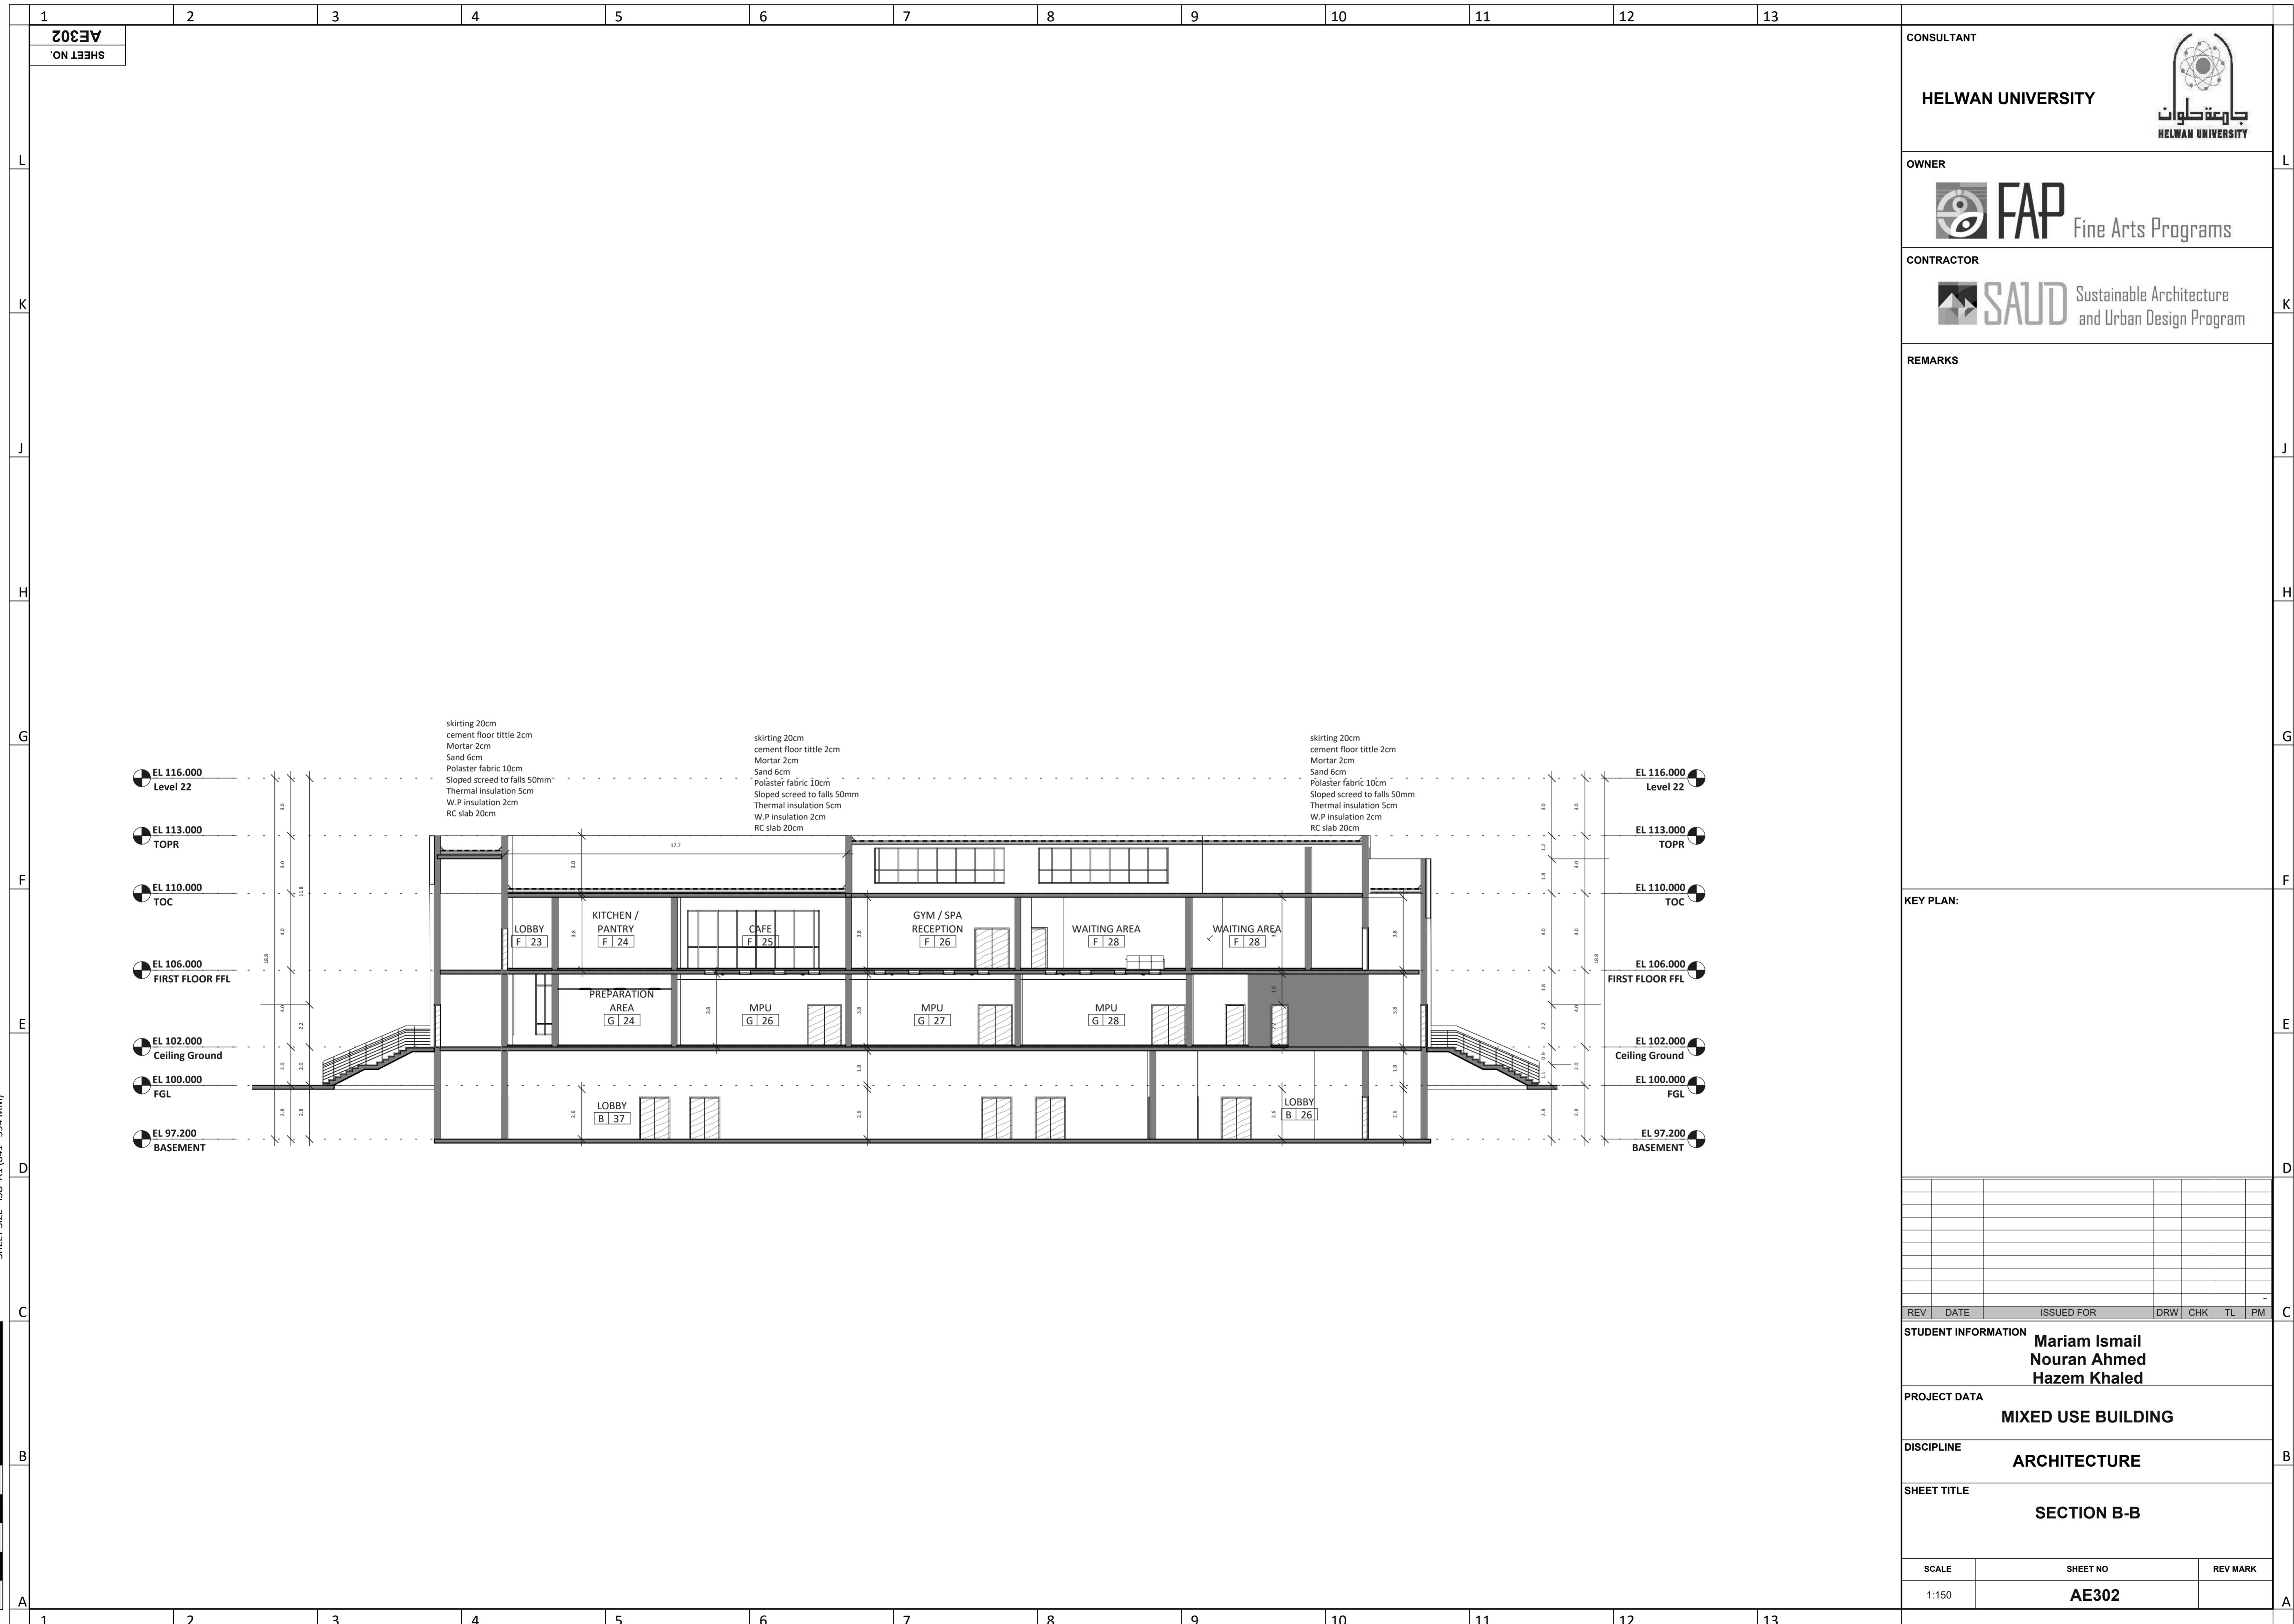

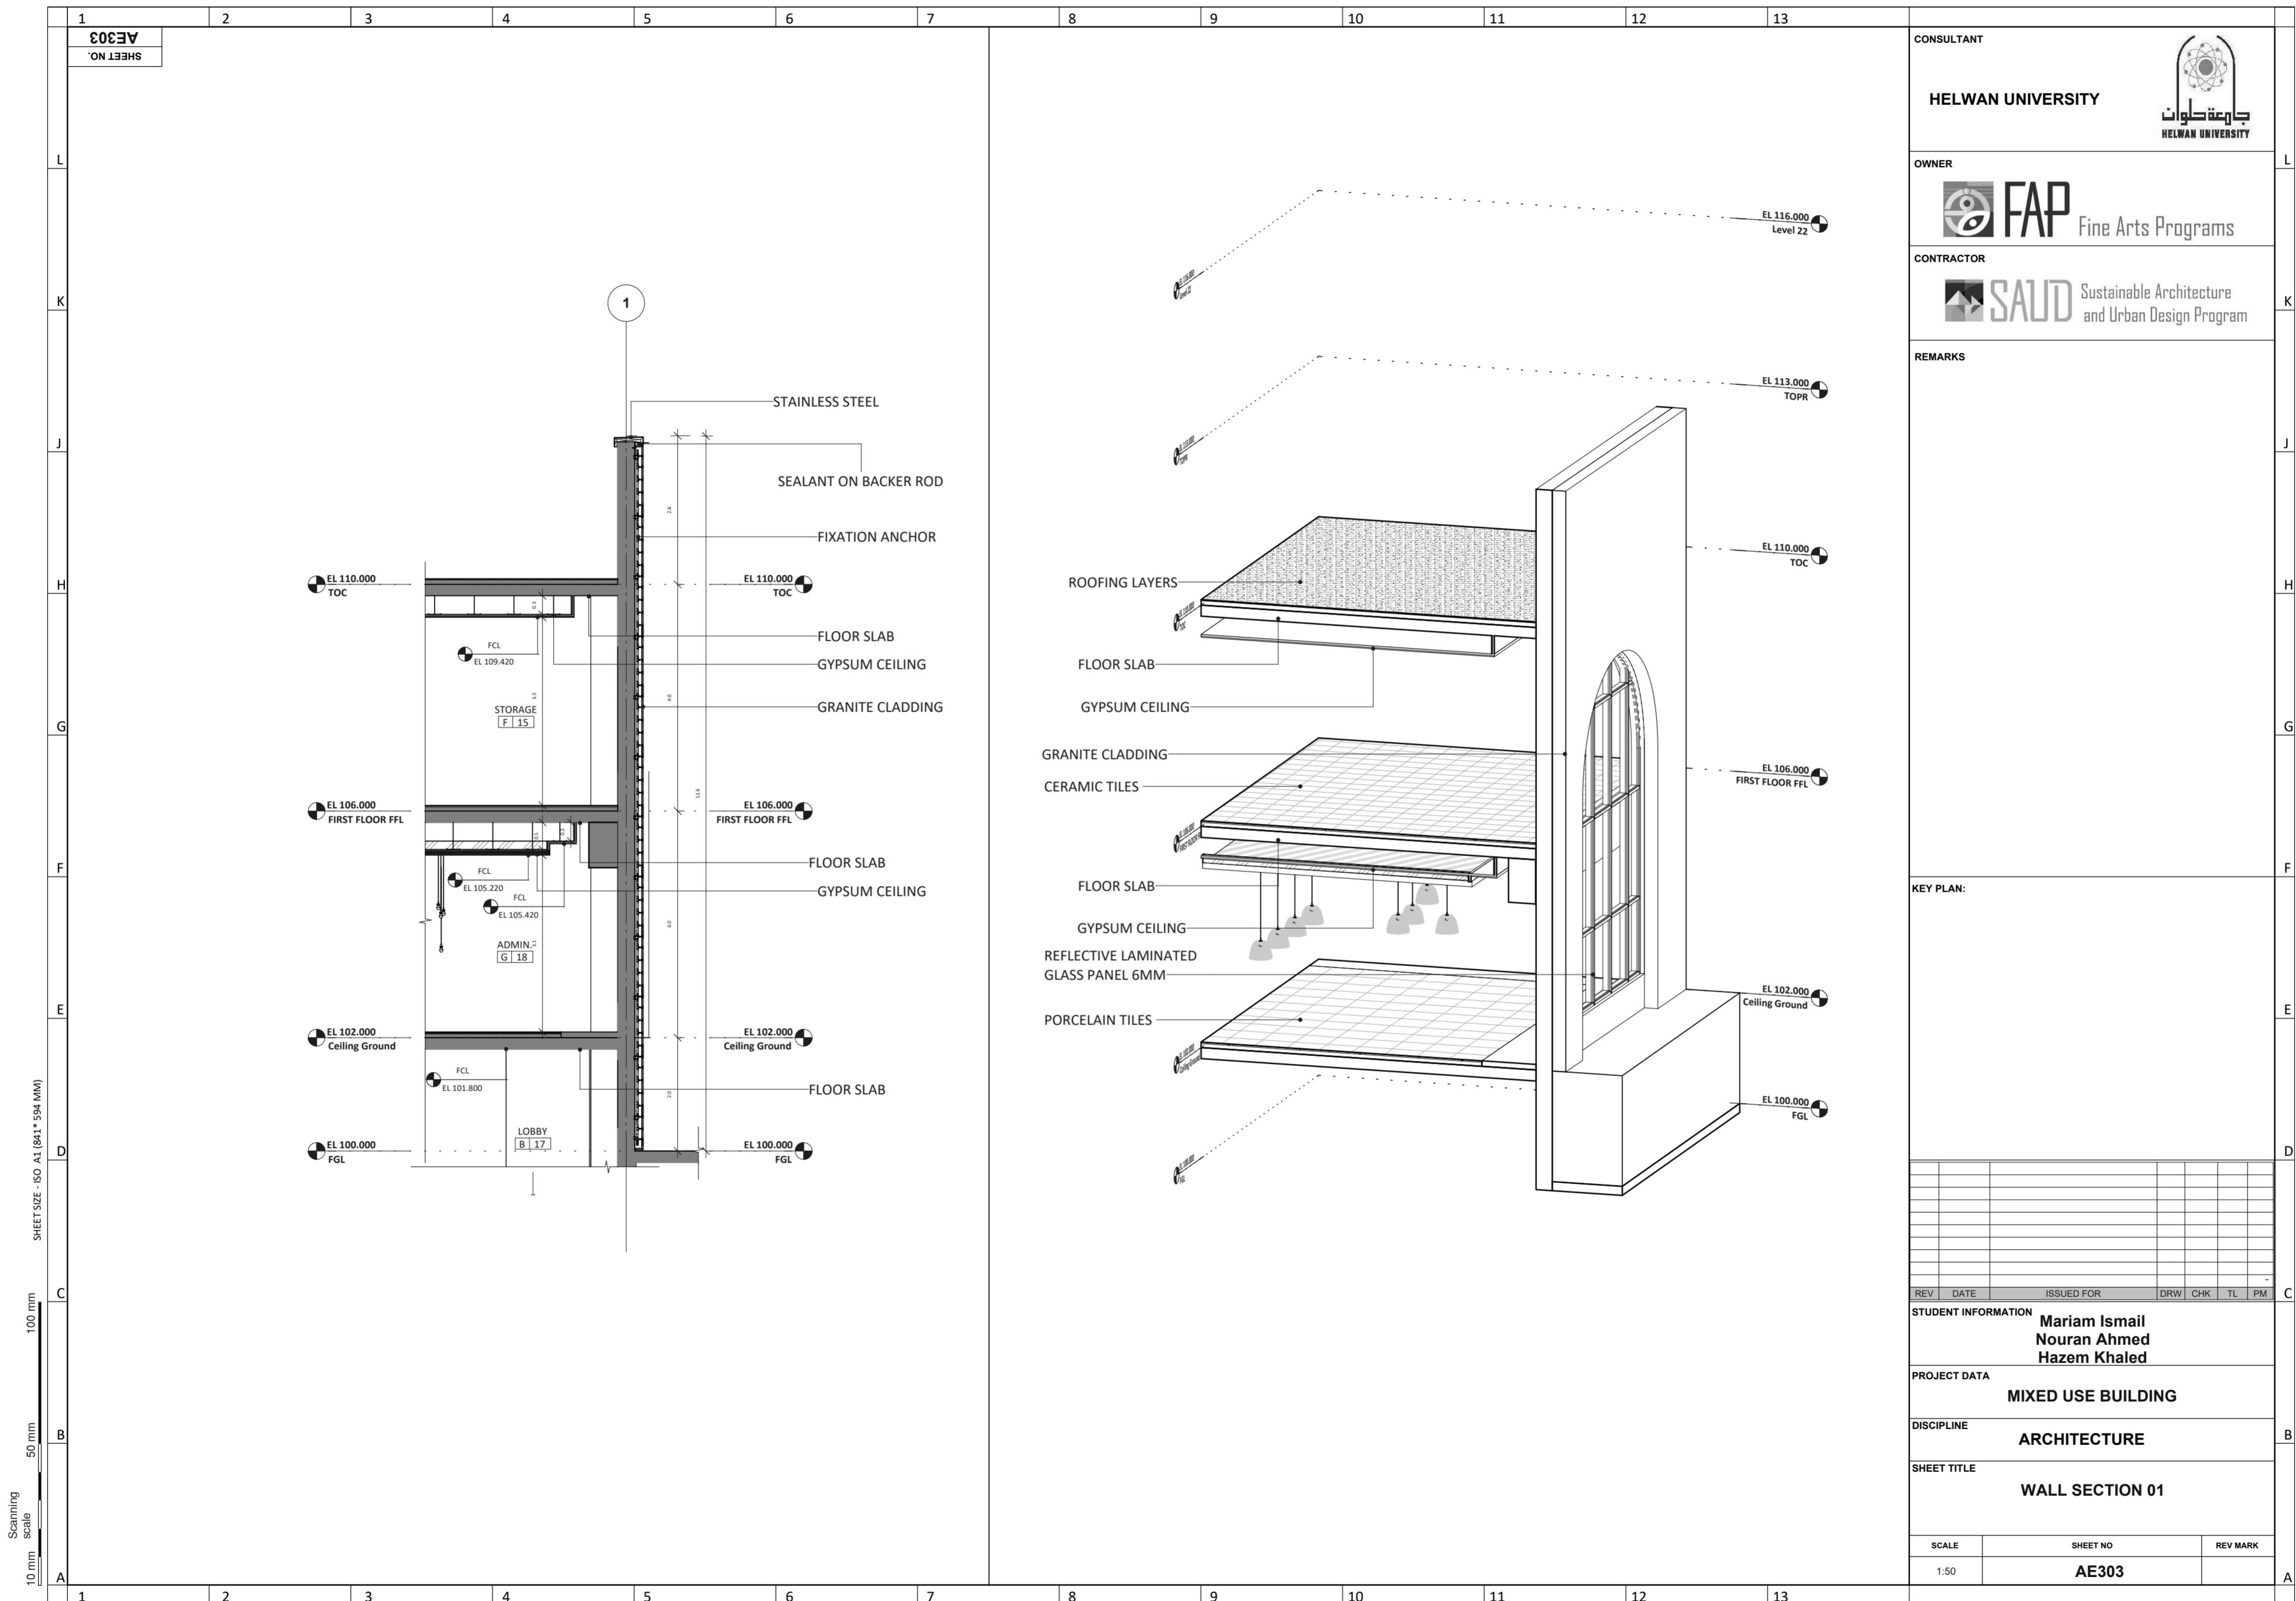

Section

1 **2** **3** **4** **5** **6** **7** **8** **9** **10** **11** **12** **13**

CONSULTANT
HELWAN UNIVERSITY

OWNER
FAP Fine Arts Programs

CONTRACTOR
SAUD Sustainable Architecture and Urban Design Program

REMARKS

KEY PLAN:

STUDENT INFORMATION Mariam Ismail
Nouran Ahmed
Hazem Khaled

PROJECT DATA MIXED USE BUILDING

DISCIPLINE ARCHITECTURE

SHEET TITLE MPU WALL SECTION

SCALE 1:100 **SHEET NO** MPU Wall Section **REV MARK**

Sheet No MPU Wall Section

EL 113.000 **TOPR**
EL 110.000 **TOC**
EL 106.000 **FIRST FLOOR FFL**
EL 102.000 **Ground FPL**
EL 100.000 **FGL**


CLINIC 1 **F 30**
MPU **G 28**
MEP & SERVICES **B 23**


EL 101.000


STAINLESS STEEL
FIXATION ANCHOR
GRANITE CLADDING
ALUMINUM MULLION
FLOOR SLAB
GYPSUM CEILING
SPANDREL GLASS PANEL
FLOOR SLAB
GYPSUM CEILING
REFLECTIVE LAMINATED GLASS PANEL 6MM
FLOOR SLAB
REFLECTIVE LAMINATED GLASS PANEL 6MM
FLOOR SLAB
FCL **EL 109.400**
FCL **EL 105.510**
FCL **EL 105.510**
AE403
AE502
T


NATURAL STONE CLADDING
ROOFING LAYERS
GYPSUM CEILING
REFLECTIVE LAMINATED GLASS PANEL 6MM
PORCELAIN TILES
SPANDREL GLASS PANEL
FLOOR SLAB
CONCRETE BEAM
REFLECTIVE LAMINATED GLASS PANEL 6MM
PORCELAIN TILES 600*600MM
FLOOR SLAB
REFLECTIVE LAMINATED GLASS PANEL 6MM


REV DATE ISSUED FOR DRW CHK TL PM

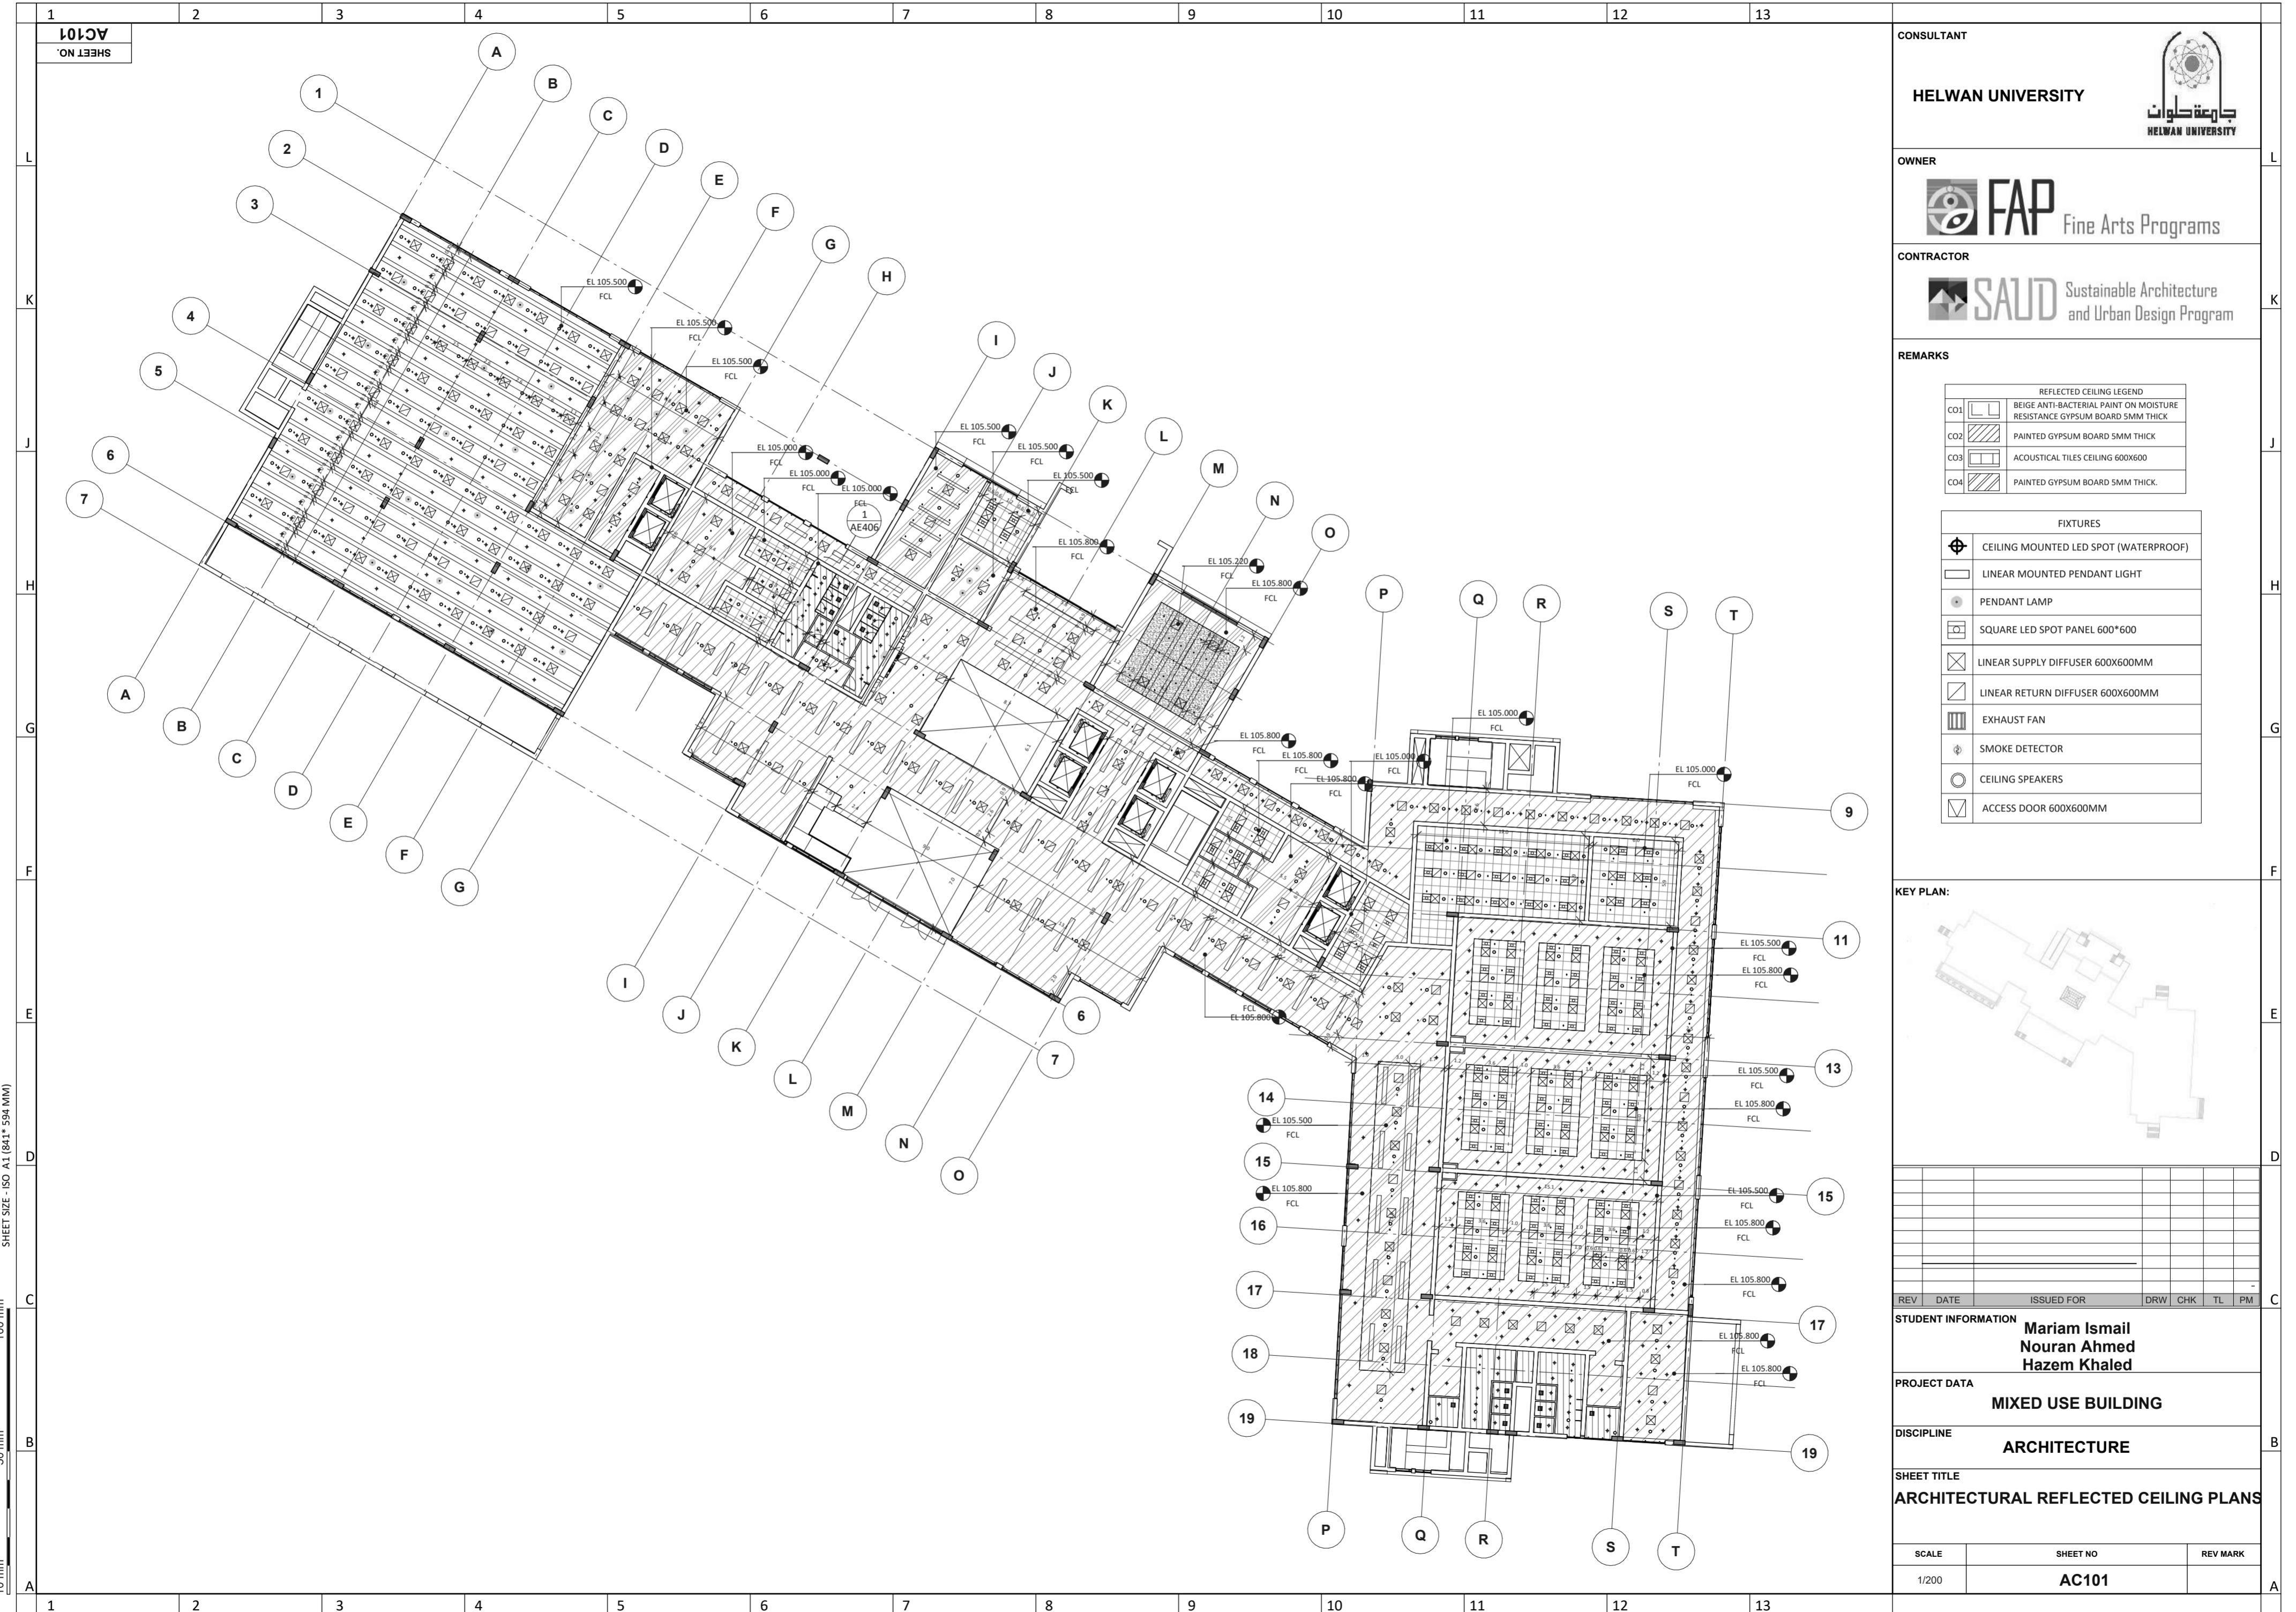


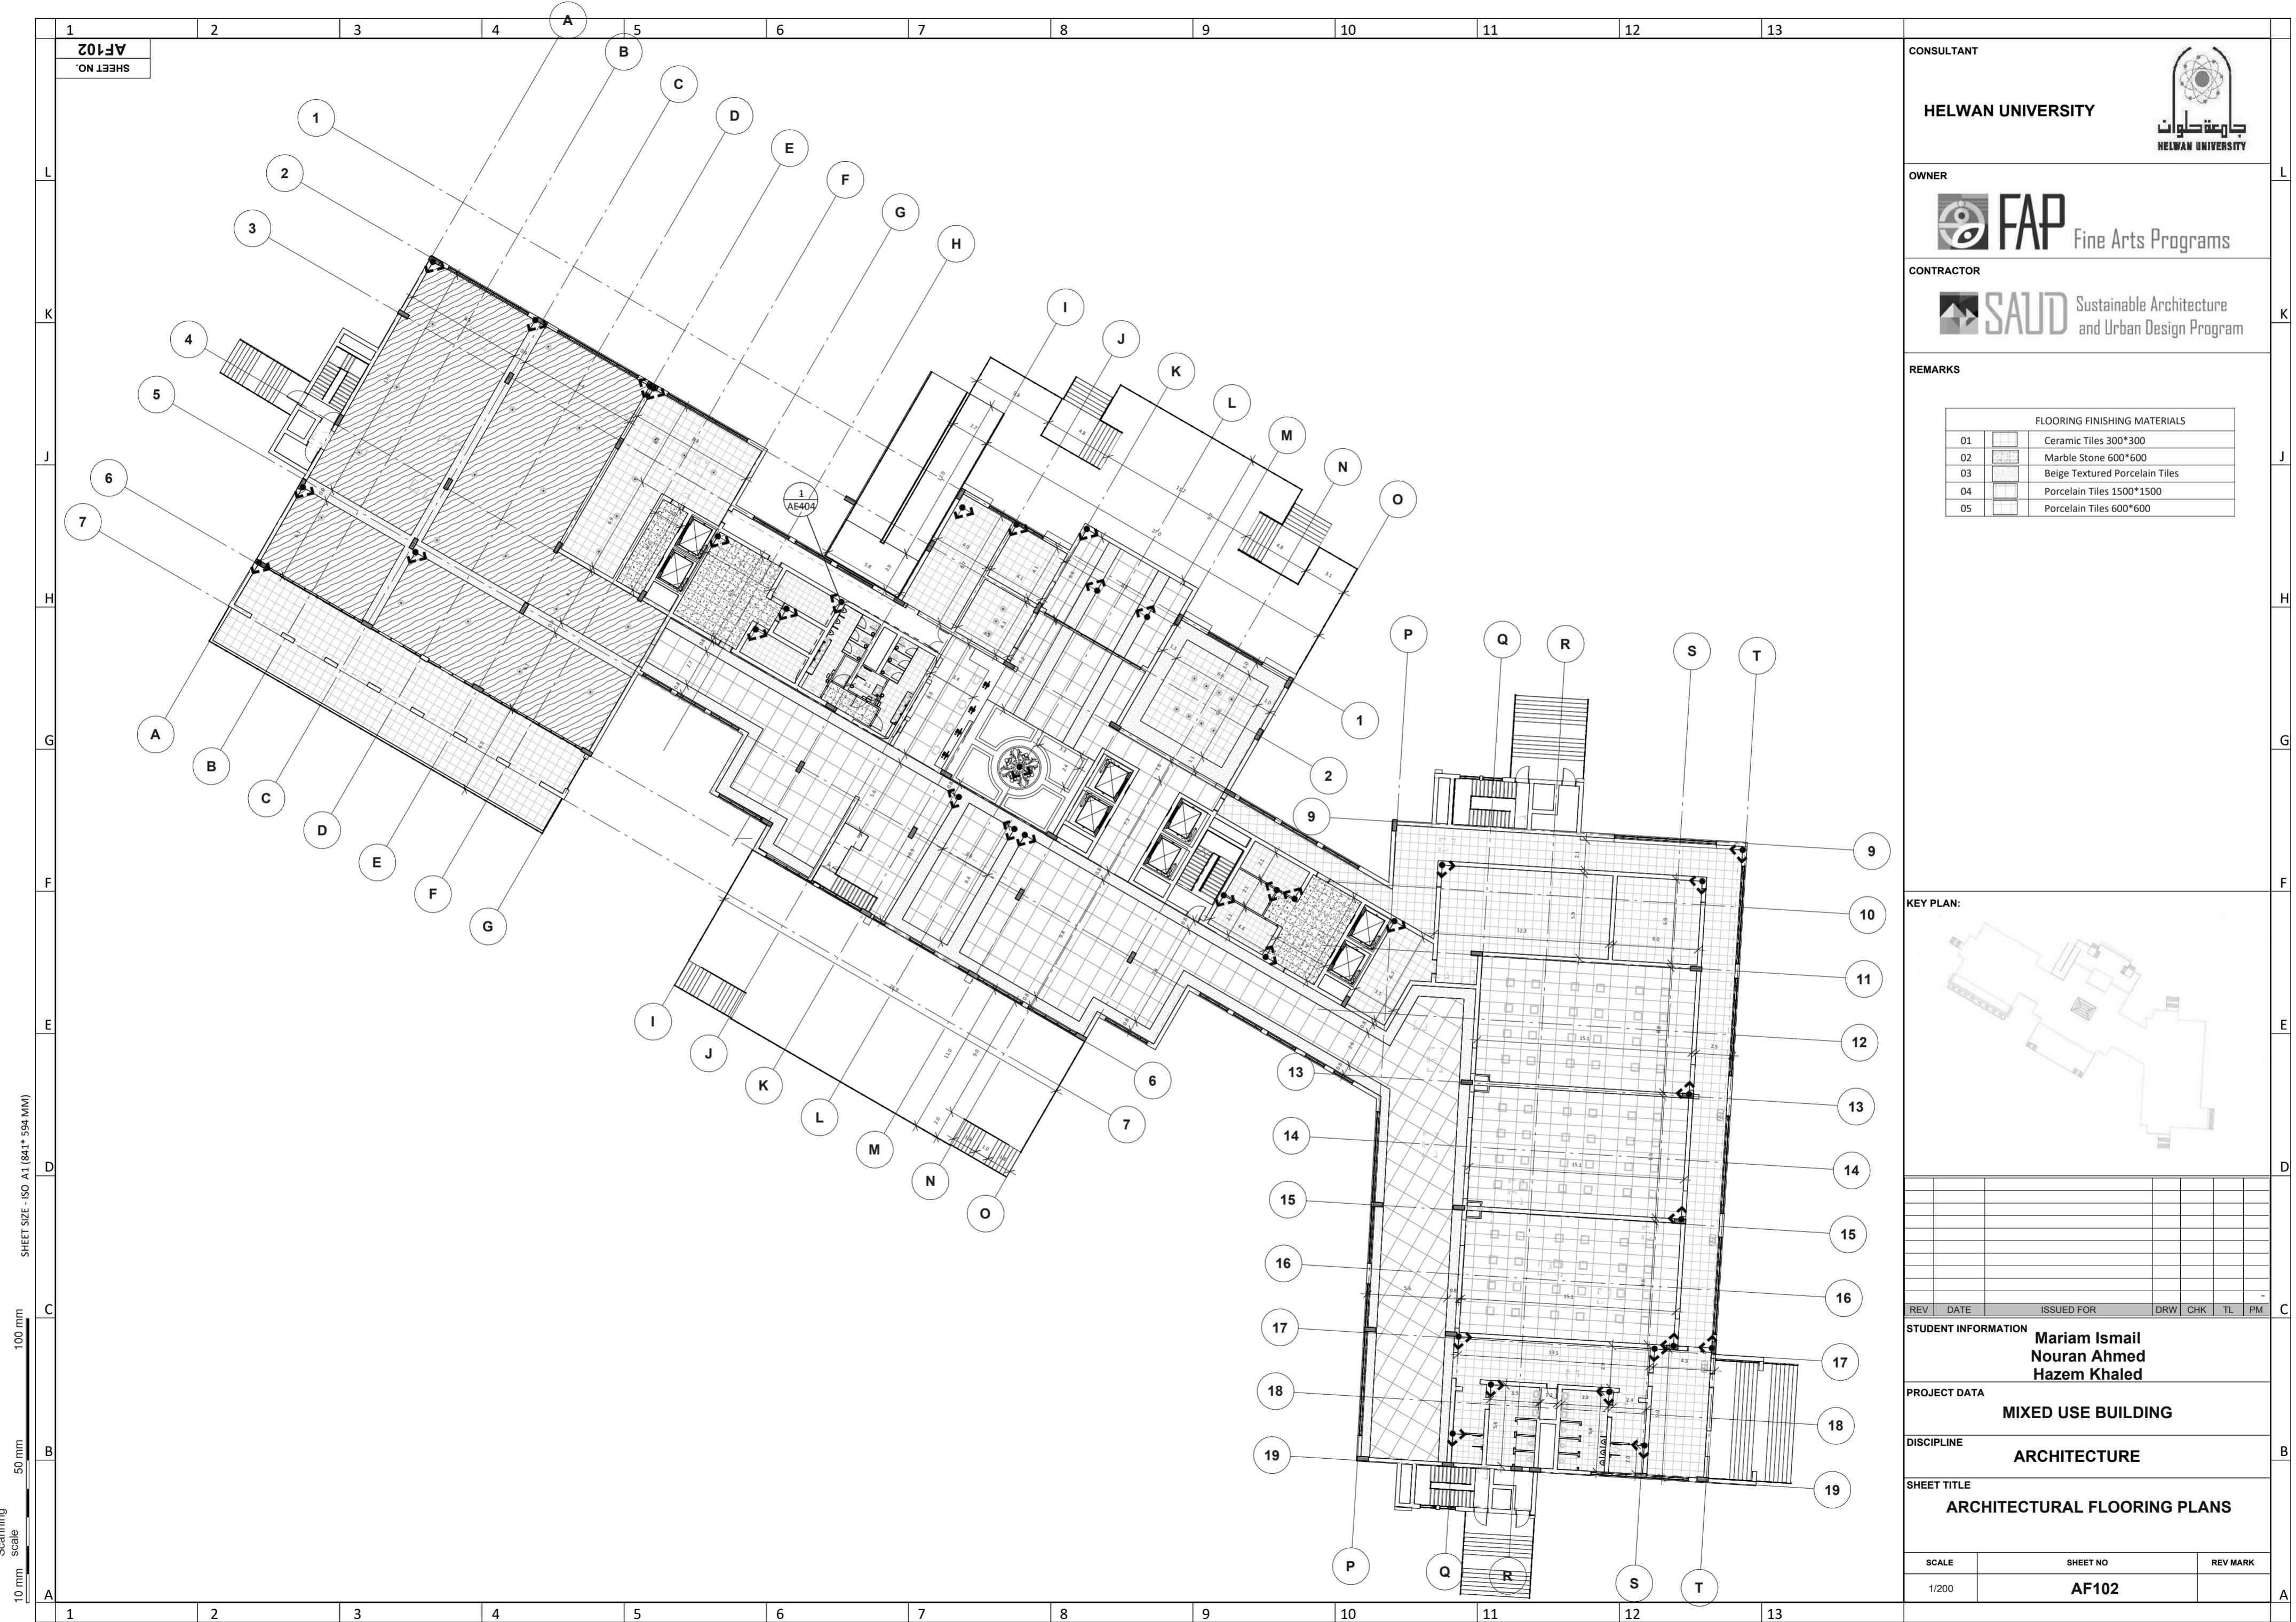

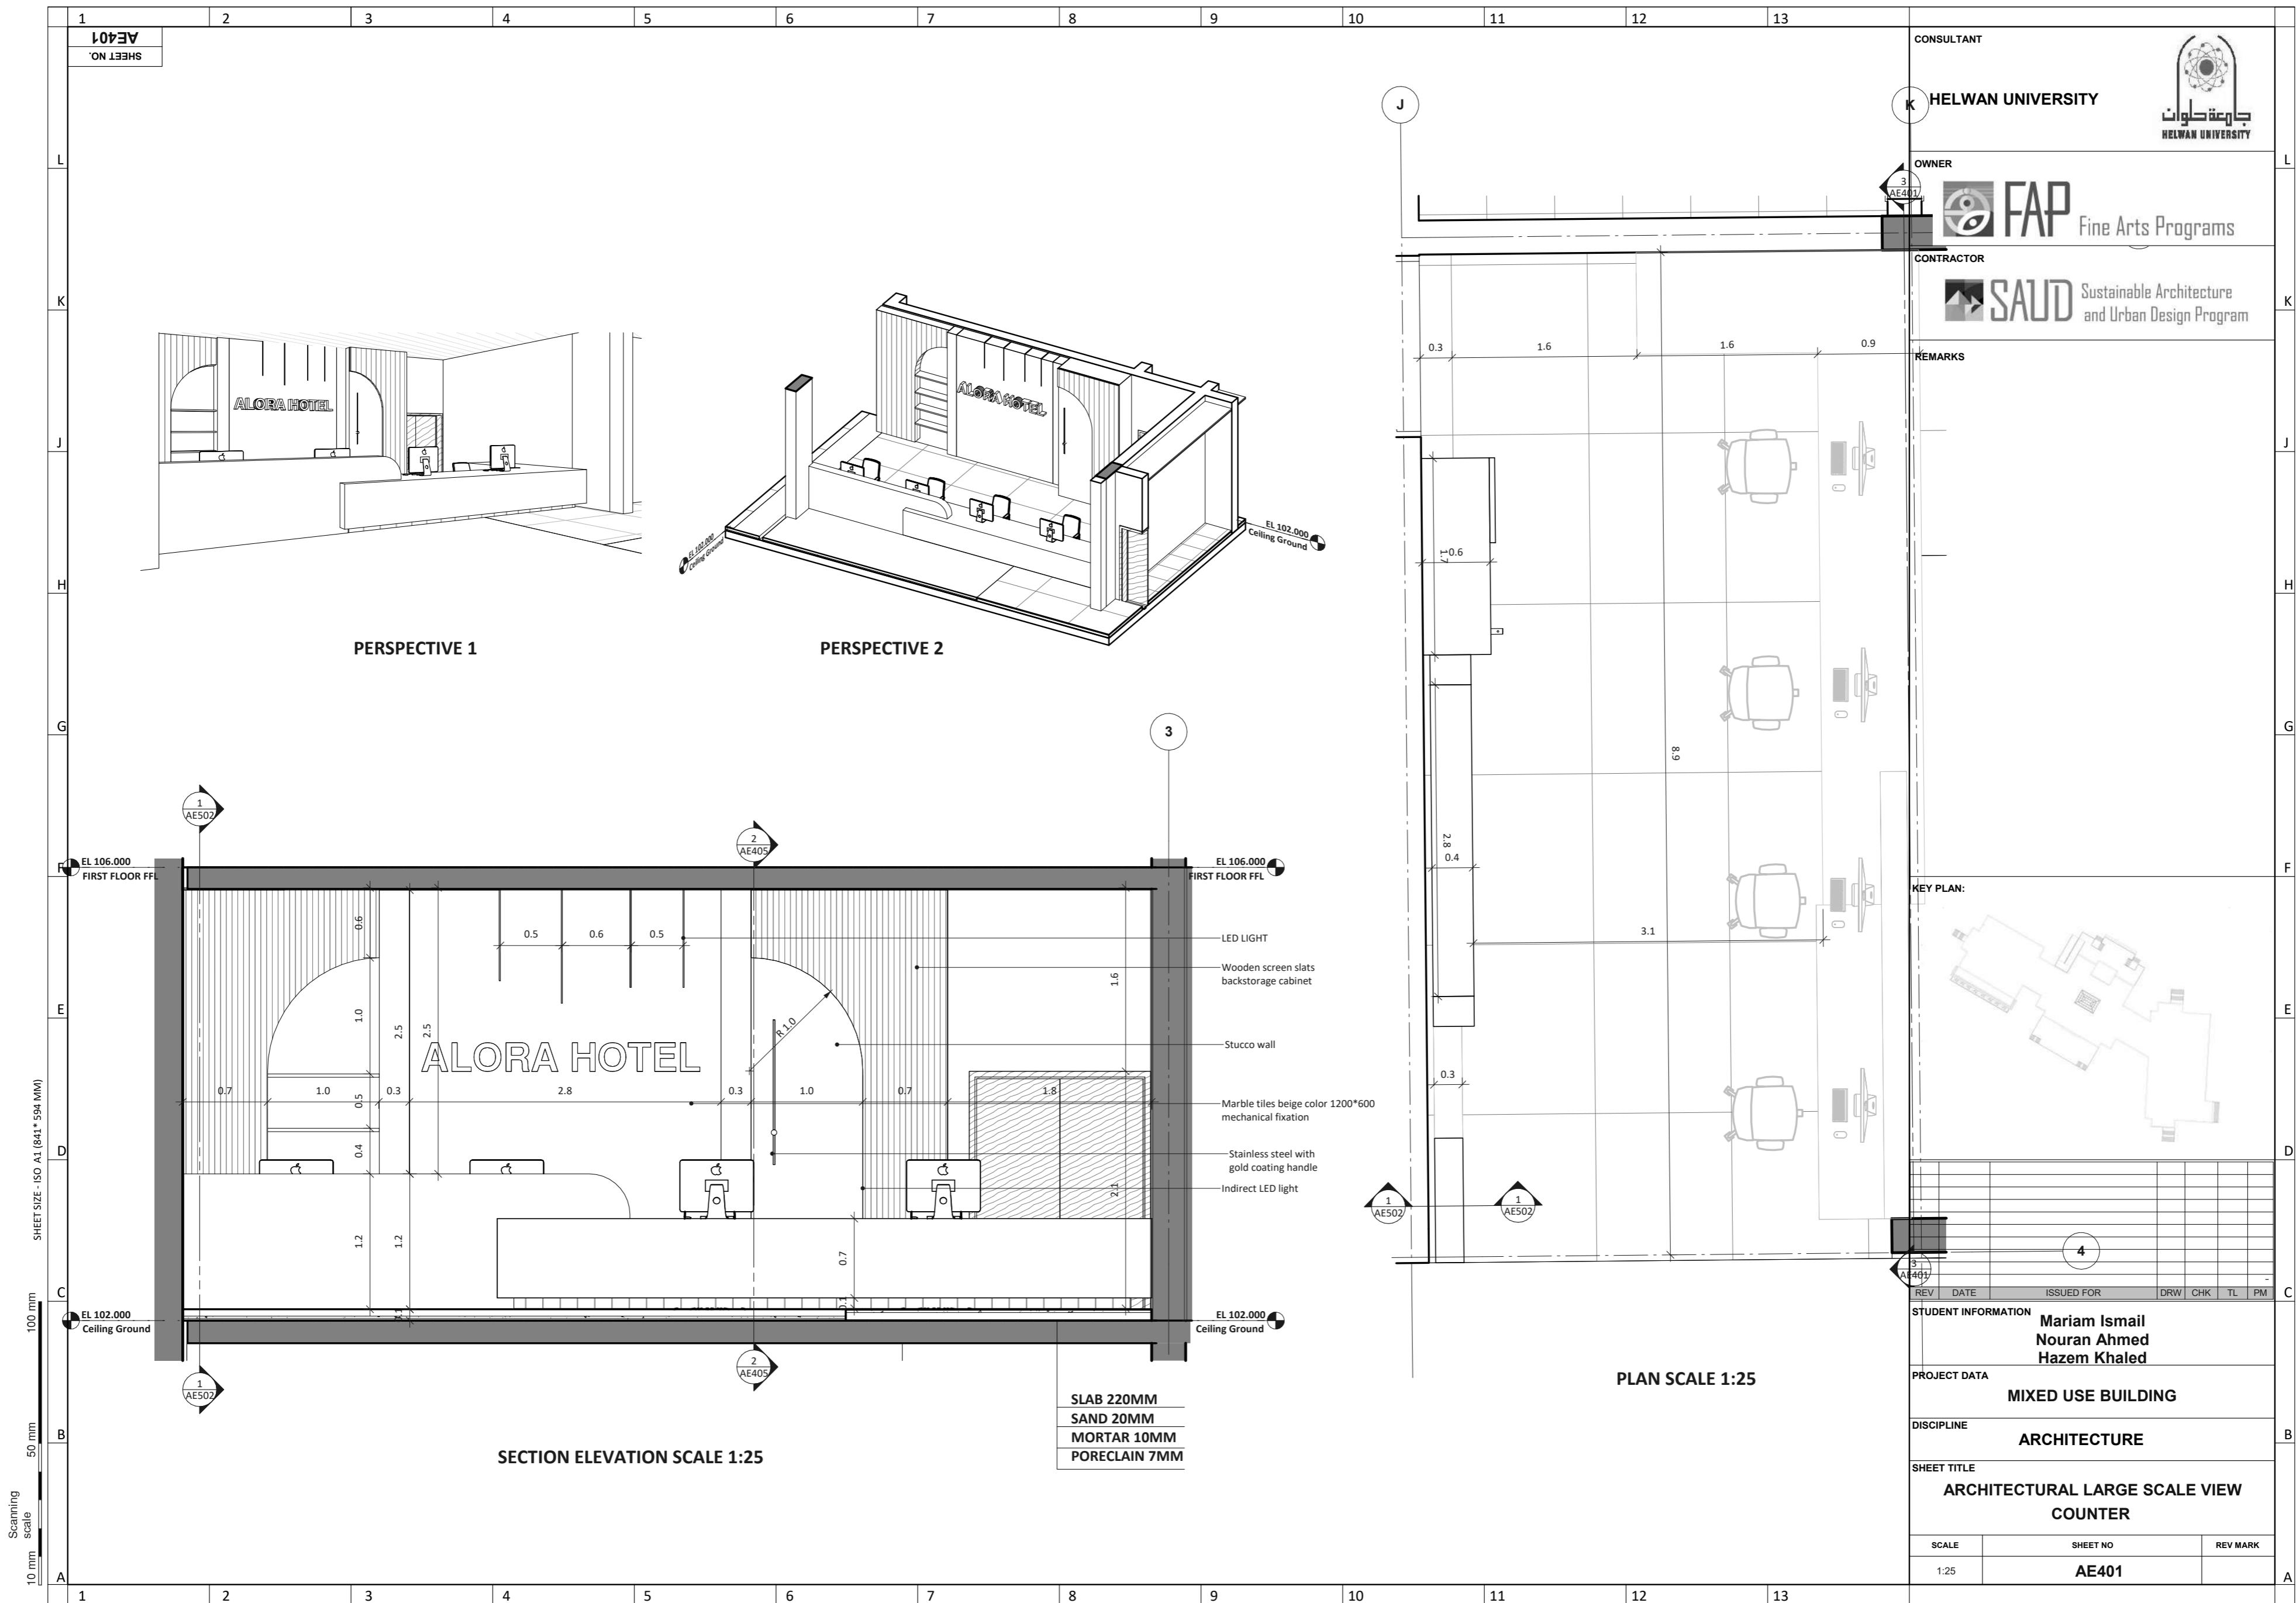

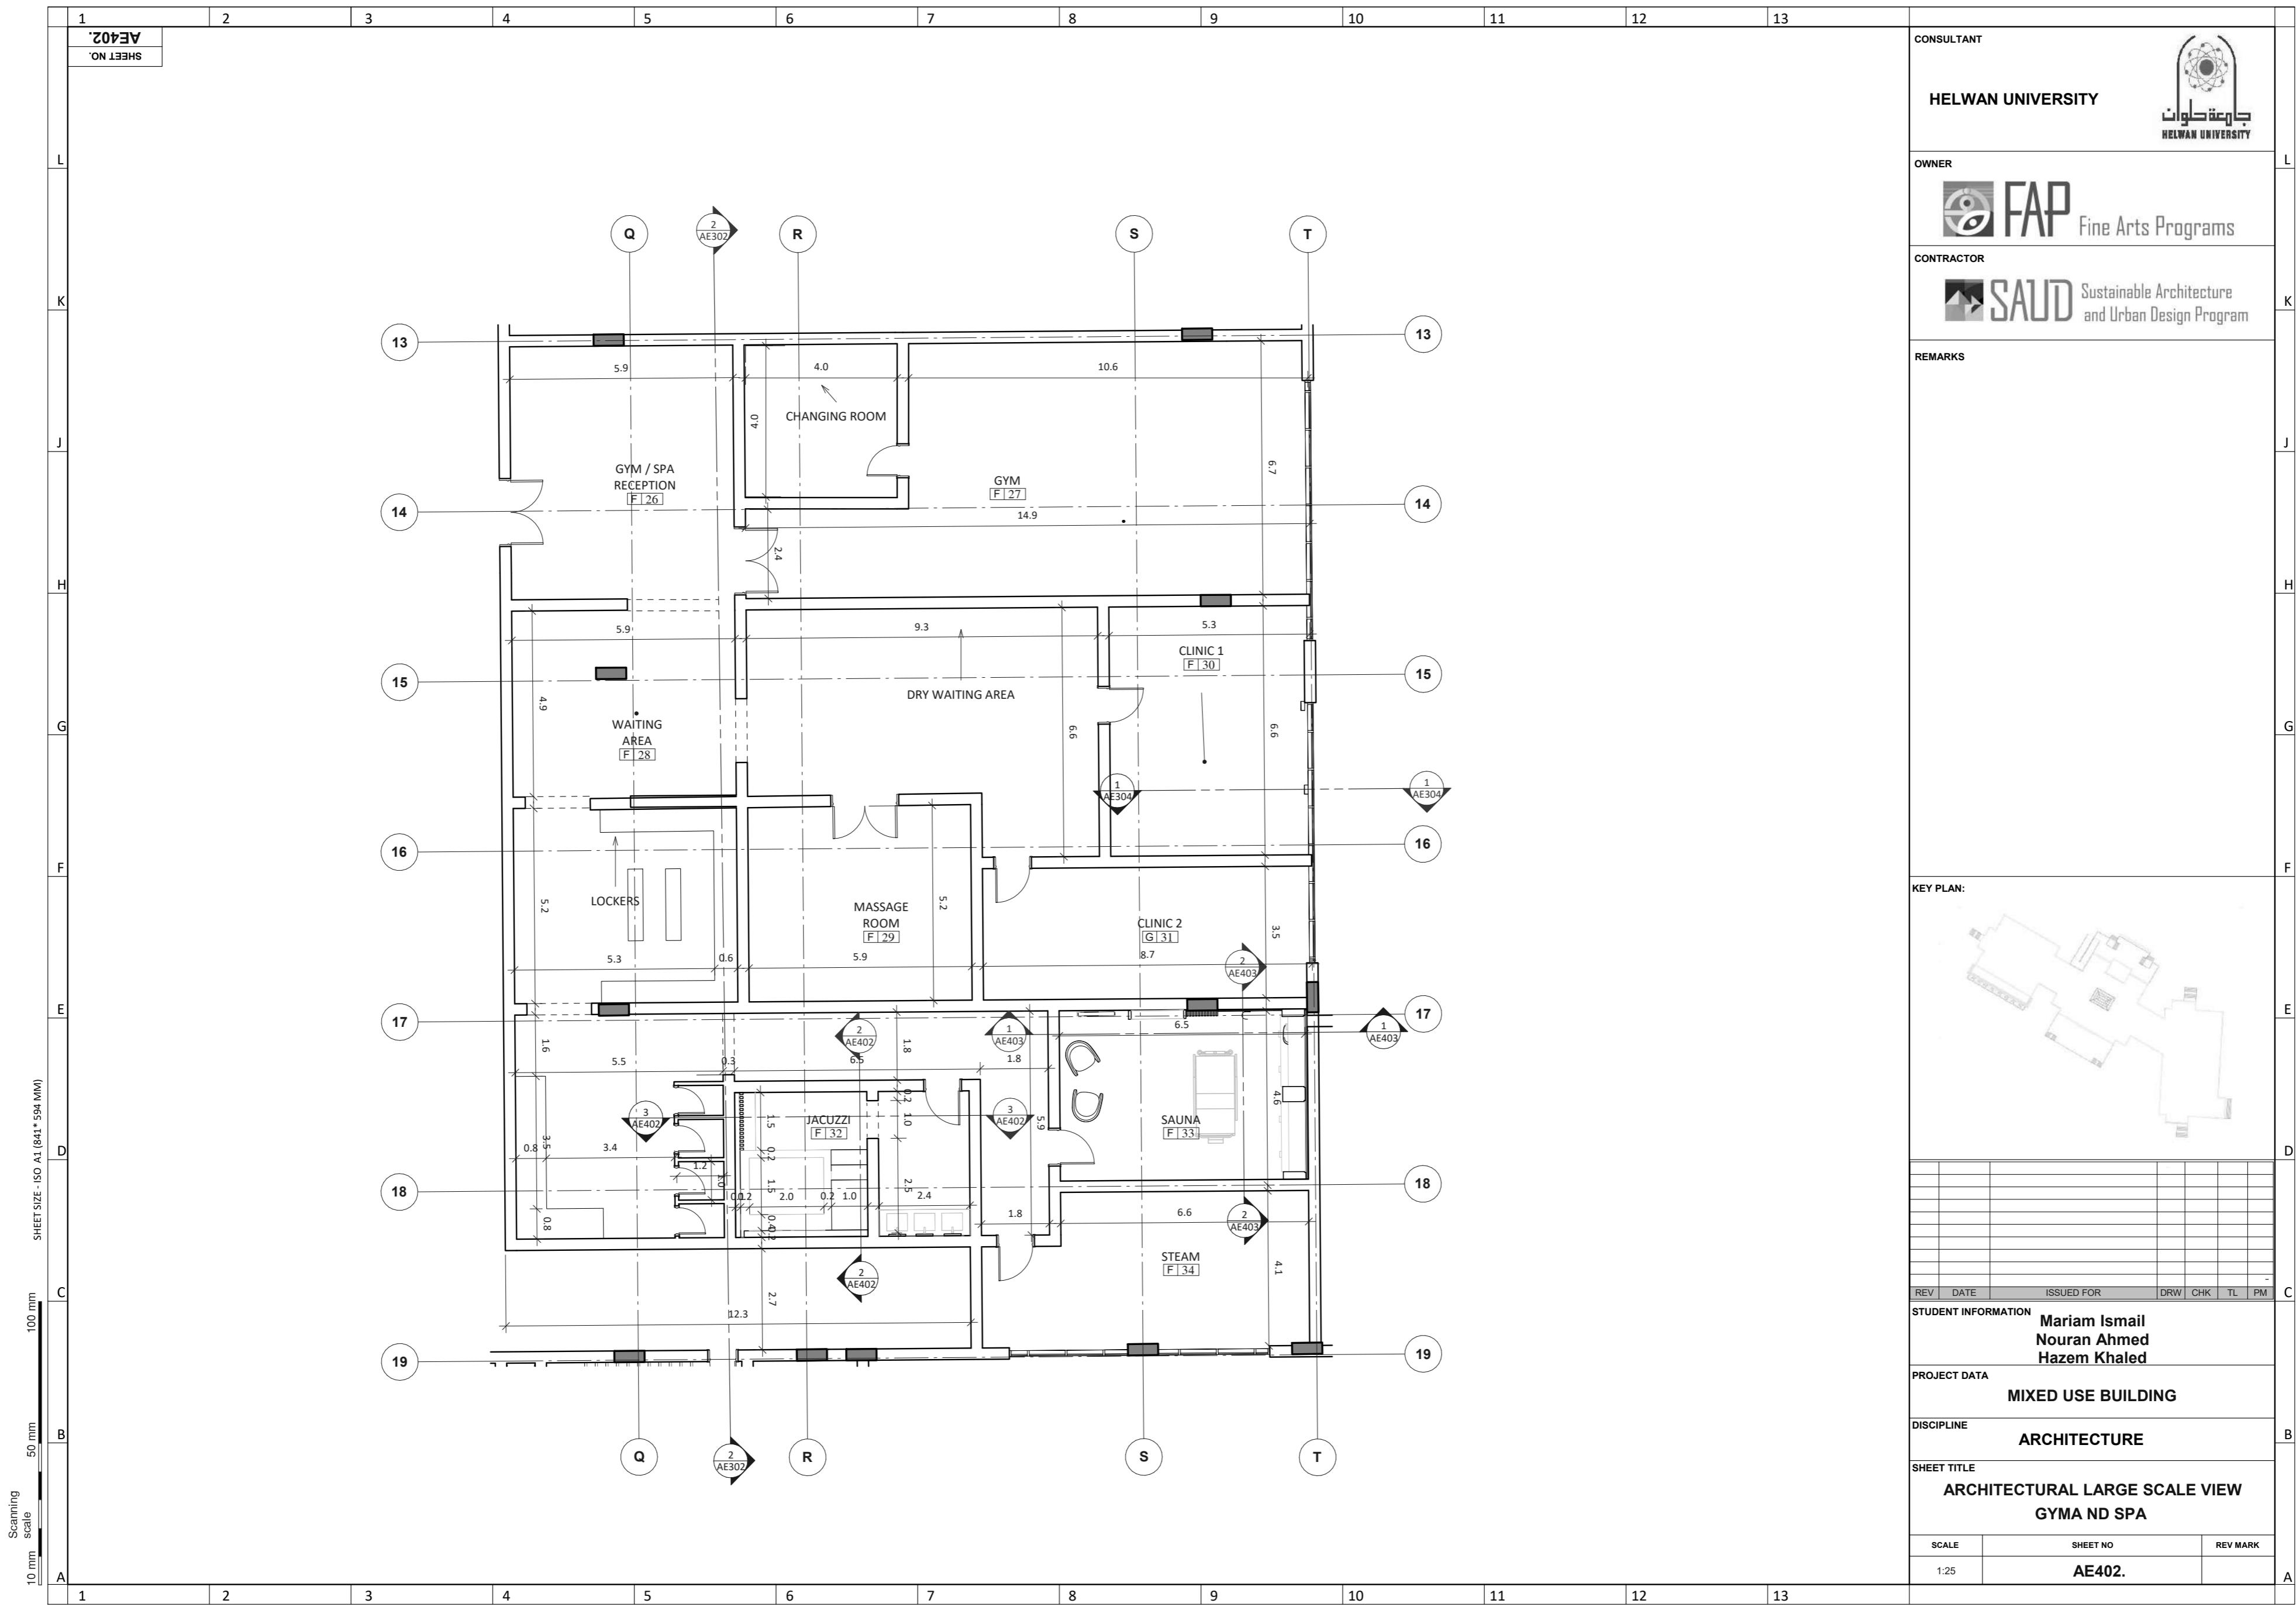

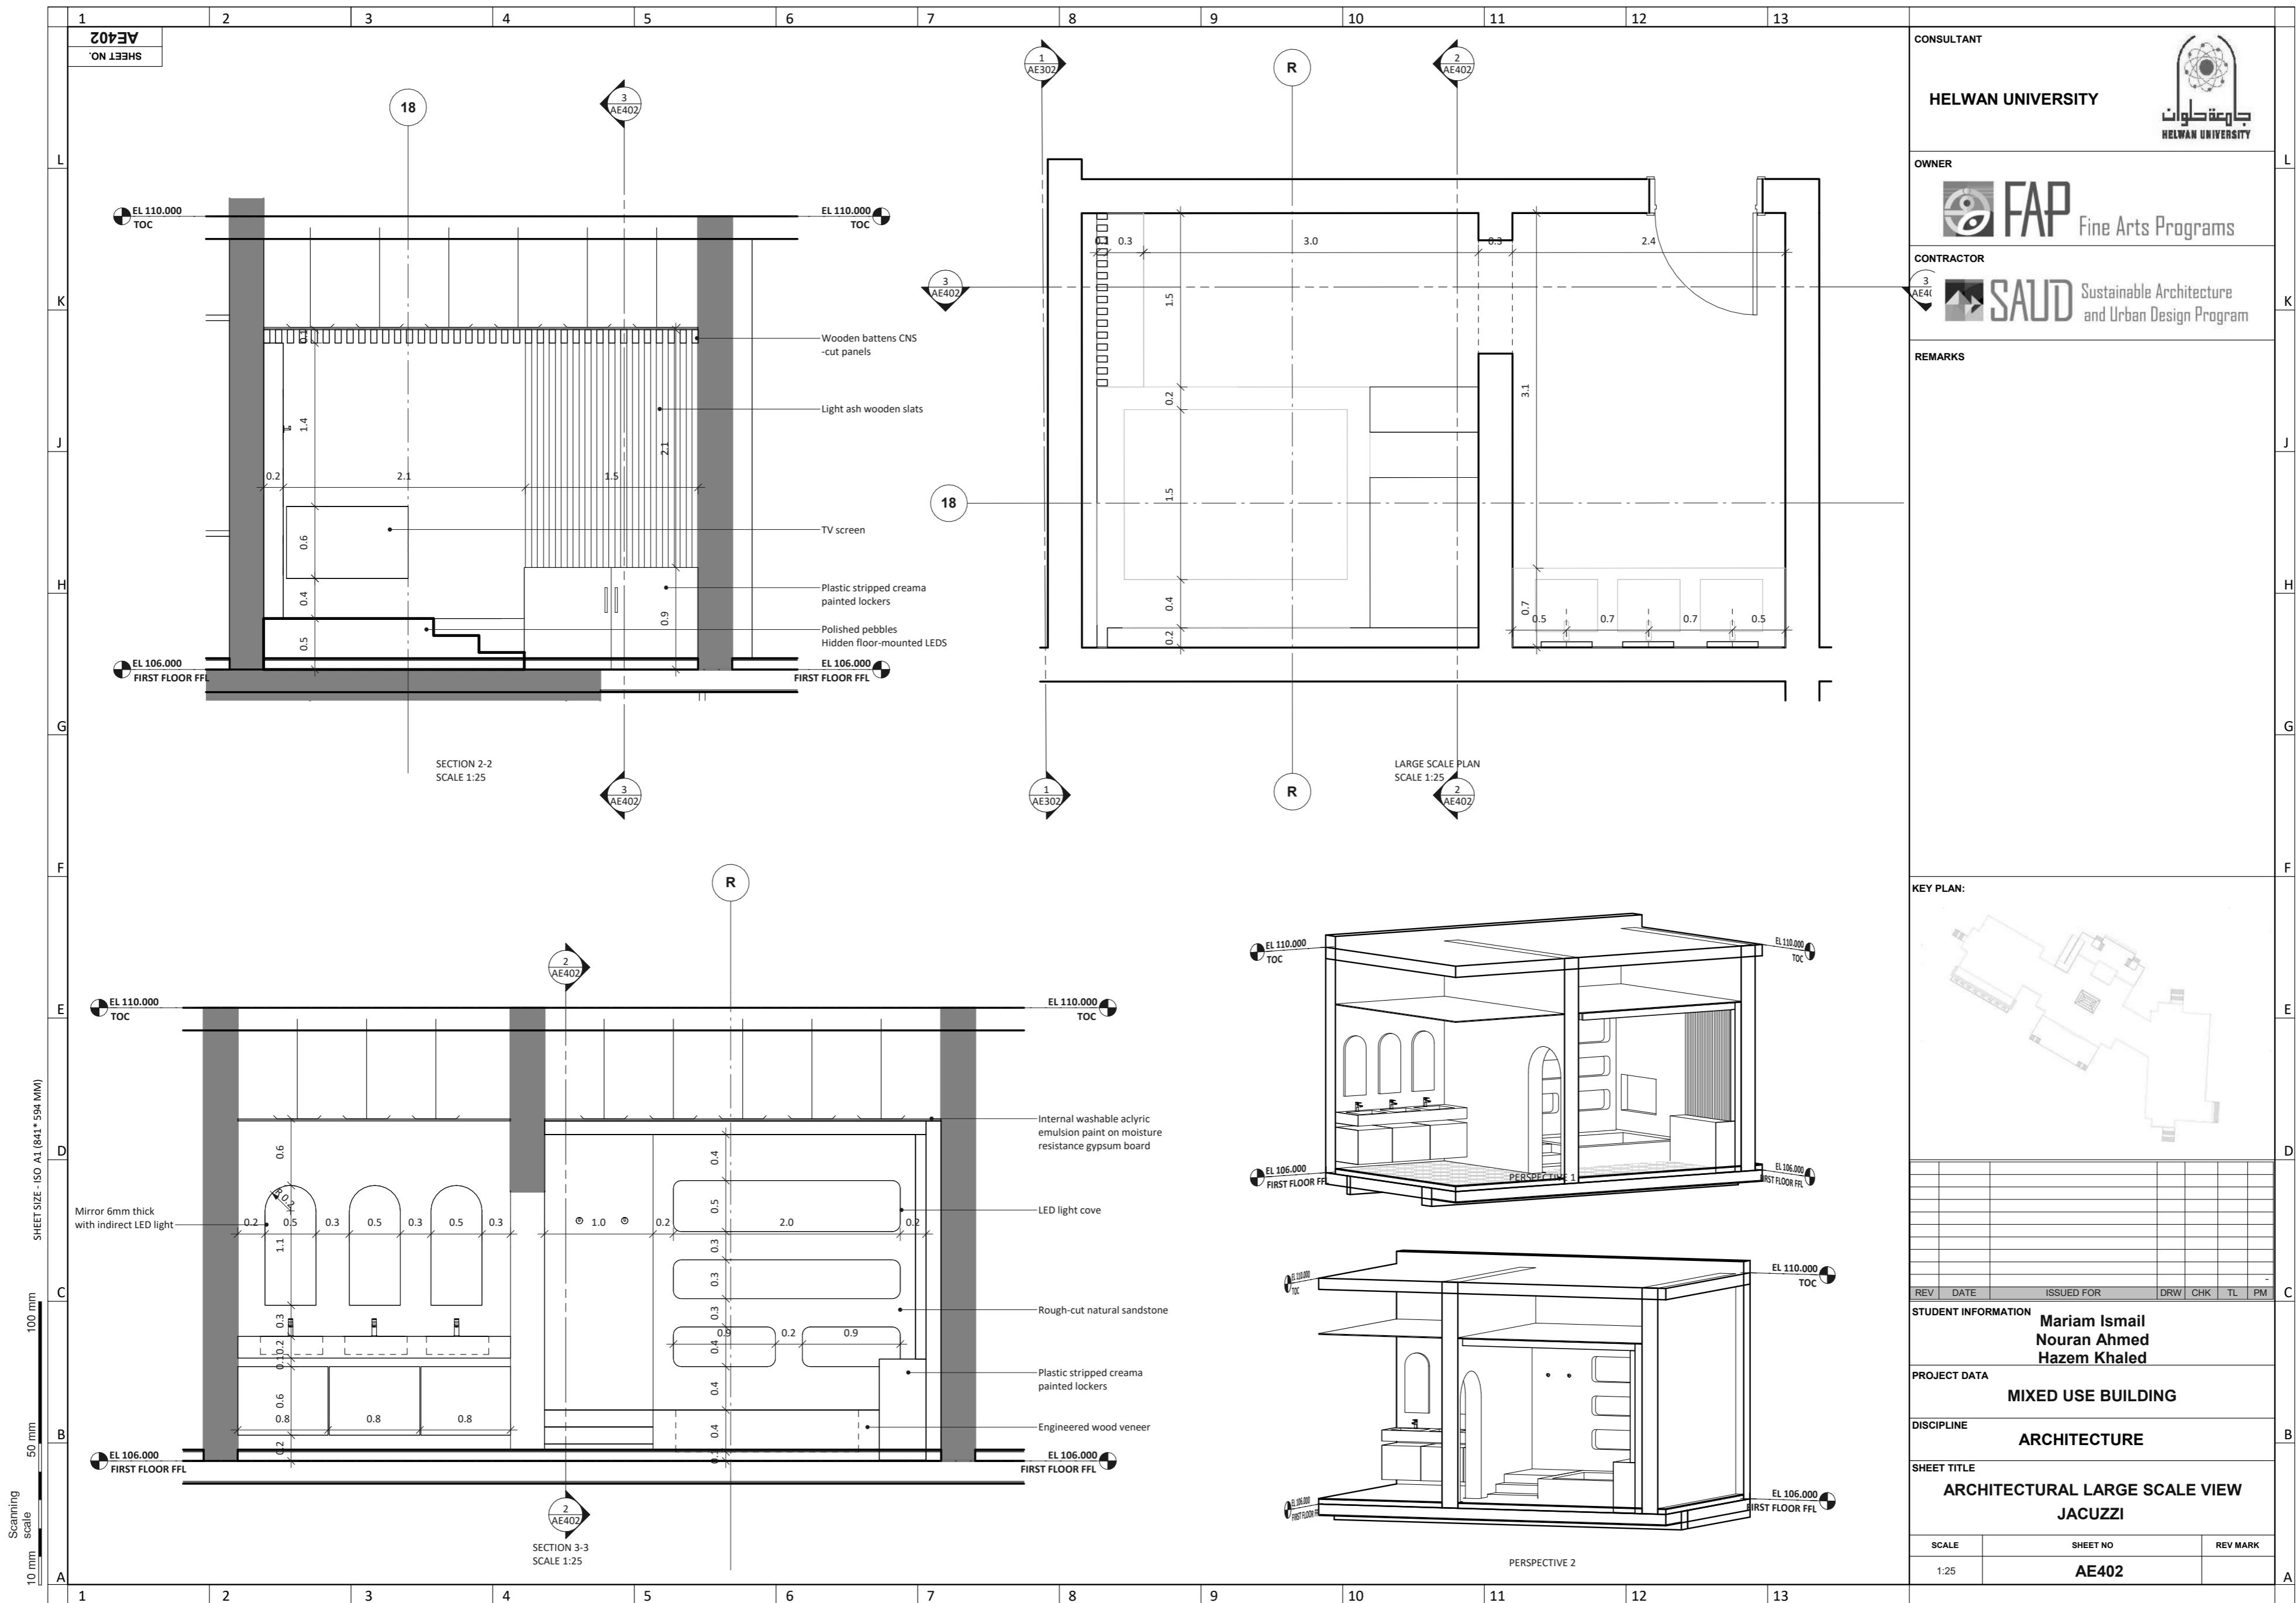

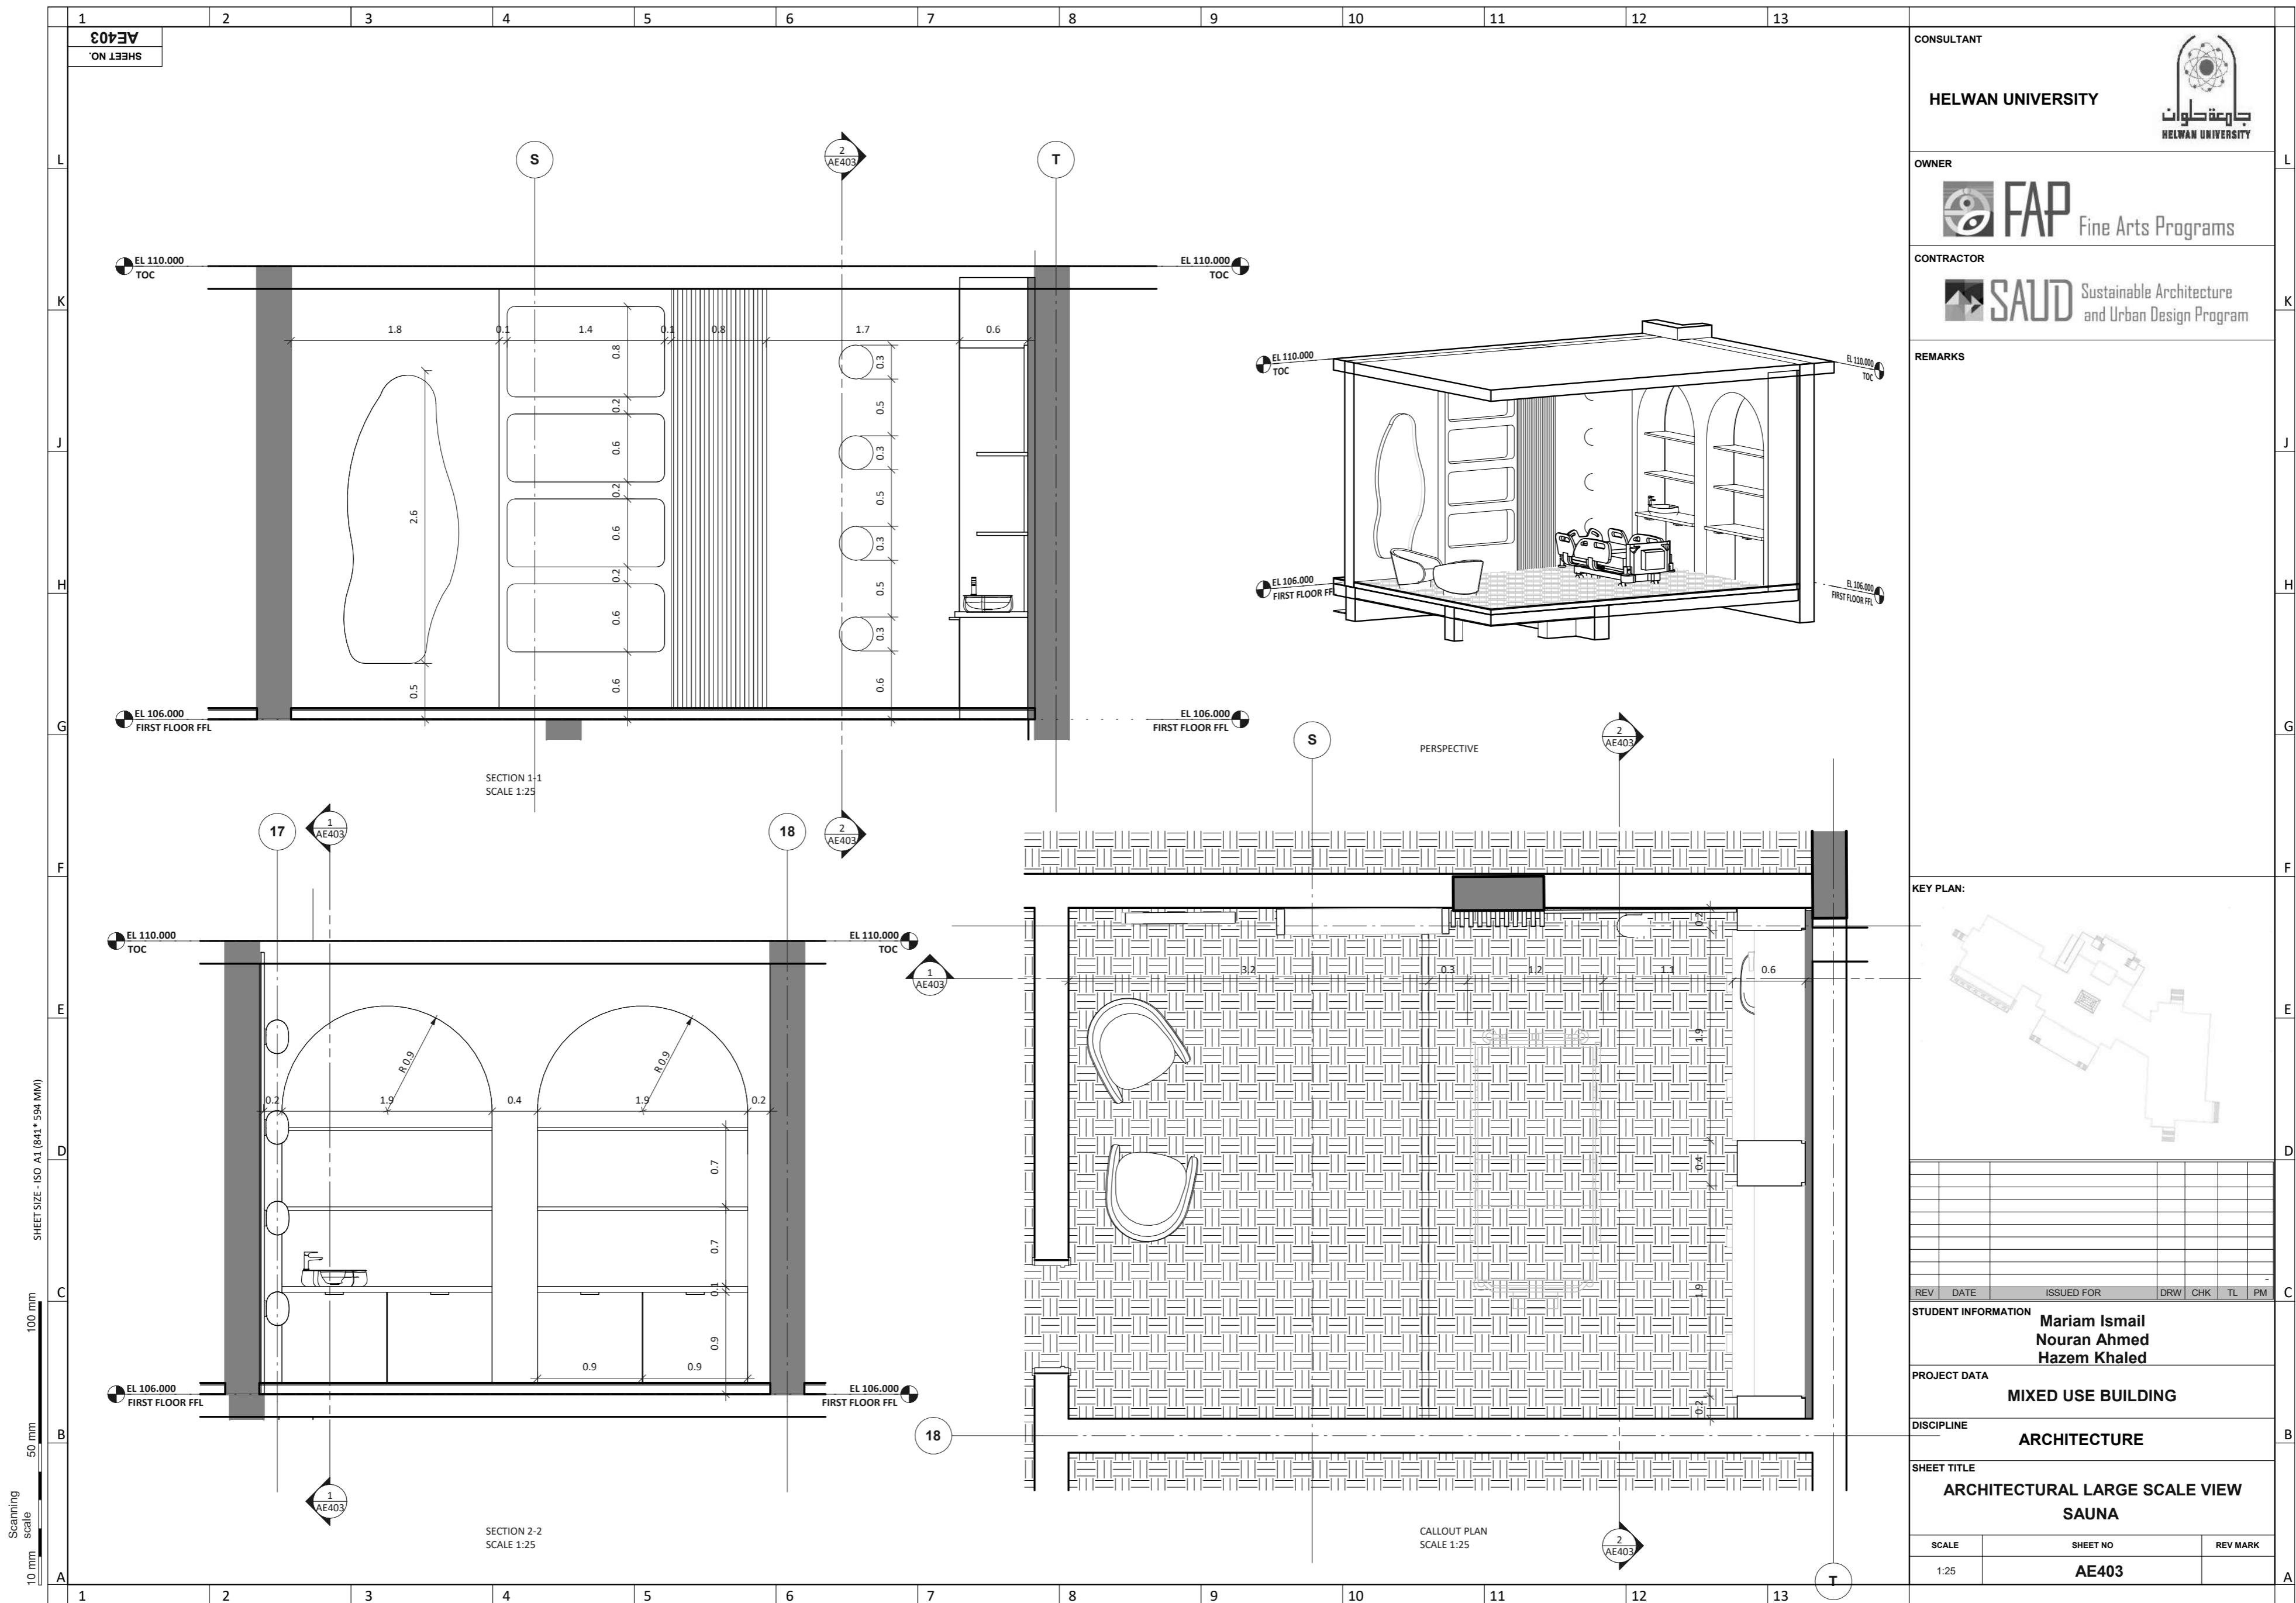


CONSULTANT
HELWAN UNIVERSITY


OWNER


CONTRACTOR


REMARKS

	Item Codes	Item Description
01	WC-01	Water closet
02	WC-02	Wall mounted water closet
03	LAV-01	Counter top wash basin
04	GB-01	Grab bar (300mm)
05	GB-02	Grab bar
06	GB-03	Grab bar (vertical swing)
07	HD-01	Hand dryer
08	PD-01	Paper towel dispenser
09	SD-01	Soap dispenser
10	TB-01	Trash bin
11	UR-01	Wall mounted urinal
12	FD-01	Floor drain

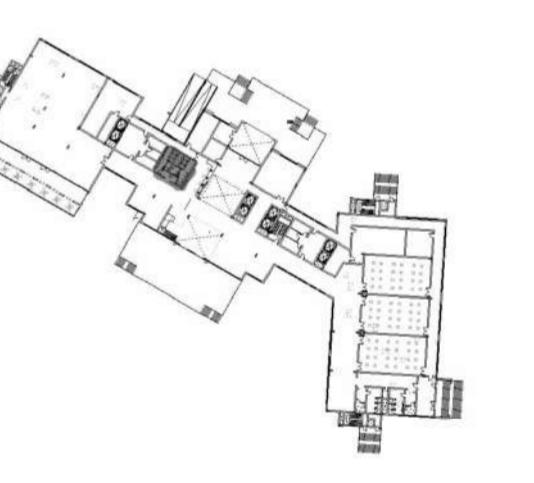KEY PLAN:


STUDENT INFORMATION
Mariam Ismail
Nouran Ahmed
Hazem Khaled

PROJECT DATA
MIXED USE BUILDING

DISCIPLINE
ARCHITECTURE

SHEET TITLE
PUBLIC TOILETS PLAN


REV	DATE	ISSUED FOR	DRW	CHK	TL	PM
-----	------	------------	-----	-----	----	----


SCALE
1:25

SHEET NO
AE404

REV MARK

Scanning scale
100 mm
50 mm
10 mm

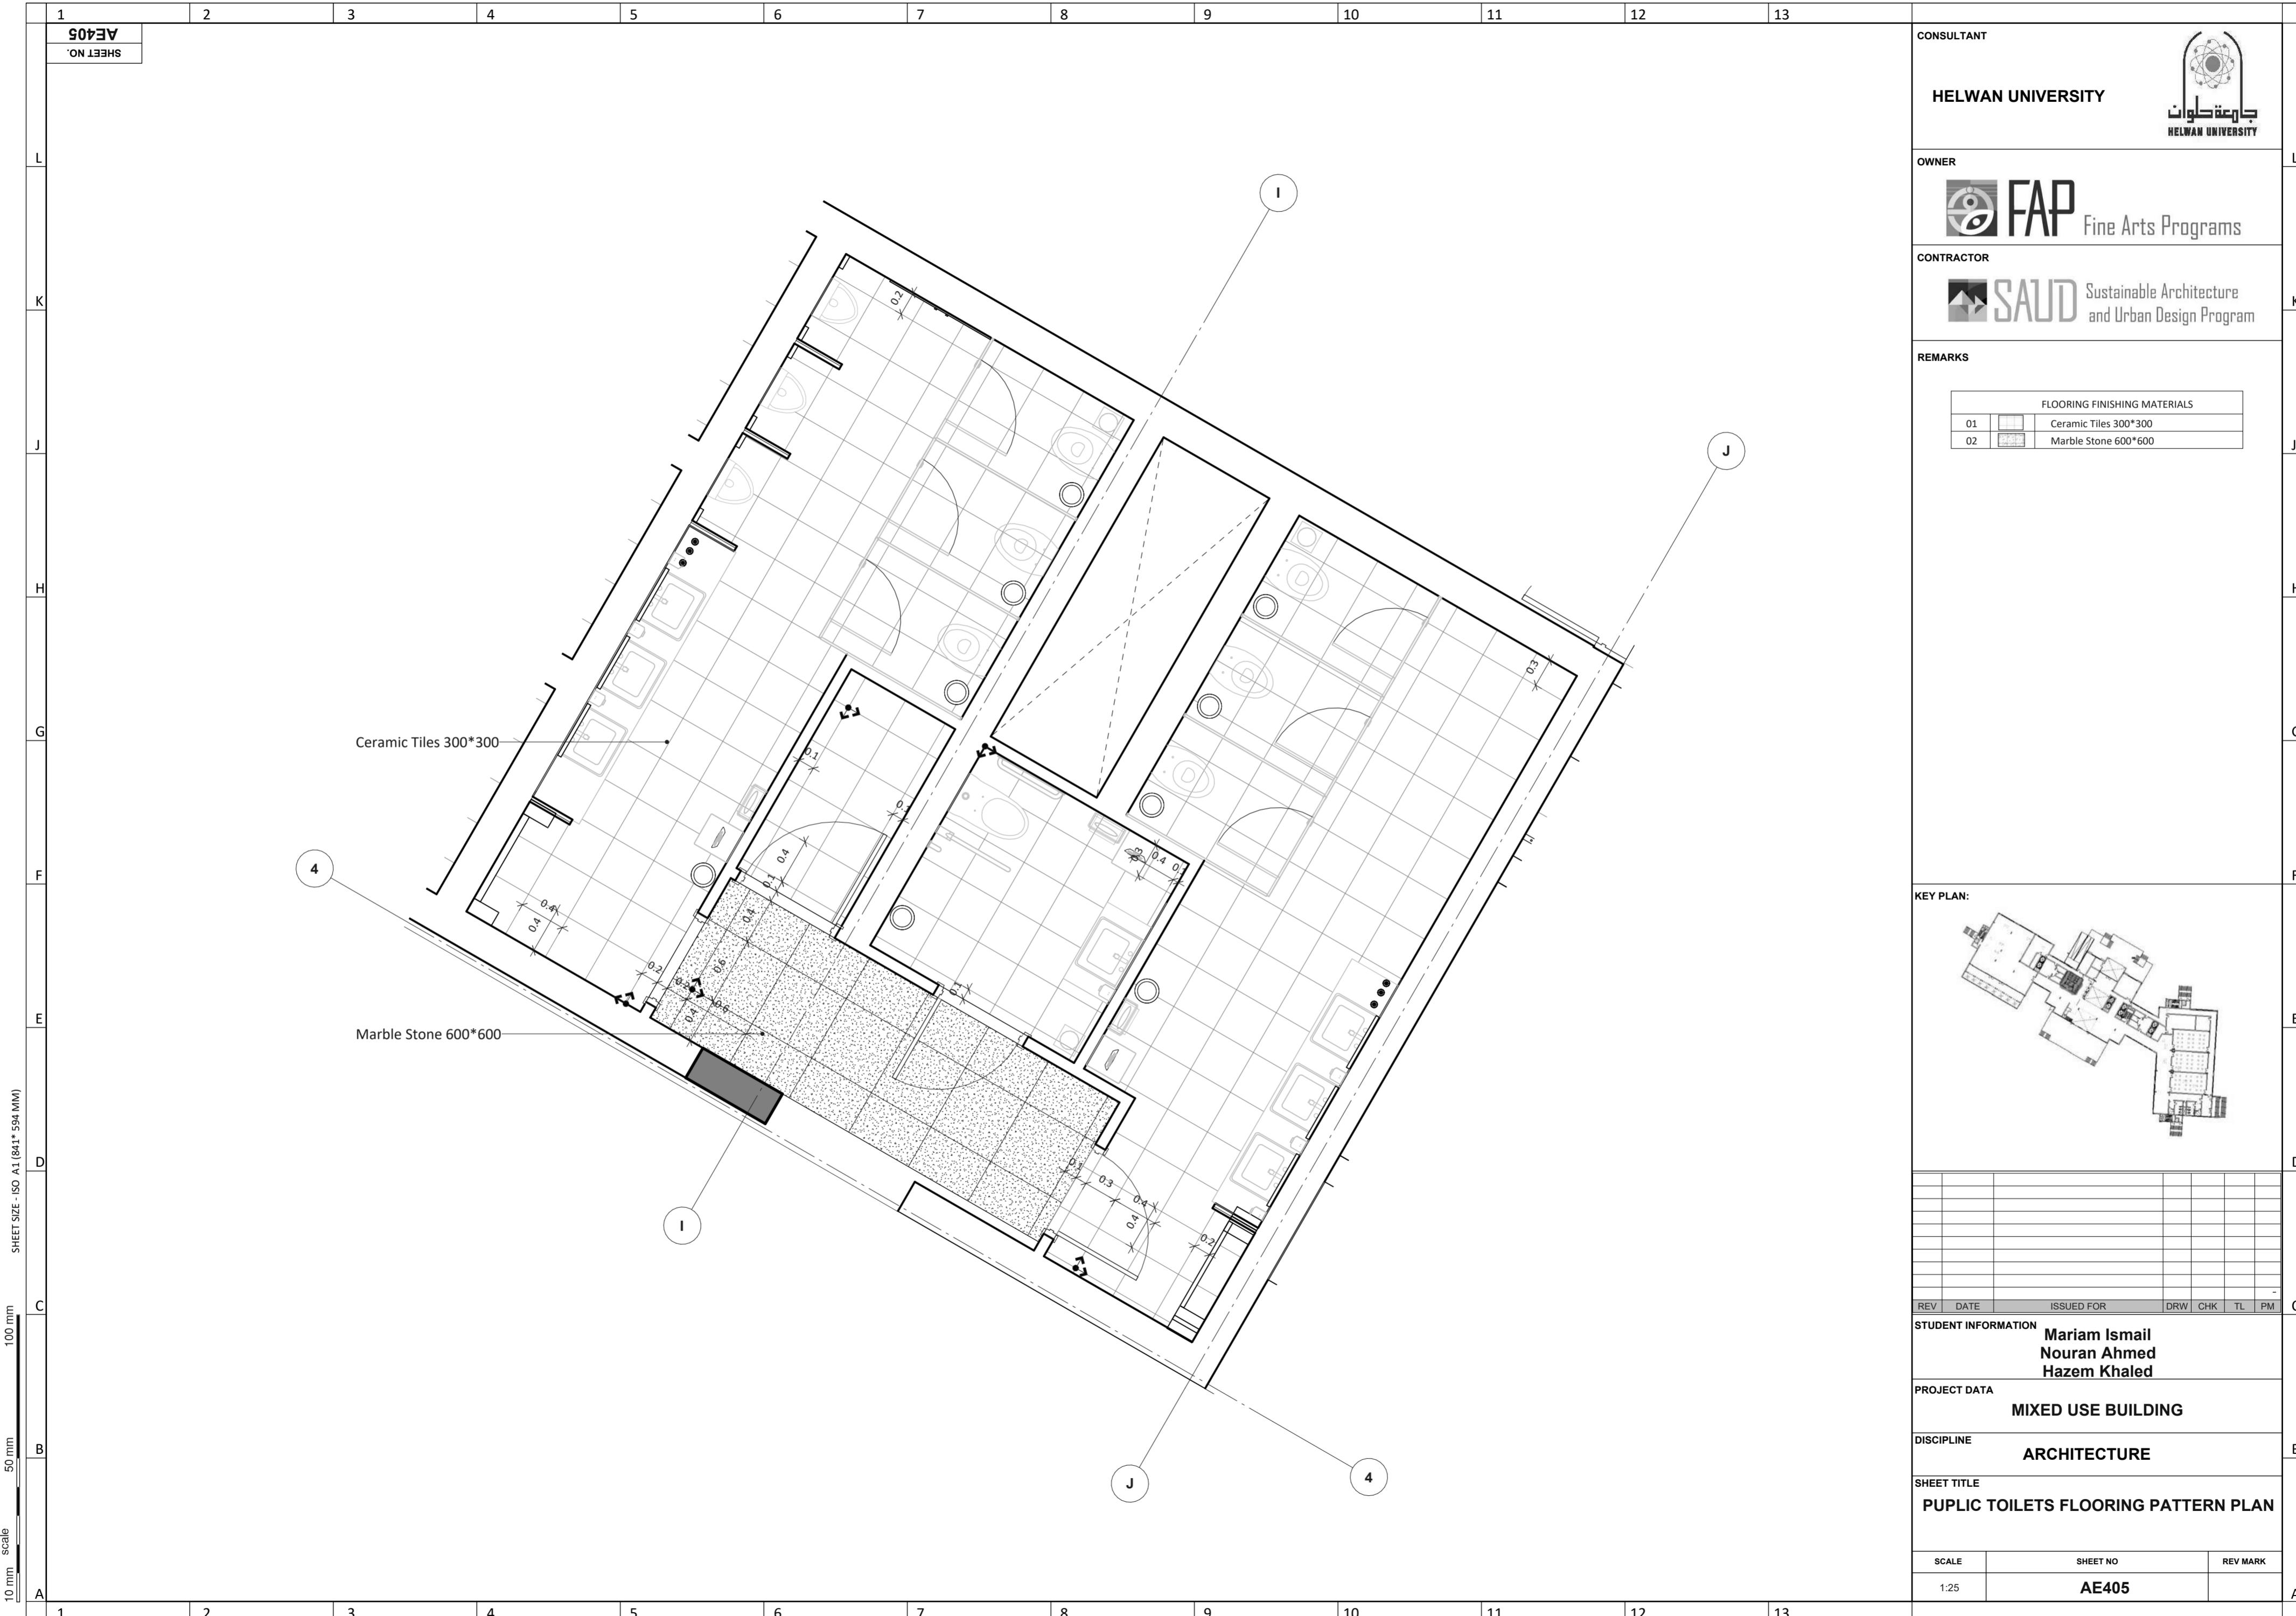

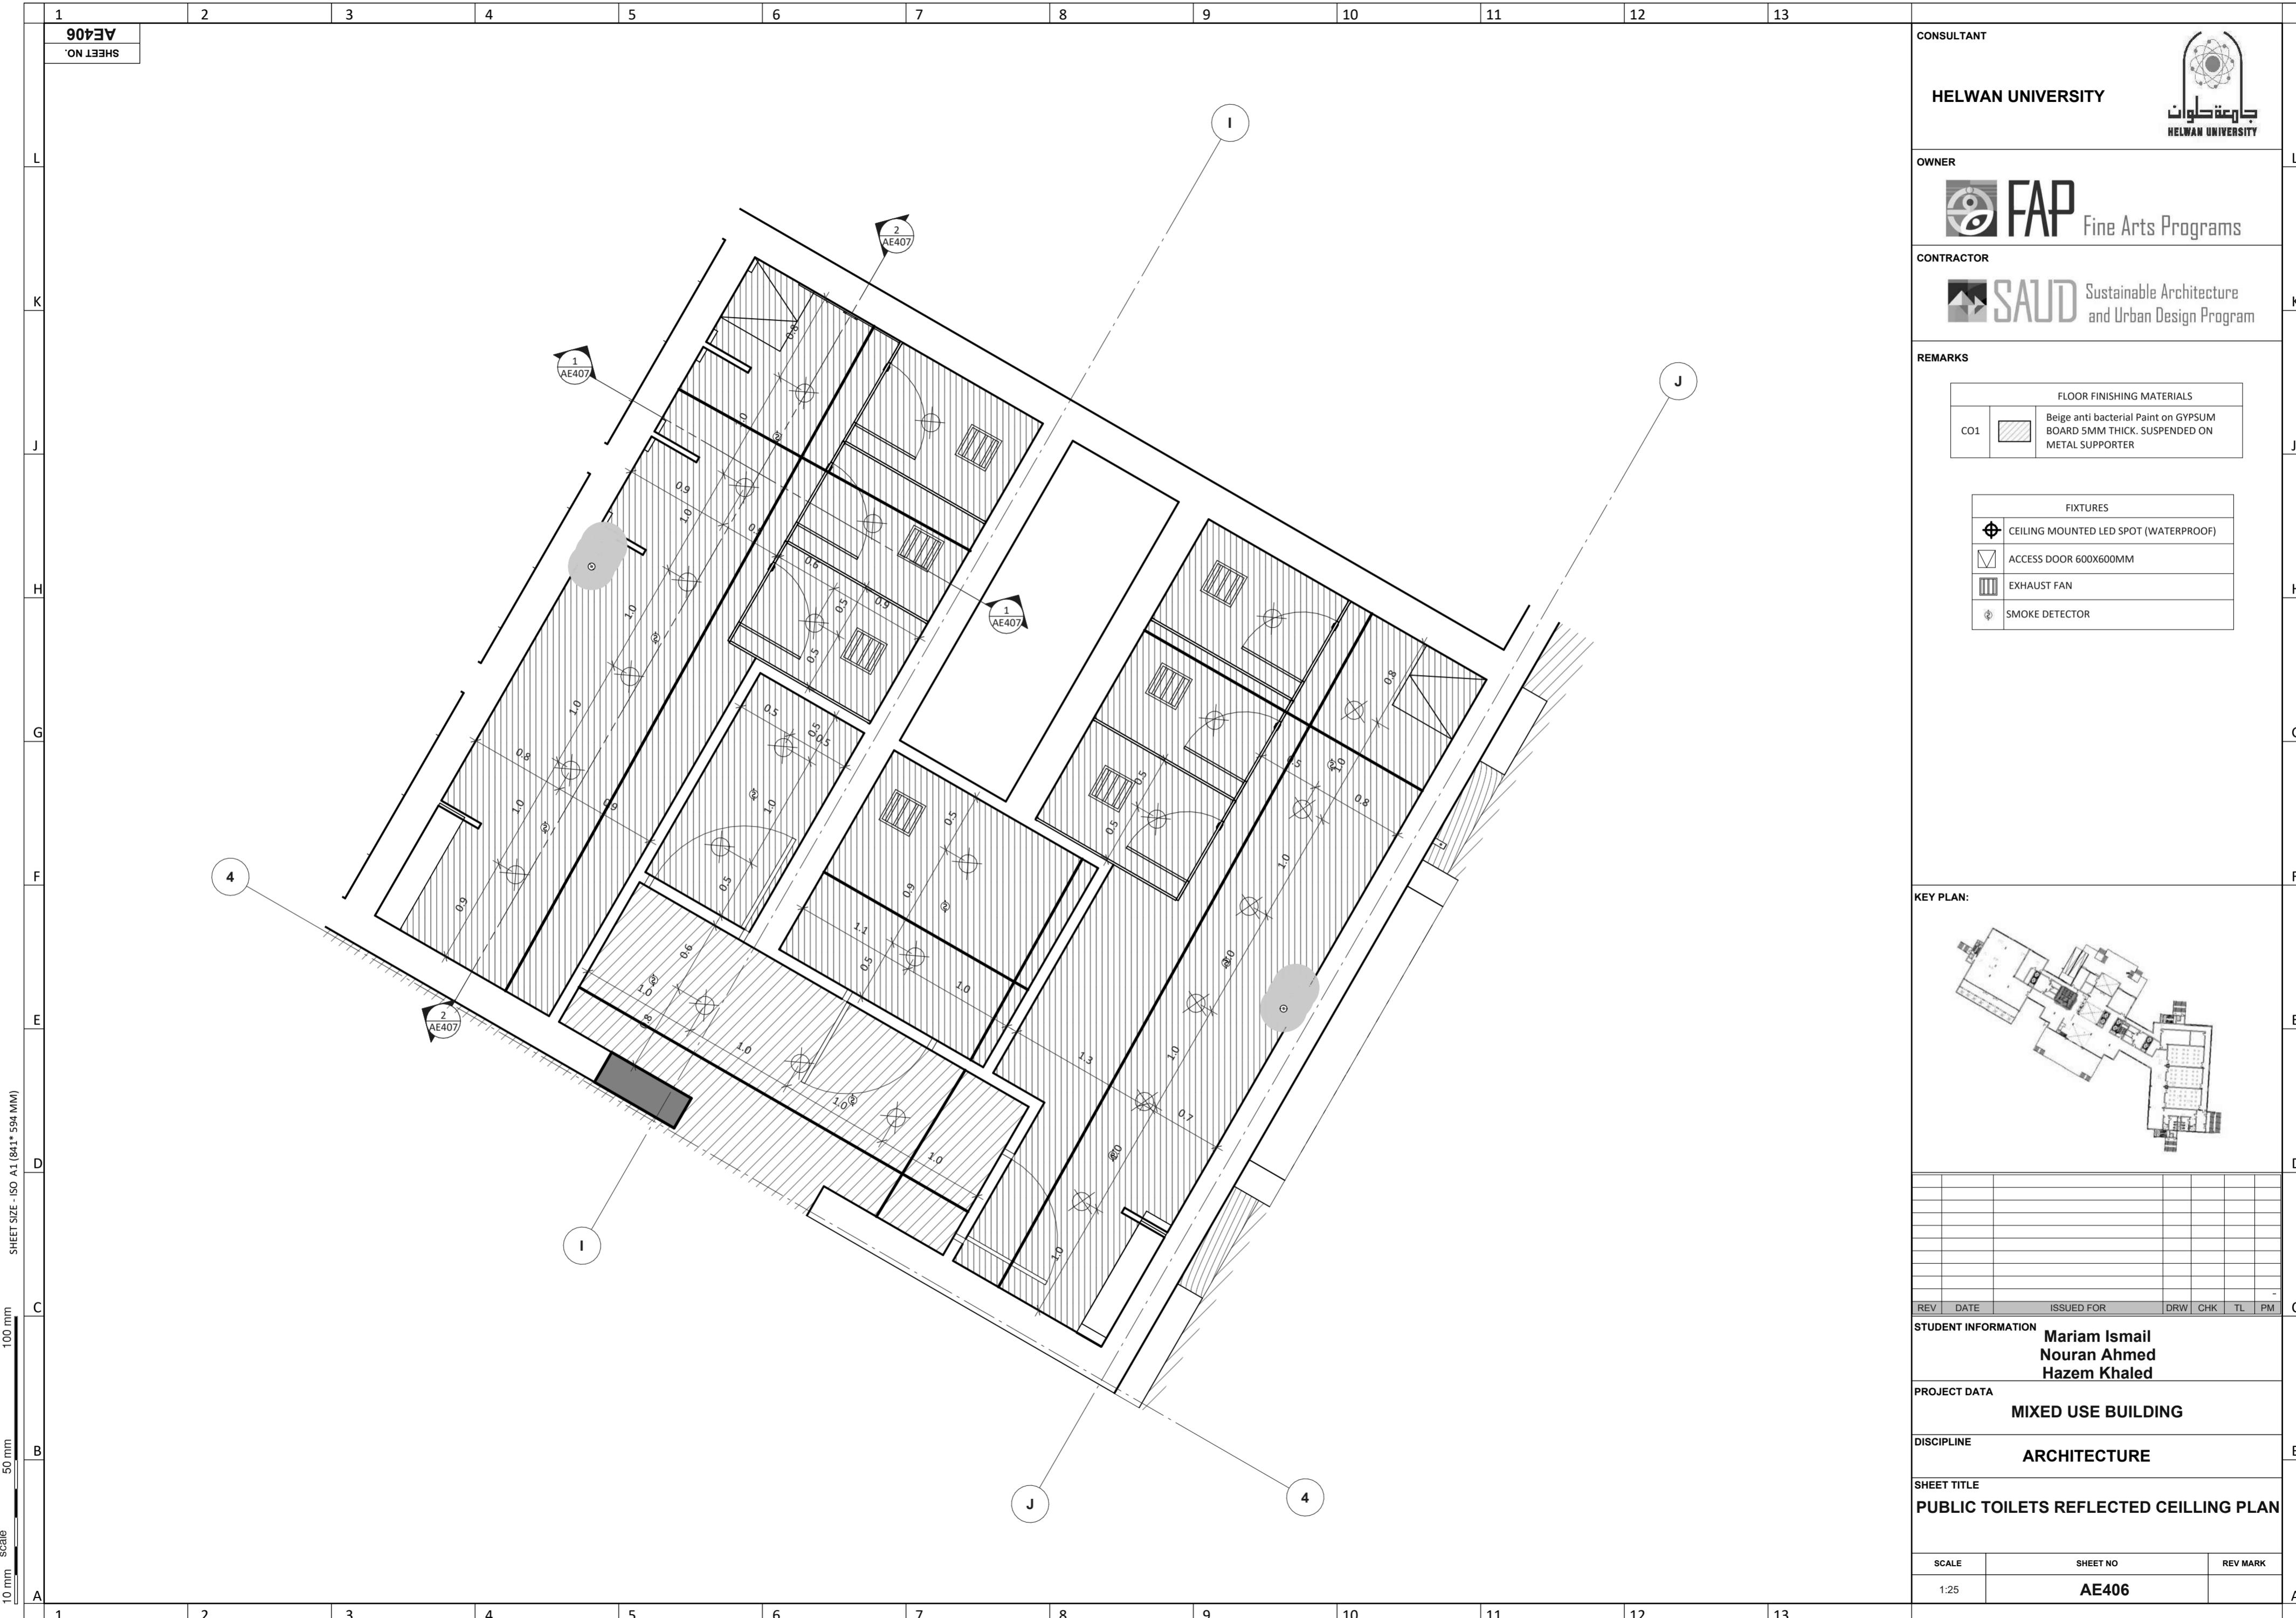

1 2 3 4 5 6 7 8 9 10 11 12 13
 SHEET NO. AE407
 Scanning scale 10mm 50mm 100mm
 SHEET SIZE - ISO A1 (841*594 MM)


CONSULTANT
HELWAN UNIVERSITY


OWNER


CONTRACTOR



REMARKS


	Item Codes	Item Description
01	WC-01	Water closet
02	WC-02	Wall mounted water closet
03	LAV-01	Counter top wash basin
04	GB-01	Grab bar (300mm)
05	GB-02	Grab bar
06	GB-03	Grab bar (vertical swing)
07	HD-01	Hand dryer
08	PD-01	Paper towel dispenser
09	SD-01	Soap dispenser
10	TB-01	Trash bin
11	UR-01	Wall mounted urinal
12	FD-01	Floor drain

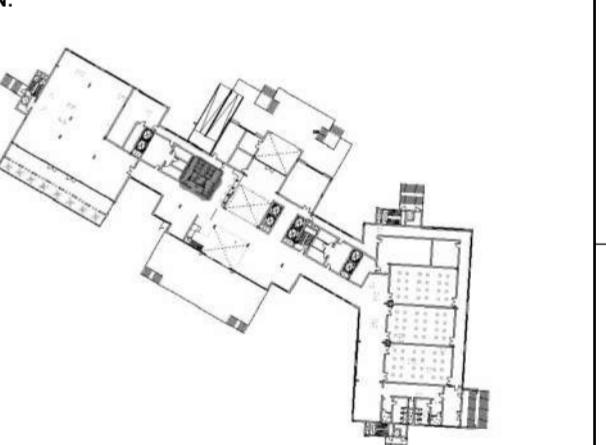KEY PLAN:


STUDENT INFORMATION
 Mariam Ismail
 Nouran Ahmed
 Hazem Khaled

PROJECT DATA
MIXED USE BUILDING
DISCIPLINE
ARCHITECTURE
SHEET TITLE
PUBLIC TOILETS SECTION ELEVATION 1,2 AND 3D VIEW
SCALE 1:25 **SHEET NO.** AE407 **REV MARK**

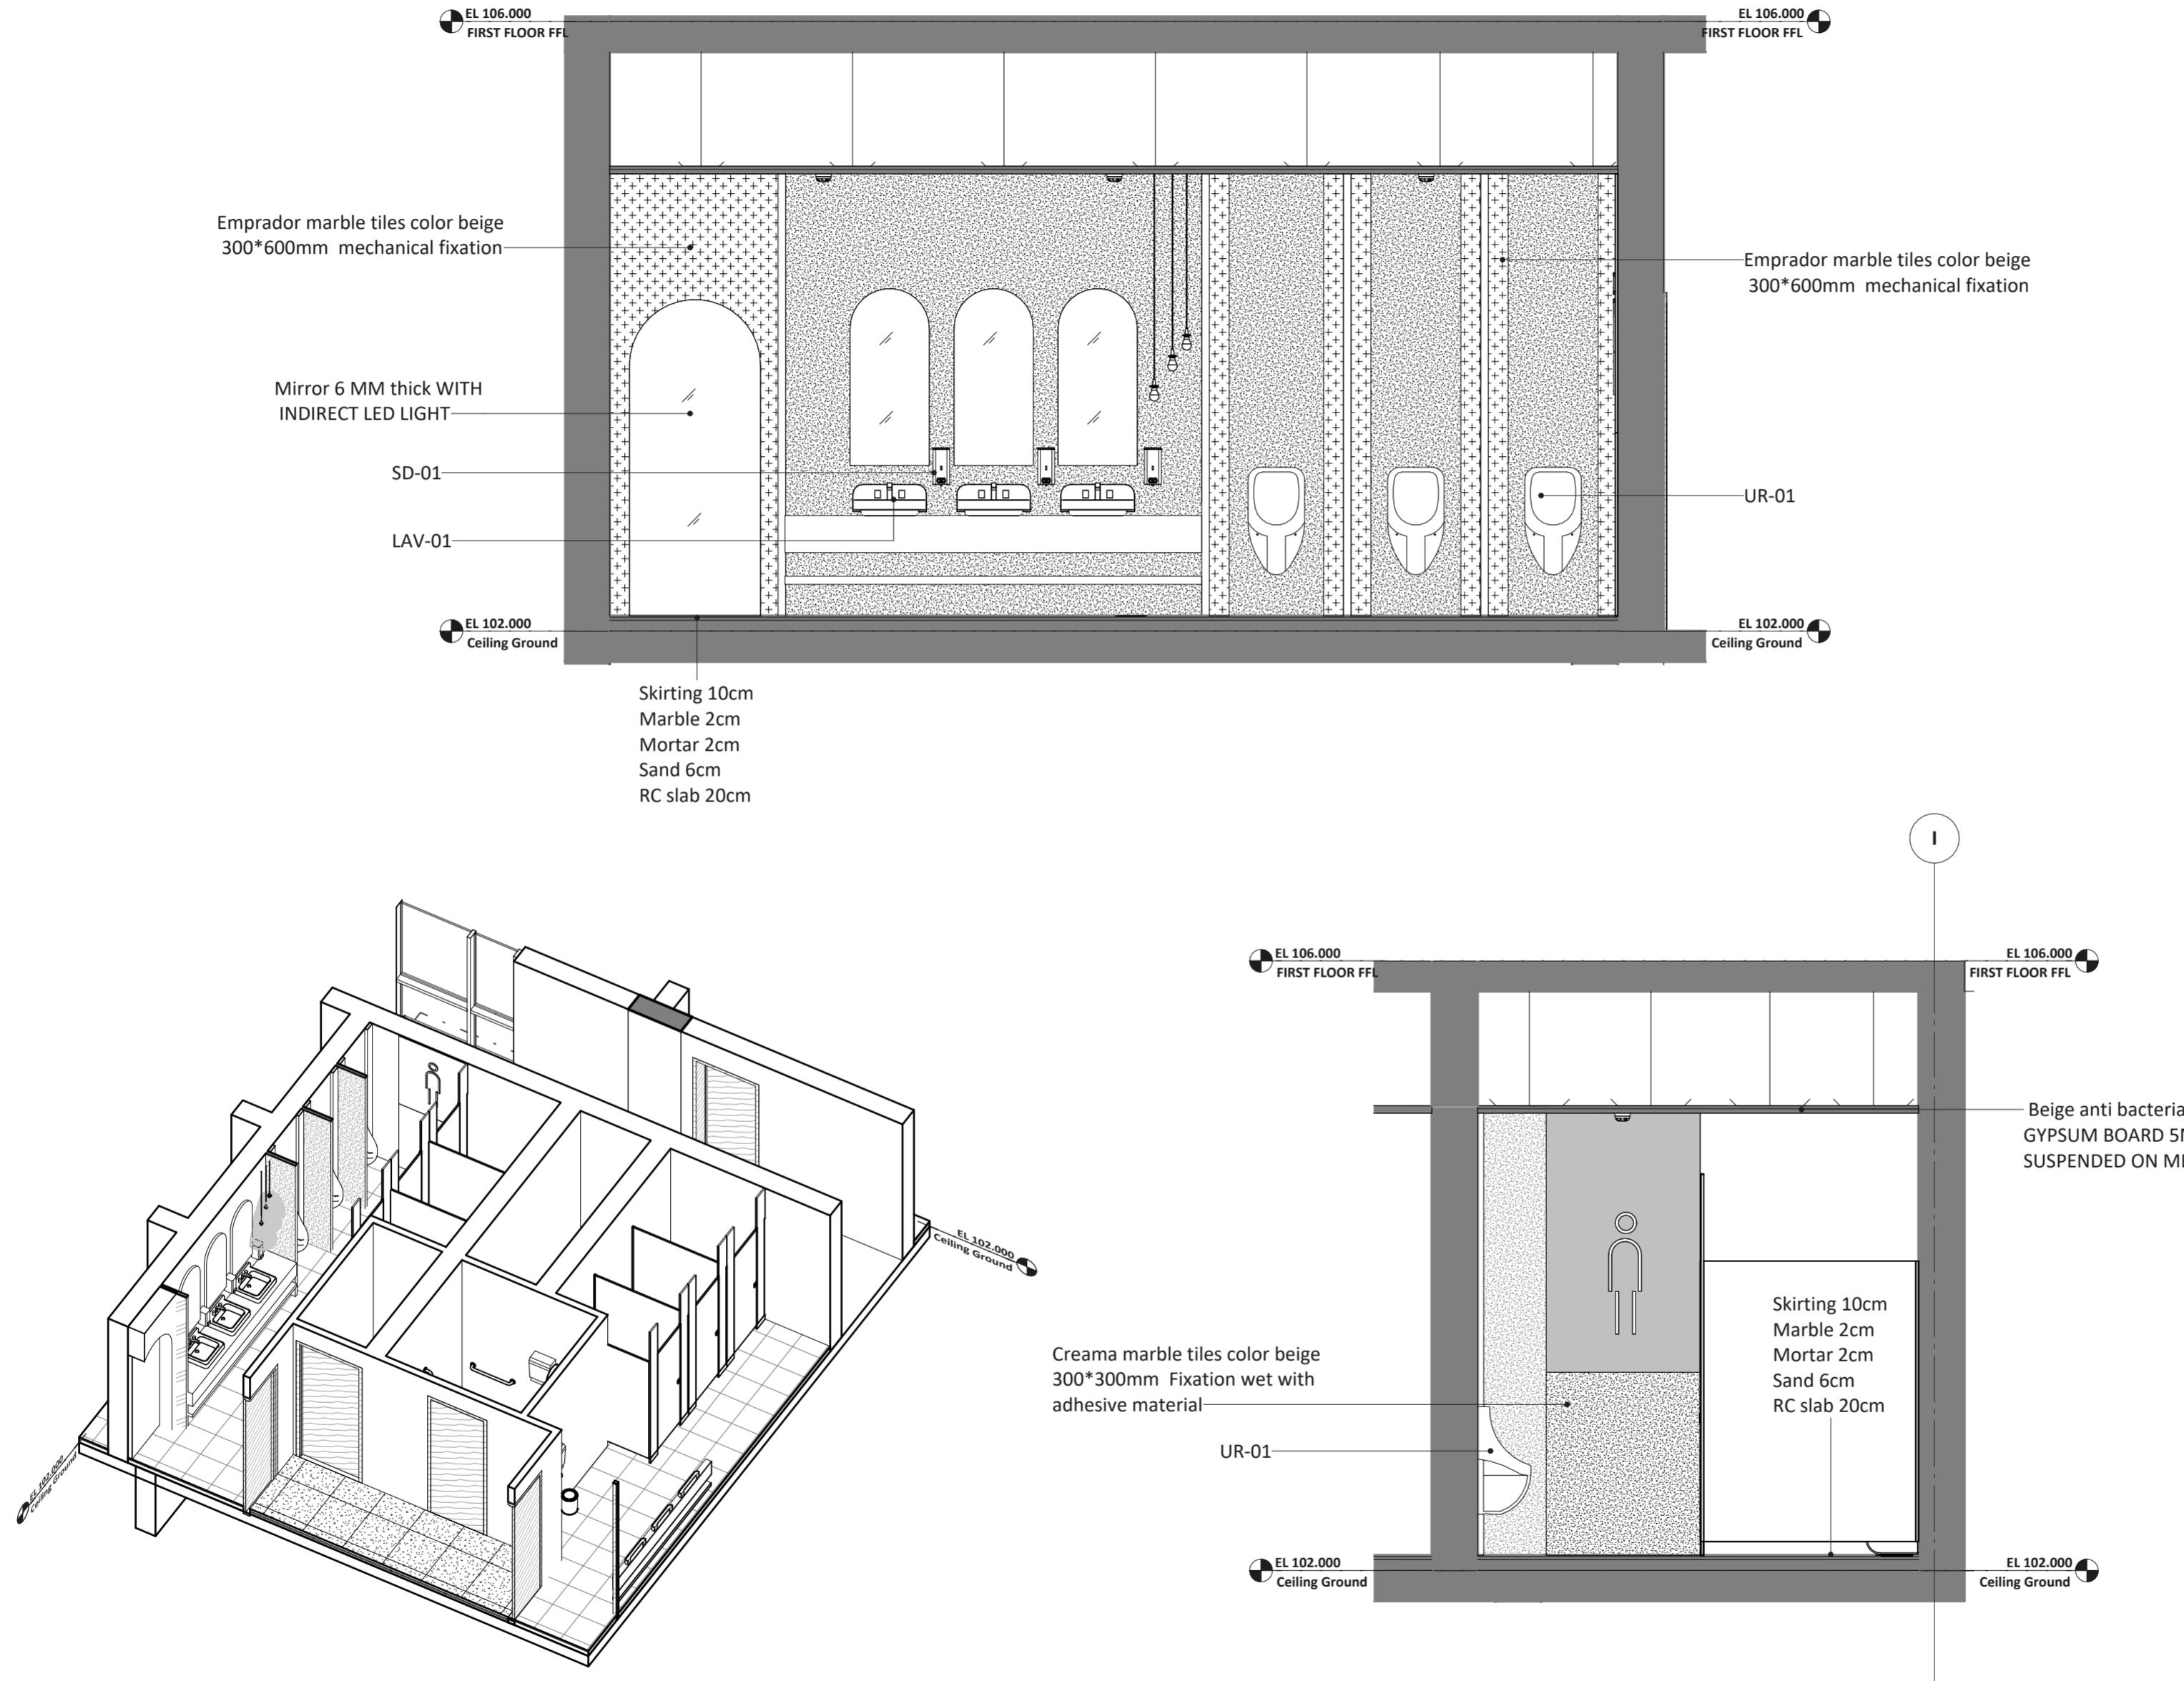SECTION ELEVATION 1,2

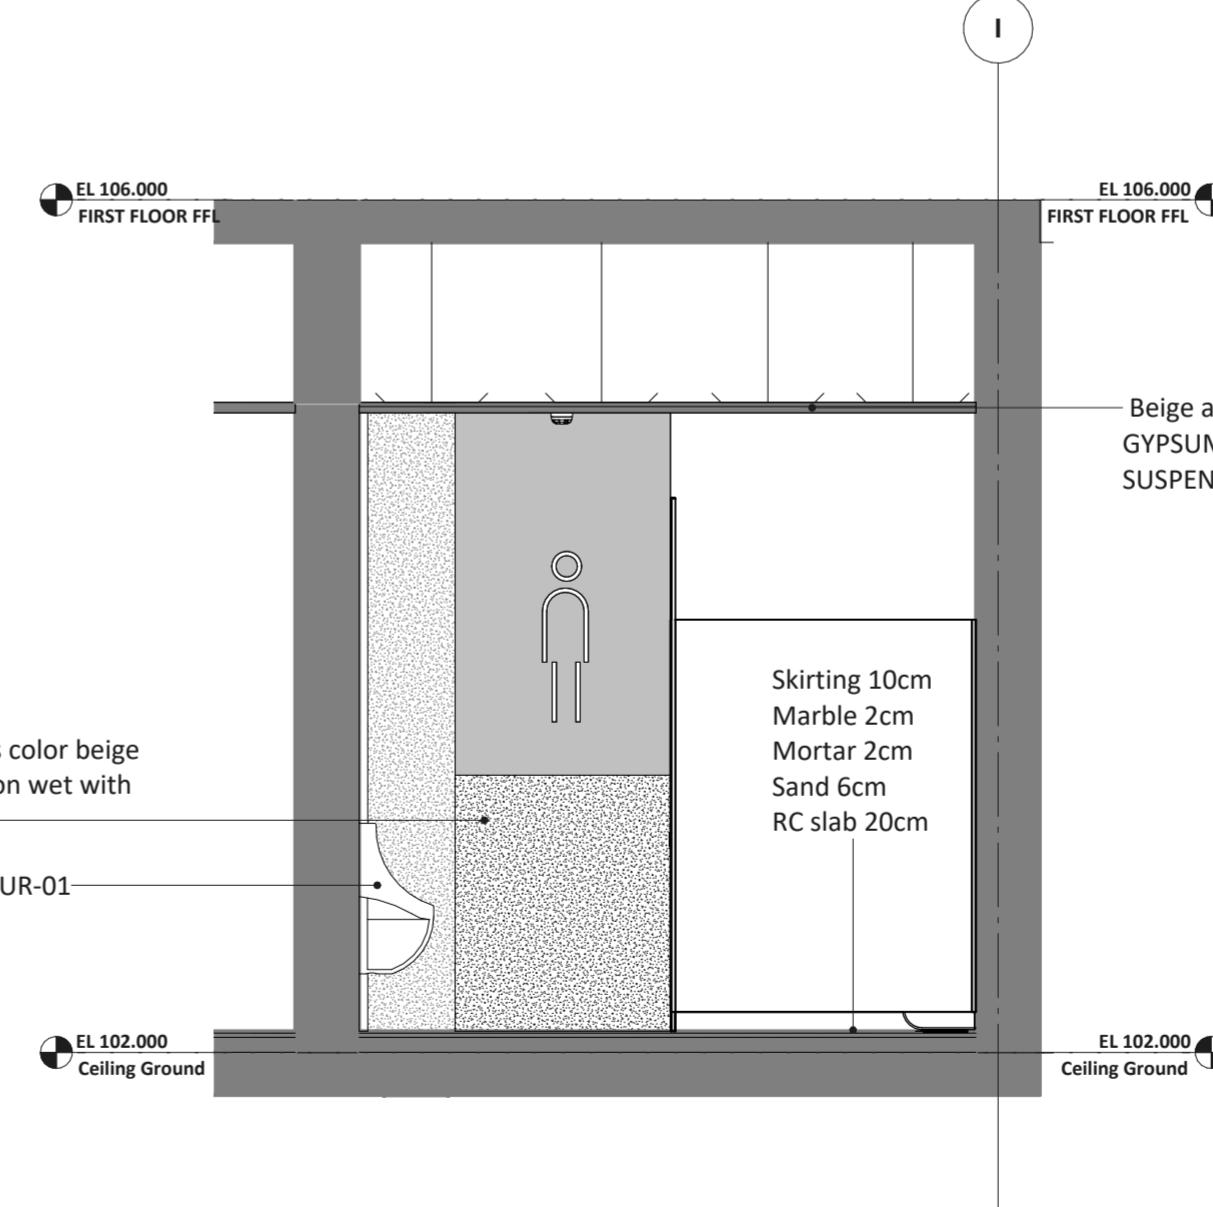
SECTION ELEVATION 1,2


CONSULTANT
HELWAN UNIVERSITY 

OWNER


CONTRACTOR


REMARKS

KEY PLAN:

STUDENT INFORMATION
Mariam Ismail
Nouran Ahmed
Hazem Khaled





PROJECT DATA
MIXED USE BUILDING

DISCIPLINE
ARCHITECTURE

SHEET TITLE
ARCHITECTURAL TYPES AND DETAILS

SCALE **SHEET NO** **REV MARK**

AE501

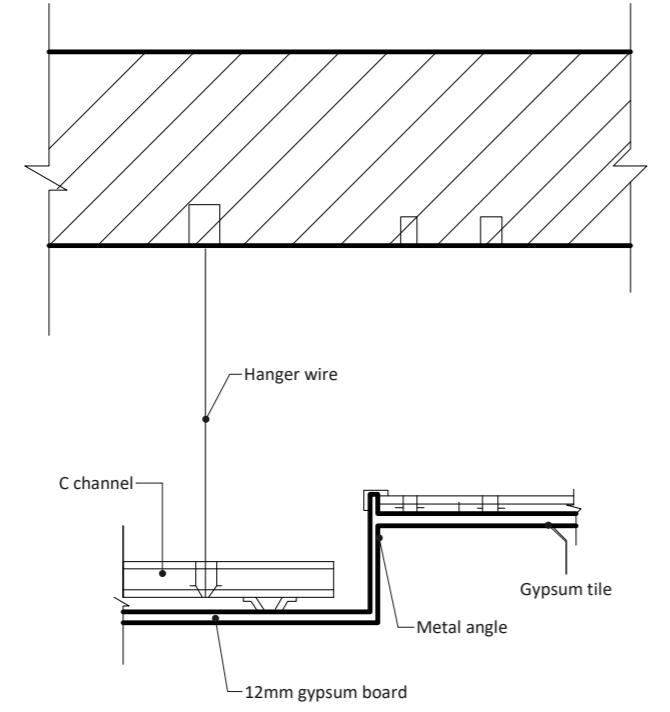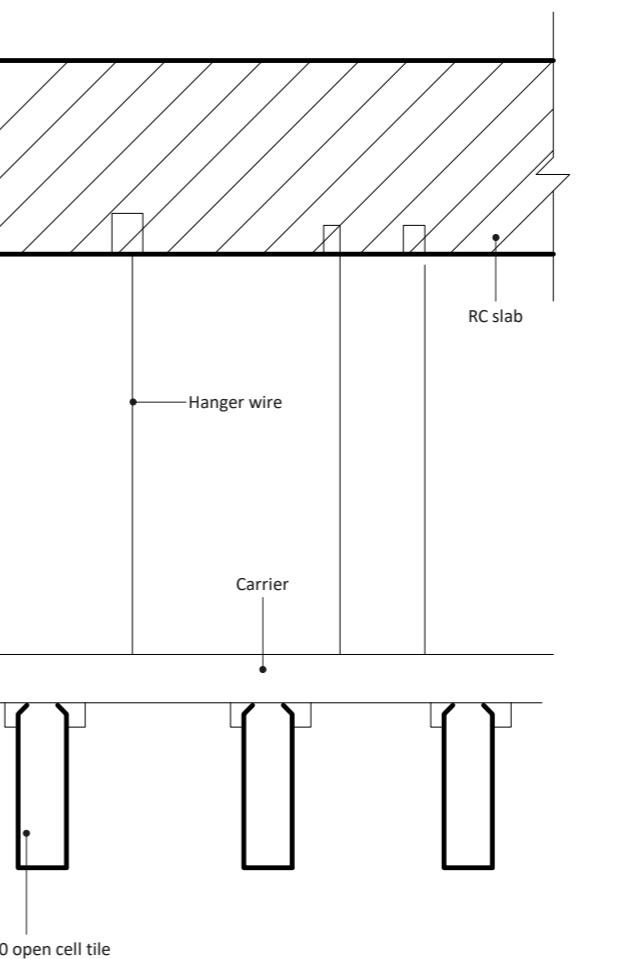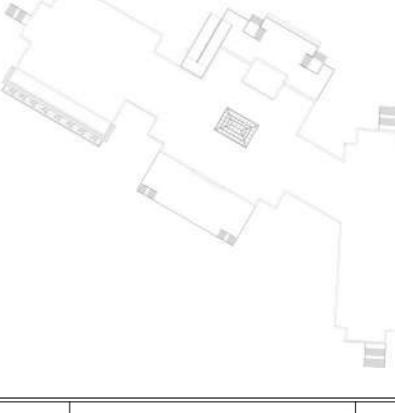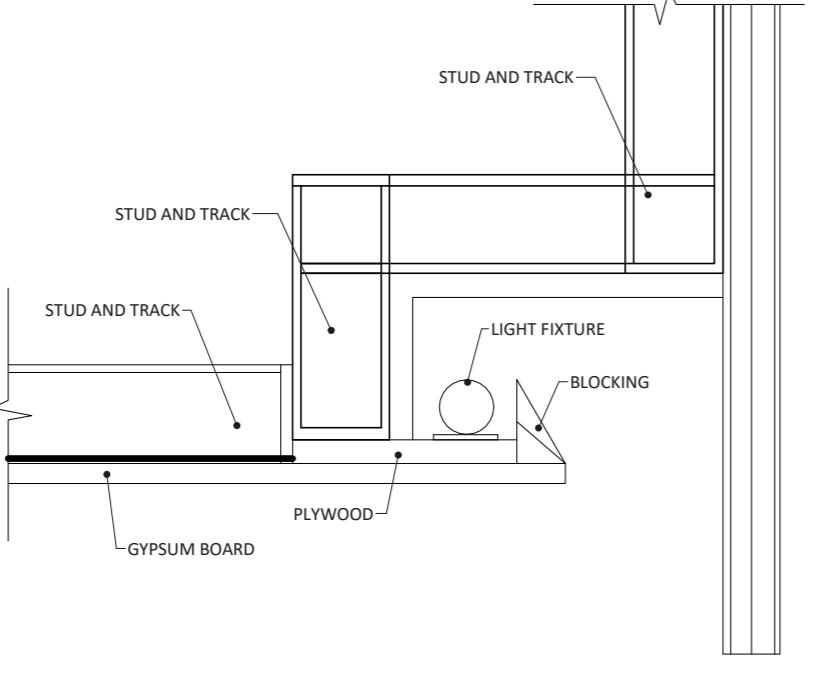1	2	3	4	5	6	7	8	9	10	11	12	13	
													CONSULTANT HELWAN UNIVERSITY 
L	K	J	H	G	F	E	D	C	B	A		L	
 <p>GYPSUM BOARD AND GYPSUM TILE CONNECTION DETAIL 1 01 AE501 SCALE 1:10</p>					 <p>GYPSUM BOARD AND GYPSUM TILE CONNECTION DETAIL 2 02 AE501 SCALE 1:10</p>								OWNER FAP Fine Arts Programs CONTRACTOR SAUD Sustainable Architecture and Urban Design Program REMARKS
													KEY PLAN: 
													STUDENT INFORMATION Mariam Ismail Nouran Ahmed Hazem Khaled
													PROJECT DATA MIXED USE BUILDING
													DISCIPLINE ARCHITECTURE
													SHEET TITLE ARCHITECTURAL TYPES AND DETAILS
													SCALE SHEET NO REV MARK AE502.
1	2	3	4	5	6	7	8	9	10	11	12	13	A
 <p>INDIRECT LIGHT GYPSUM BOARD DETAIL 03 AE501 SCALE 1:10</p>													
<p>Scanning scale 100 mm 50 mm 10 mm</p>													

RECEPTION ENTRANCE STAIRCASE PLAN
SCALE 1:25

RECEPTION ENTRANCE STAIRCASE SECTION
SCALE 1:25

RECEPTION ENTRANCE STAIRCASE 3D

KEY PLAN:

STUDENT INFORMATION: Mariam Ismail, Nouran Ahmed, Hazem Khaled

PROJECT DATA: MIXED USE BUILDING

DISCIPLINE: ARCHITECTURE

SHEET TITLE: ARCHITECTURAL TYPES AND DETAILS

CONSULTANT: HELWAN UNIVERSITY

OWNER: FAP Fine Arts Programs


CONTRACTOR: SAUD Sustainable Architecture and Urban Design Program


REMARKS:

REV DATE ISSUED FOR DRW CHK TL PM

SCALE SHEET NO REV MARK

AE503

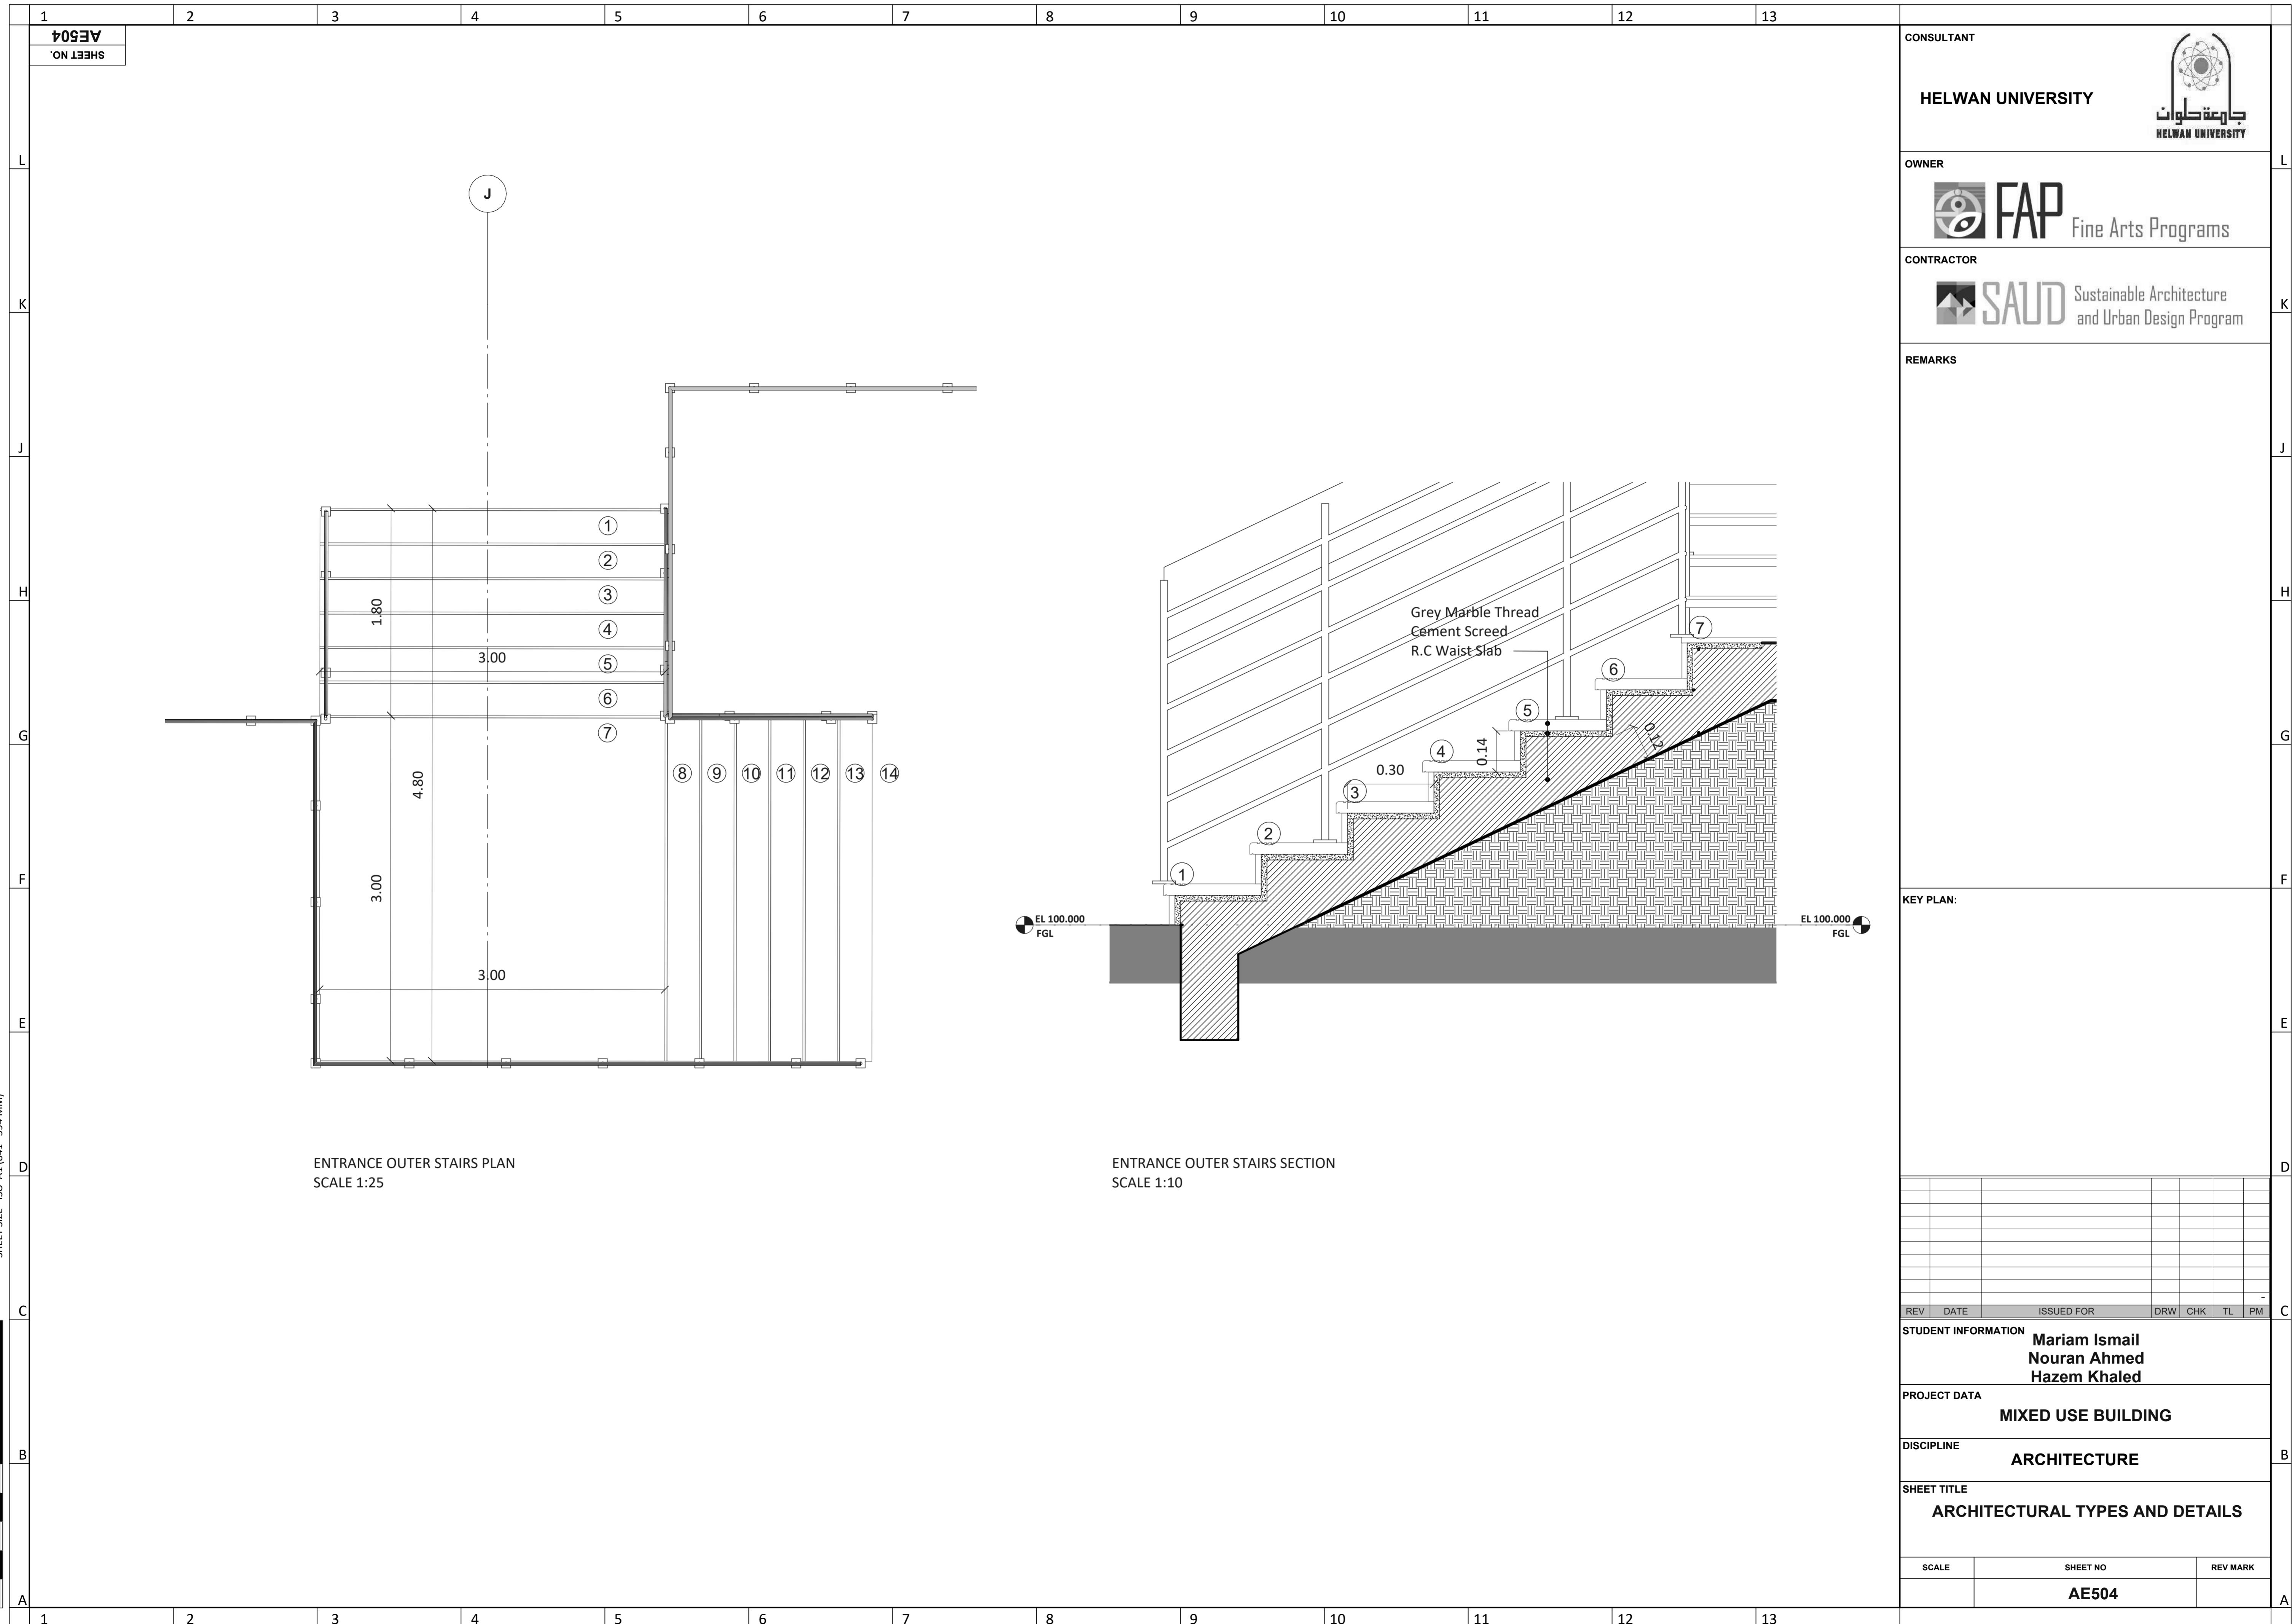

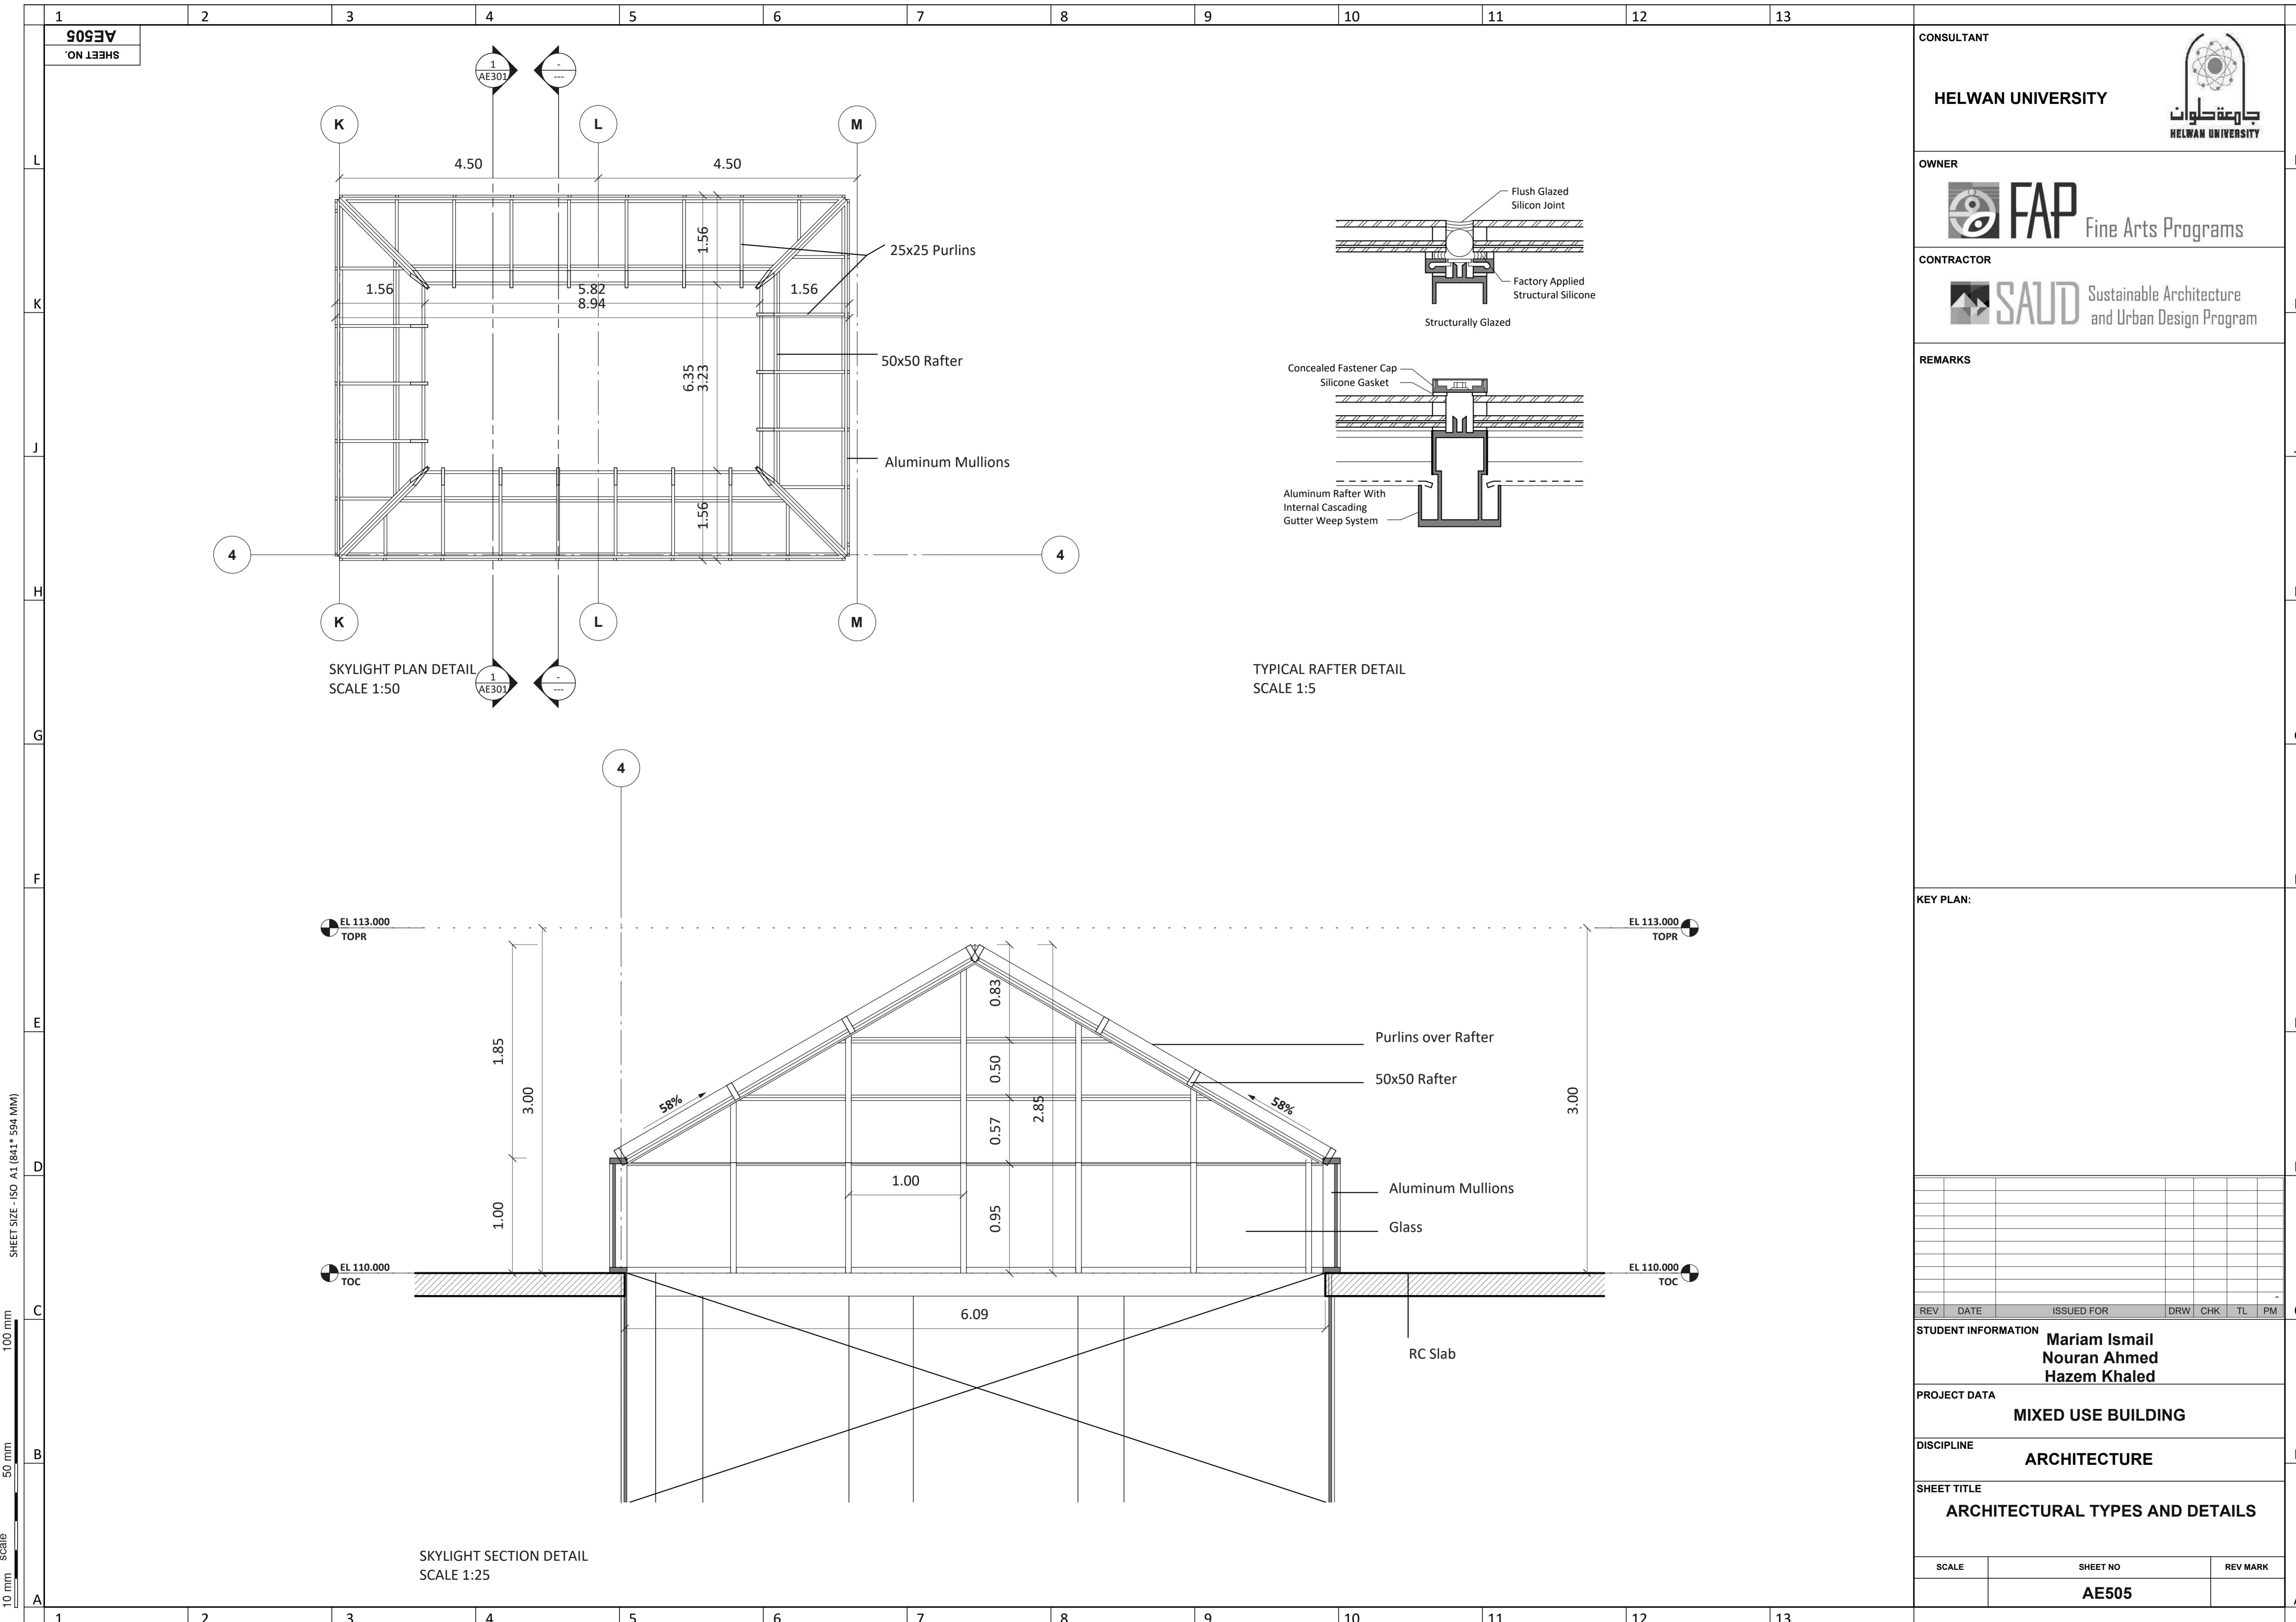

1	2	3	4	5	6	7	8	9	10	11	12	13	CONSULTANT HELWAN UNIVERSITY 	L
A E507 SHEET NO.													OWNER  FAP Fine Arts Programs	L
													CONTRACTOR  SAUD Sustainable Architecture and Urban Design Program	K
													REMARKS	J
														H
														G
														F
														E
														D
														C
														B
														A
1	2	3	4	5	6	7	8	9	10	11	12	13		



MIRROR FIXATION DETAIL
SCALE 1:10




TOILET INSTALLATION DETAIL
SCALE 1:10



HPL FIXATION PLAN
SCALE 1:10

SHEET SIZE - ISO A1 (841+594 MM)
100 mm
50 mm
Scanning scale
10 mm

KEY PLAN:

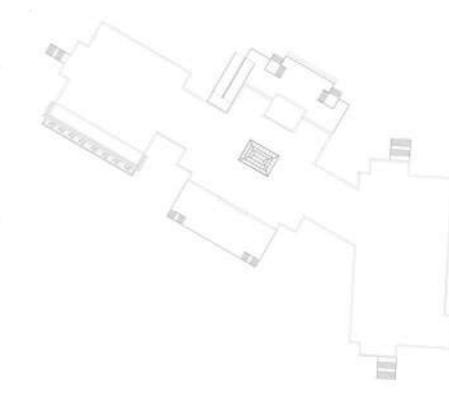

REV	DATE	ISSUED FOR	DRW	CHK	TL	PM
-----	------	------------	-----	-----	----	----

STUDENT INFORMATION
NOURAN AHMED MOHAMED


PROJECT DATA
MALL

DISCIPLINE
ARCHITECTURE

SHEET TITLE
WET AREA CALLOUTS

SCALE	SHEET NO	REV MARK

AE507

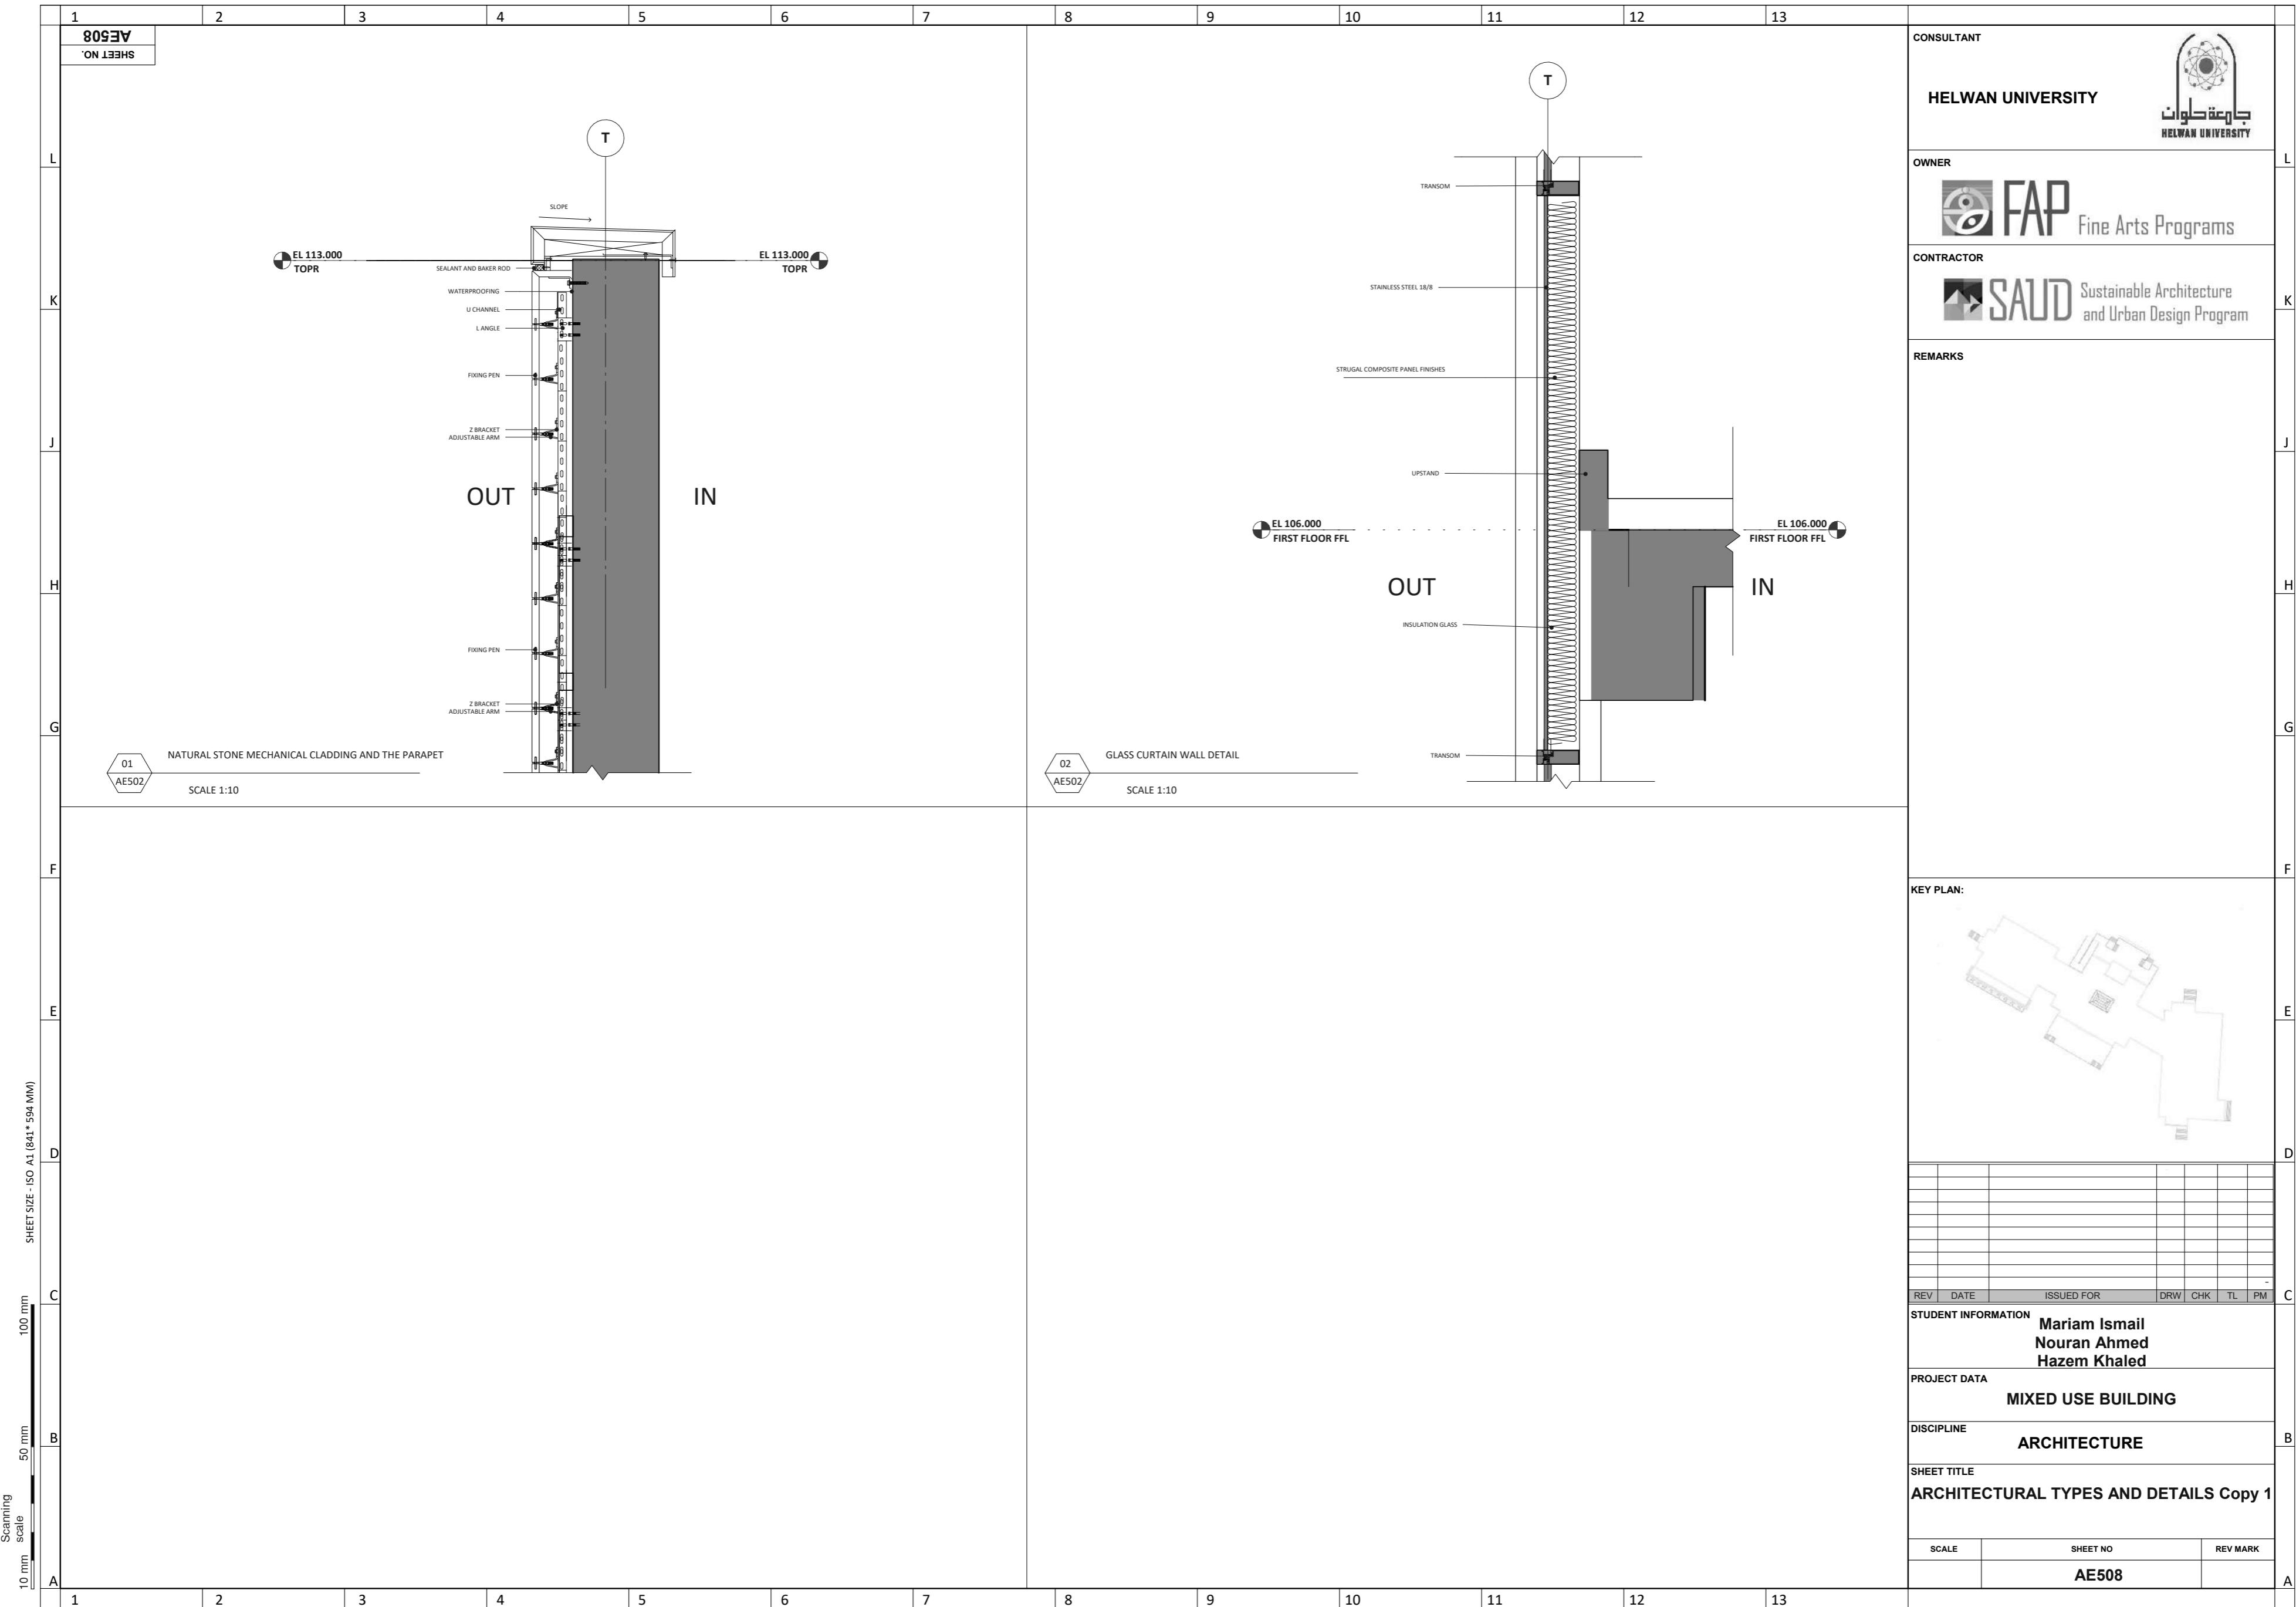

1	2	3	4	5	6	7	8	9	10	11	12	13	
AE509	
SHEET NO.	
L	K	J	H	G	F	E	D	C	B	A	
<p>ELEVATION (WALL PANEL)</p>							<p>SECTION B-B</p> <p>DETAIL OF WALL PANELLING</p>	
<p>SECTION A-A</p>							<p>JOINING DETAIL</p> <p>SECTION SHOWING PANELLING DETAIL</p>	
<p>TYP. CORNER WINDOW TO WALL DETAIL (STONE CLADDING)</p> <p>100mm</p> <p>50mm</p> <p>10mm</p> <p>Scanning scale</p>							<p>TYP. CORNER WALL TO WALL DETAIL (STONE CLADDING)</p>	
<p>TYP. DETAIL FOR GROOVE WITH ALUMINIUM SECTION (STONE CLADDING)</p>							<p>KEY PLAN:</p>	
<p>CONSULTANT HELWAN UNIVERSITY OWNER FAP Fine Arts Programs CONTRACTOR SAUD Sustainable Architecture and Urban Design Program REMARKS</p> <table border="1"> <tr> <td>REV</td><td>DATE</td><td>ISSUED FOR</td><td>DRW</td><td>CHK</td><td>TL</td><td>PM</td></tr> <tr> <td colspan="7">STUDENT INFORMATION Mariam Ismail Nouran Ahmed Hazem Khaled</td></tr> <tr> <td colspan="7">PROJECT DATA MIXED USE BUILDING</td></tr> <tr> <td colspan="7">DISCIPLINE ARCHITECTURE</td></tr> <tr> <td colspan="7">SHEET TITLE CLADDING AND PANELING DETAIL</td></tr> <tr> <td>SCALE</td><td colspan="2">SHEET NO</td><td colspan="2">REV MARK</td><td colspan="3"></td></tr> <tr> <td></td><td colspan="2">AE509</td><td colspan="2"></td><td colspan="3"></td></tr> </table>													REV	DATE	ISSUED FOR	DRW	CHK	TL	PM	STUDENT INFORMATION Mariam Ismail Nouran Ahmed Hazem Khaled							PROJECT DATA MIXED USE BUILDING							DISCIPLINE ARCHITECTURE							SHEET TITLE CLADDING AND PANELING DETAIL							SCALE	SHEET NO		REV MARK						AE509							A
REV	DATE	ISSUED FOR	DRW	CHK	TL	PM	
STUDENT INFORMATION Mariam Ismail Nouran Ahmed Hazem Khaled	
PROJECT DATA MIXED USE BUILDING	
DISCIPLINE ARCHITECTURE	
SHEET TITLE CLADDING AND PANELING DETAIL	
SCALE	SHEET NO		REV MARK	
	AE509	
1	2	3	4	5	6	7	8	9	10	11	12	13	

1 2 3 4 5 6 7 8 9 10 11 12 13
 SHEET NO. AE510
 L K J H G F E D C B A
 100mm
 50mm
 10mm
 Scanning scale

DETAIL X

 SS FASTNER
 50X50X3 BOX SECTION WELDED OVER MS SECTION
 25 MM DIA STUD
 75X75X6 SS ANGLE
 75X50X3 BOX SECTION SCREWED OVER SS ANGLE
 2950X1200X13.52 MM THK. GLASS PANEL AS DETAIL
 FALSE CEILING
 ACCESS HATCH PANEL
 2950X1200X13.52 MM THK. GLASS PANEL AS DETAIL

SECTION A-A
TYPICAL WALL CLADDING DETAIL

 D-WALL AS STRUCTURE
 SS FASTNER
 75X75X6 SS ANGLE
 75X50X3 BOX SECTION SCREWED OVER SS ANGLE
 25 MM DIA STUD
 BLOCK WALL
 2950X1200X13.52 MM THK. GLASS PANEL AS DETAIL
 50X50X3 BOX SECTION WELDED OVER MS SECTION
 SS SHEET SCREW AT END
 25X35X5 MM THK. ALUMINIUM BOX SECTION
 3 MM THK. SS GRANDE304 MATTE FINISHED SS CLADDING SHEET
 GRANITE FLOORING AS DETAIL
 200 MM WIDE SCUPPER DRAIN AB PLUMBING
 75X50X3 BOX SECTION SCREWED OVER SS ANGLE
 2950X1200X13.52 MM THK. GLASS PANEL AS DETAIL
 50X50X3 BOX SECTION WELDED OVER MS SECTION
 TOE WALL
 75X75X6 SS ANGLE
 D-WALL AS STRUCTURE
 ACCESS HATCH PANEL
 25X35X5 MM THK. ALUMINIUM BOX SECTION
 3 MM THK. SS GRANDE304 MATTE FINISHED SS CLADDING SHEET

PLAN TYPICAL WALL CLADDING DETAIL

 APPROVED WATERPROOFING
 200 MM WIDE SCUPPER DRAIN AB PLUMBING
DETAIL Y

CONSULTANT
HELWAN UNIVERSITY

OWNER
FAP Fine Arts Programs
CONTRACTOR
SAUD Sustainable Architecture and Urban Design Program
REMARKS

KEY PLAN:

REV	DATE	ISSUED FOR	DRW	CHK	TL	PM
STUDENT INFORMATION Mariam Ismail Nouran Ahmed Hazem Khaled						
PROJECT DATA MIXED USE BUILDING						
DISCIPLINE ARCHITECTURE						
SHEET TITLE WALL CLADDING DETAIL						
SCALE	SHEET NO	REV MARK				
	AE510					